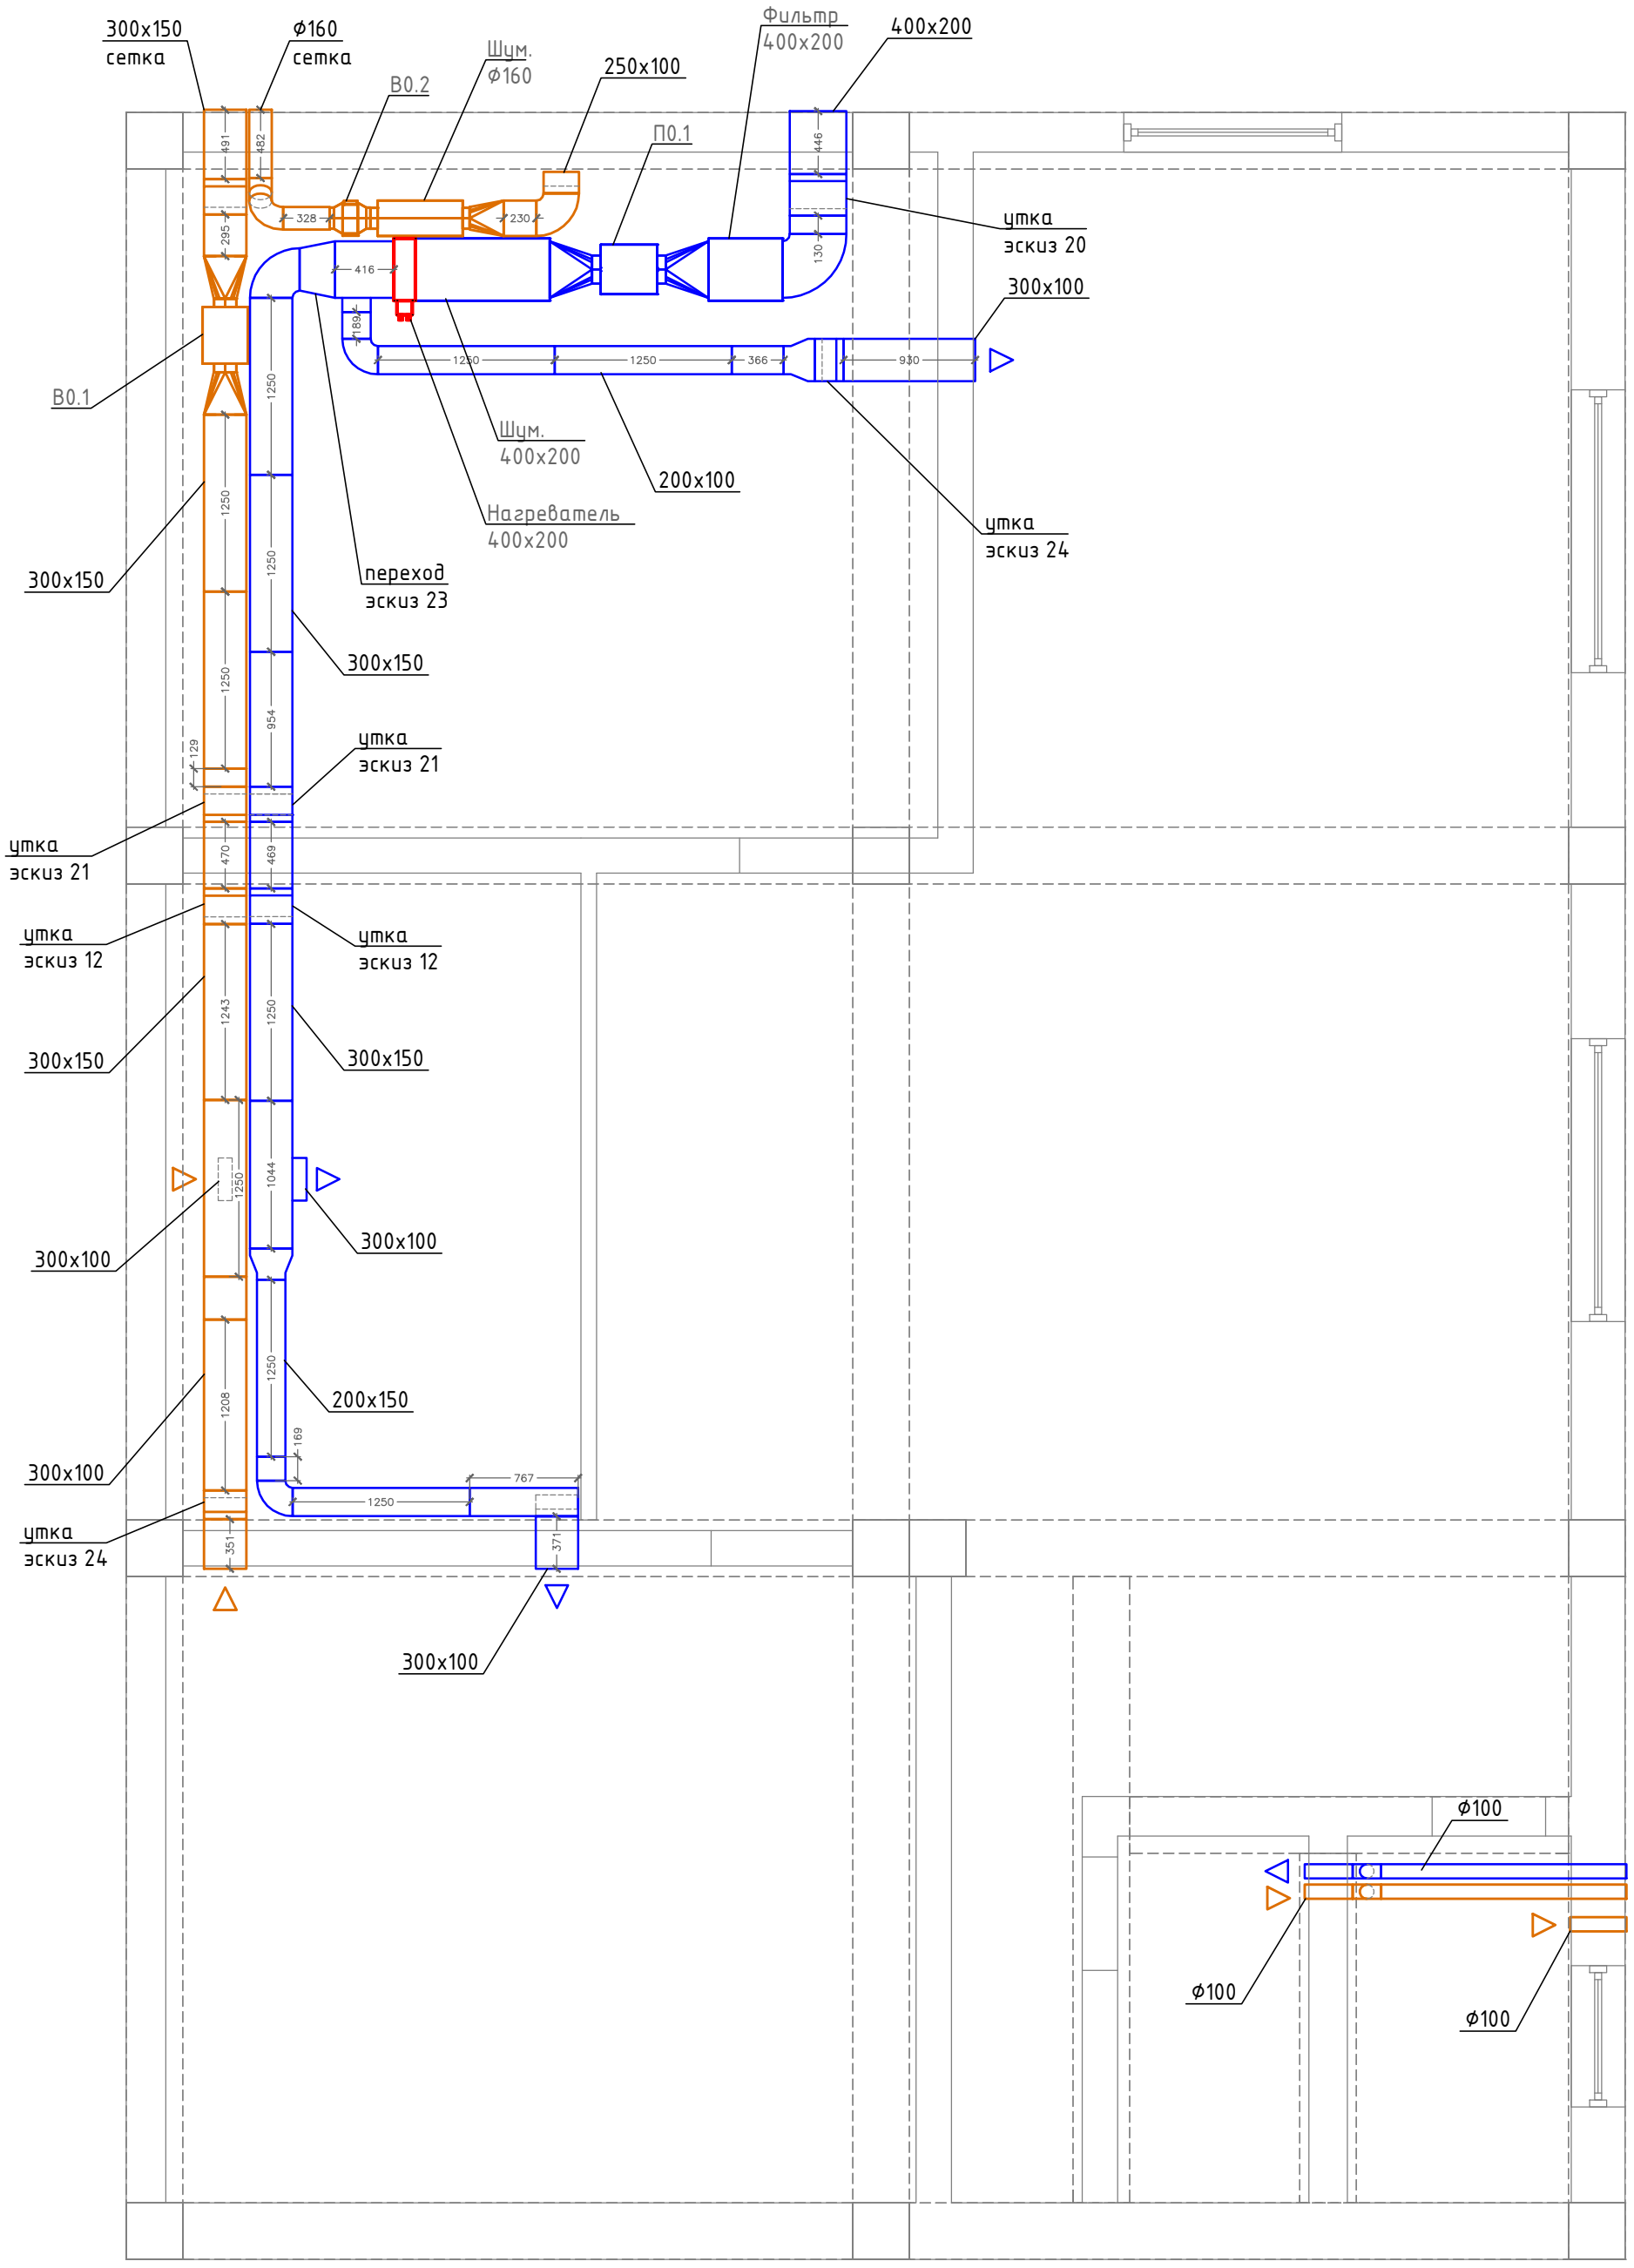

План систем вентиляции. Цокольный этаж

Согласовано

Взам. инв. №

Подпись и дата

Инв. № подл.

Копировал

Формат А3

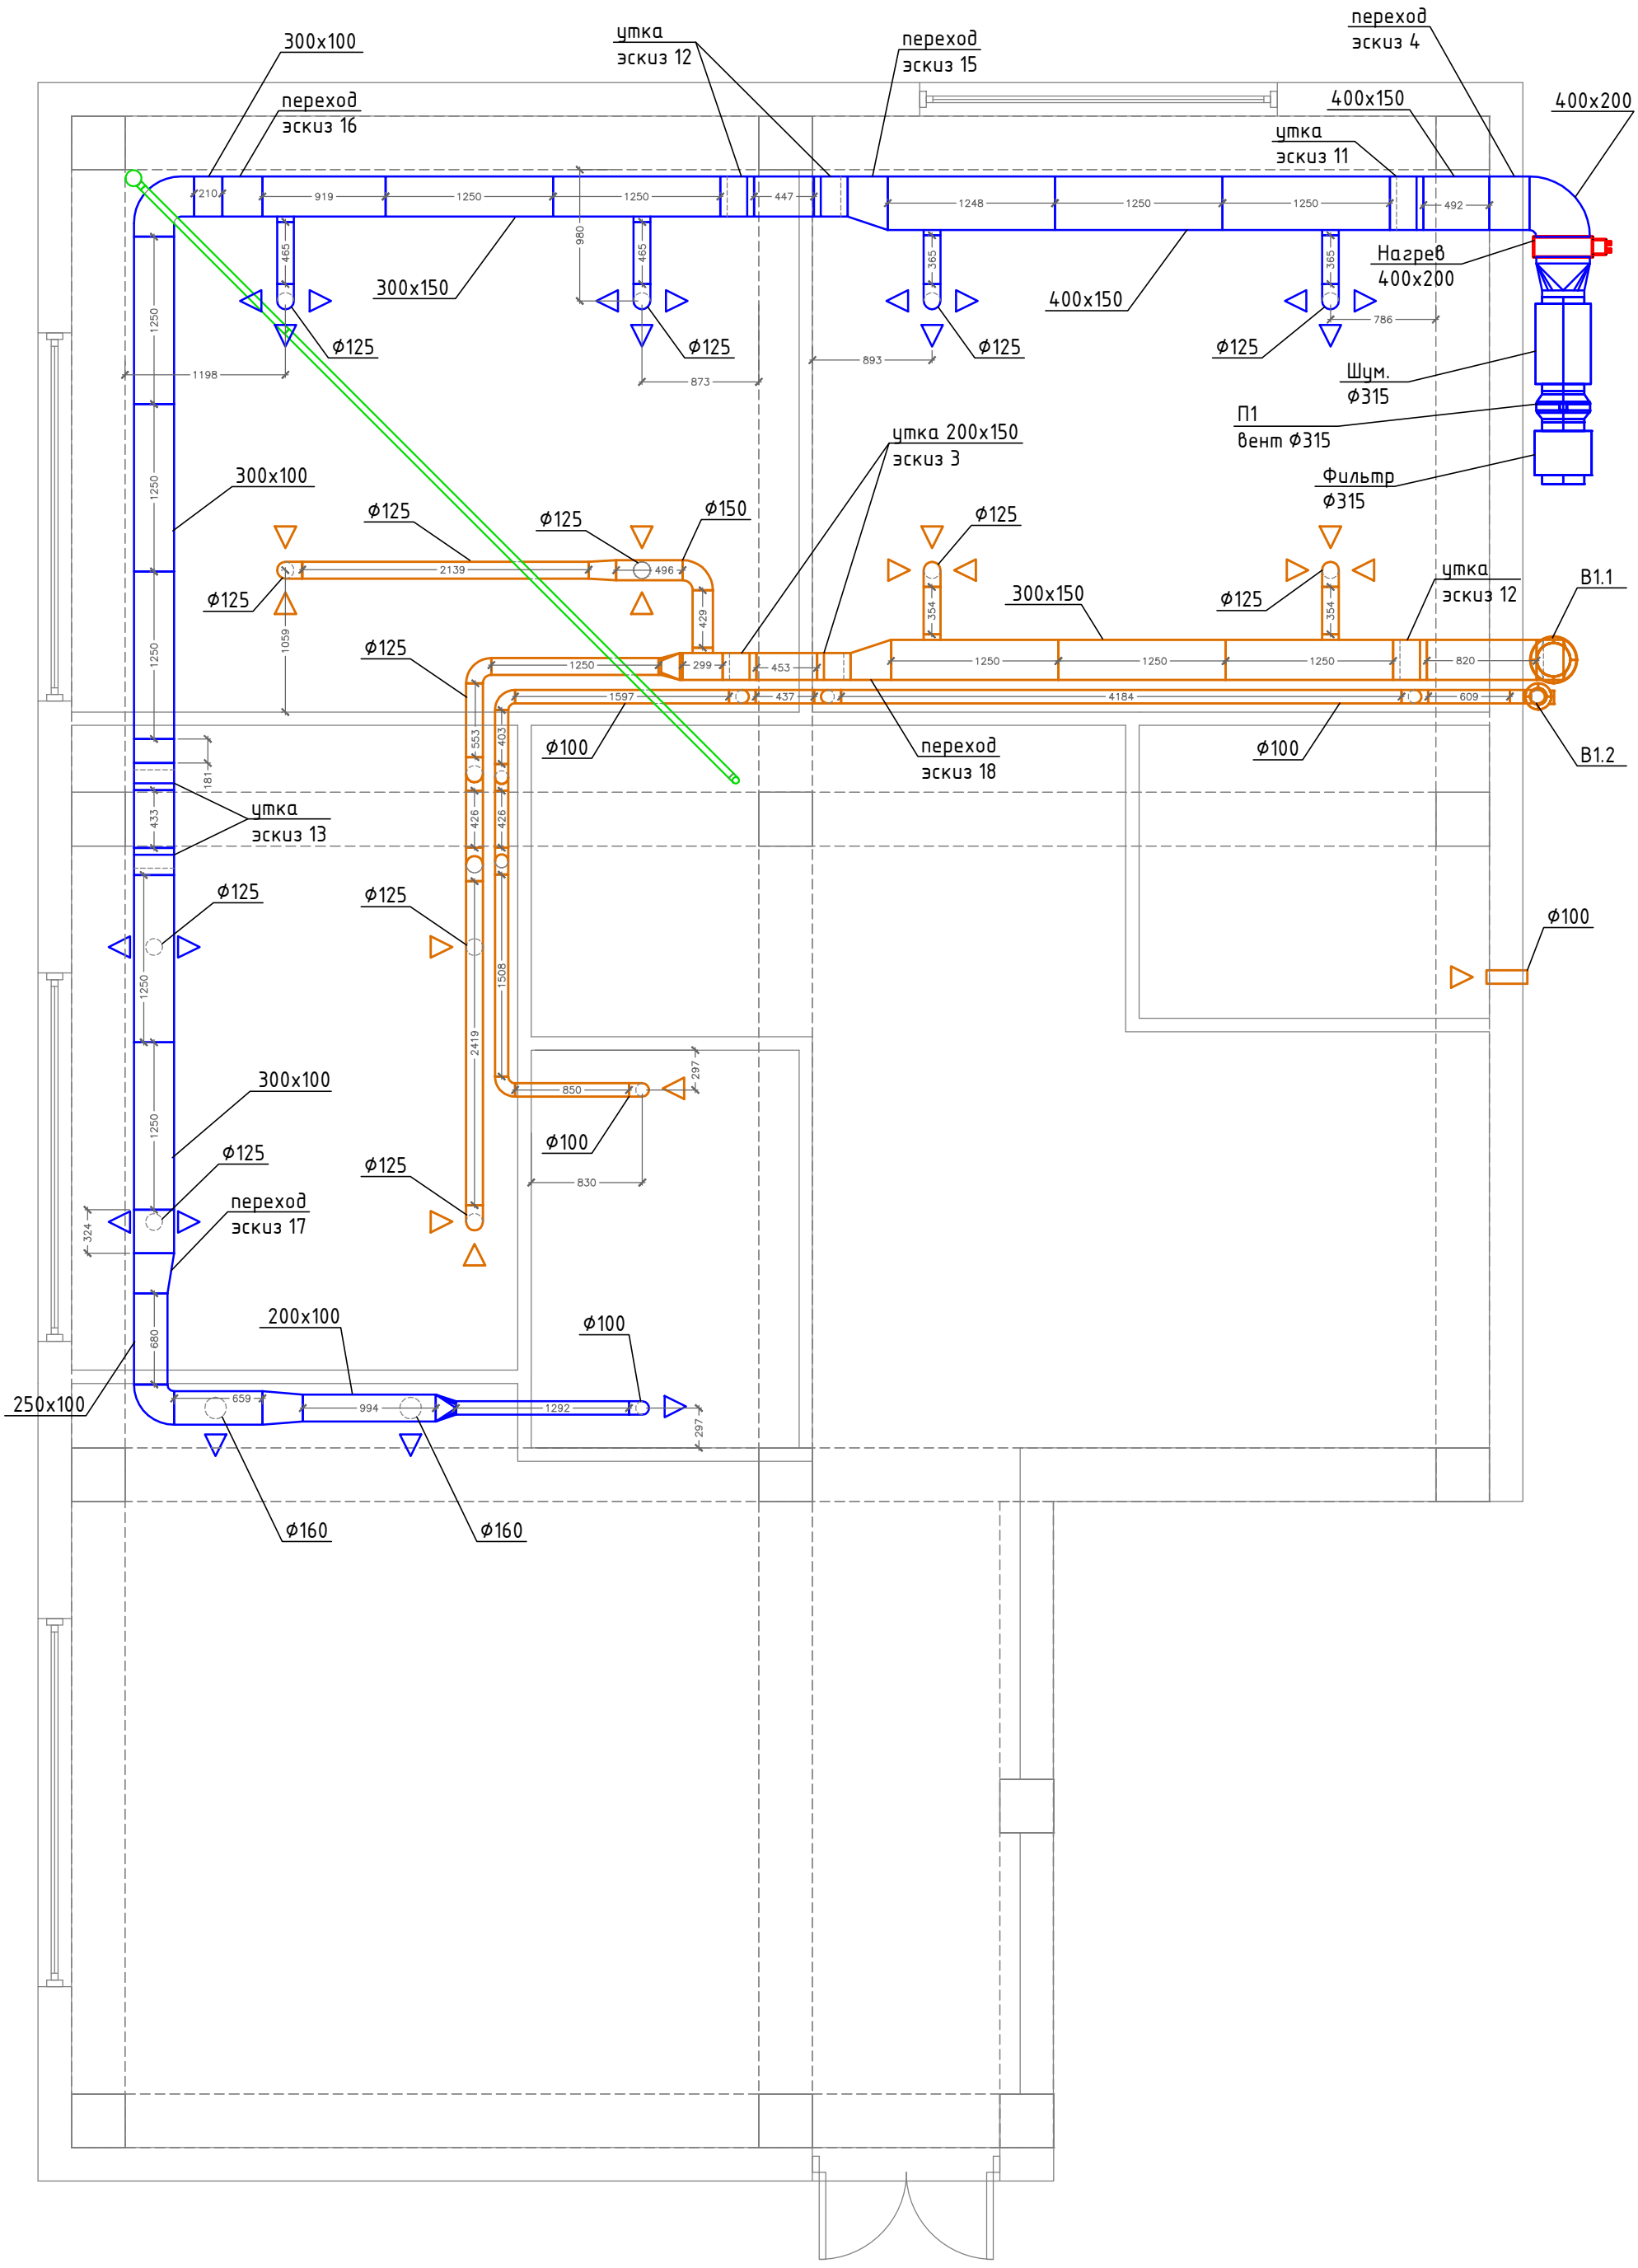

План систем вентиляции. Первый этаж

Согласовано

Взам. инв. №

Подпись и дата

Инв. № подл.

Копировал

Формат А3

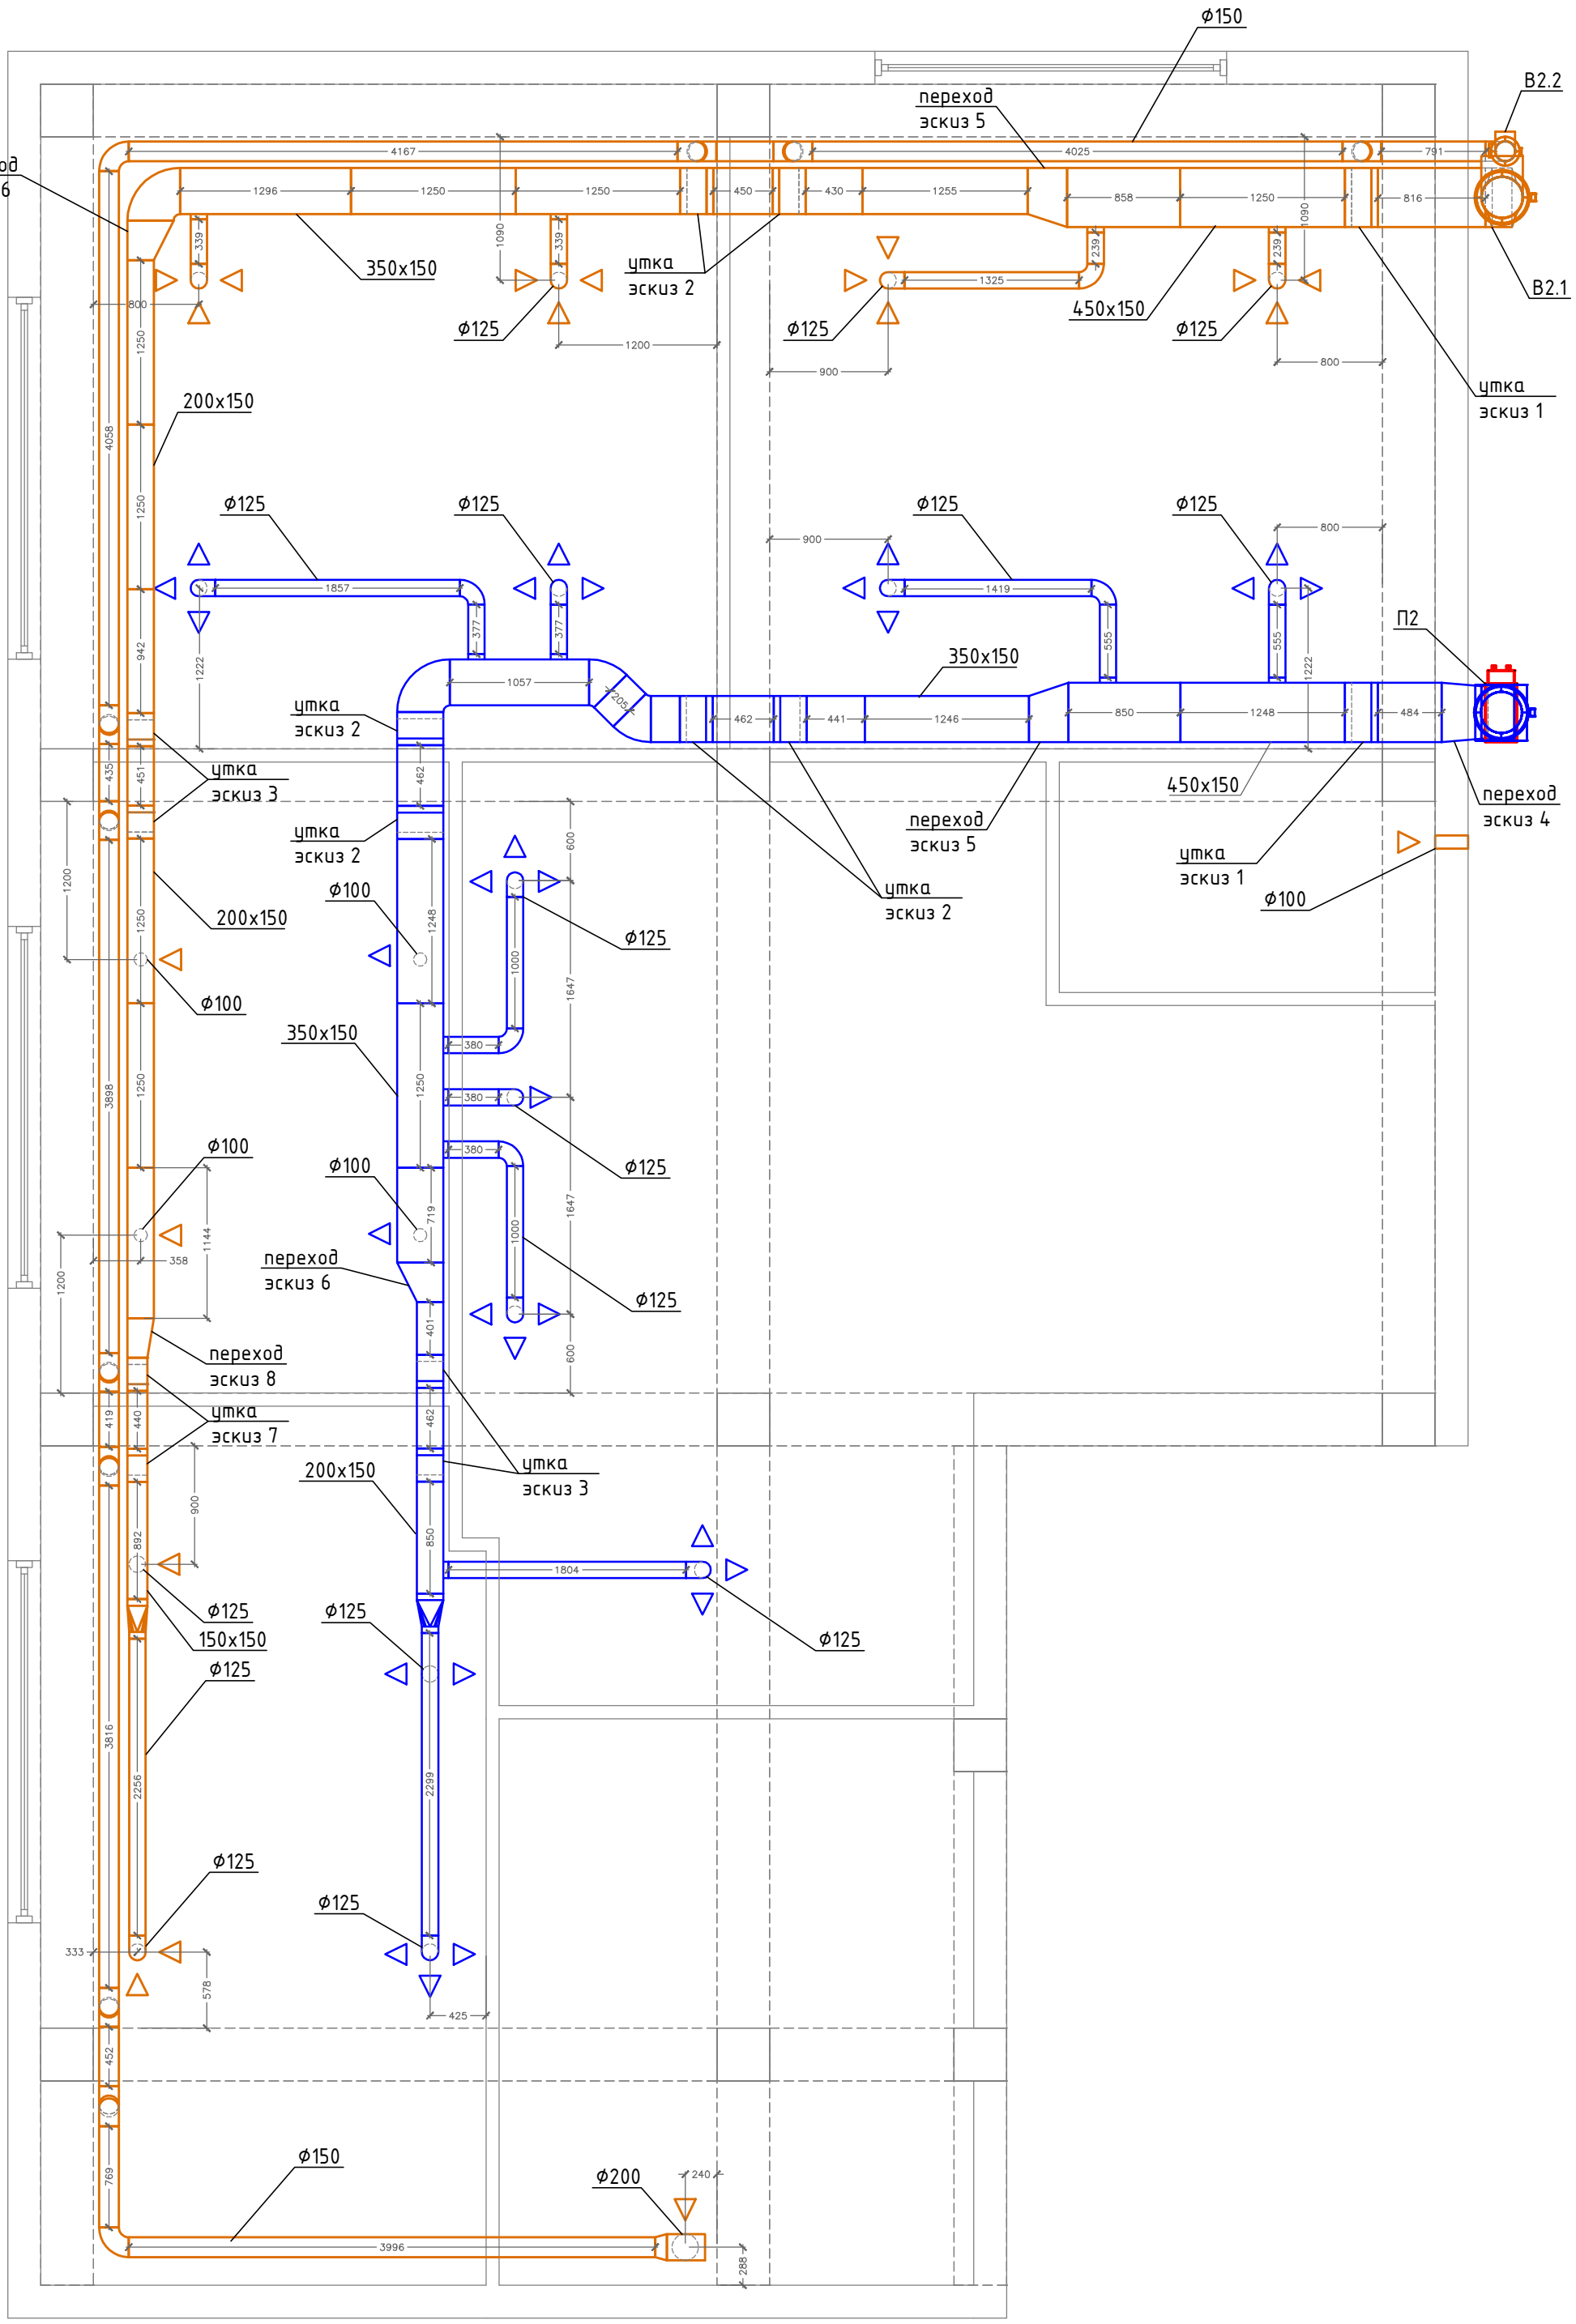

План систем вентиляции. Второй этаж

Согласовано

Взам. инв. №

Подпись и дата

Инв. № подл.

Копировал

Формат А3

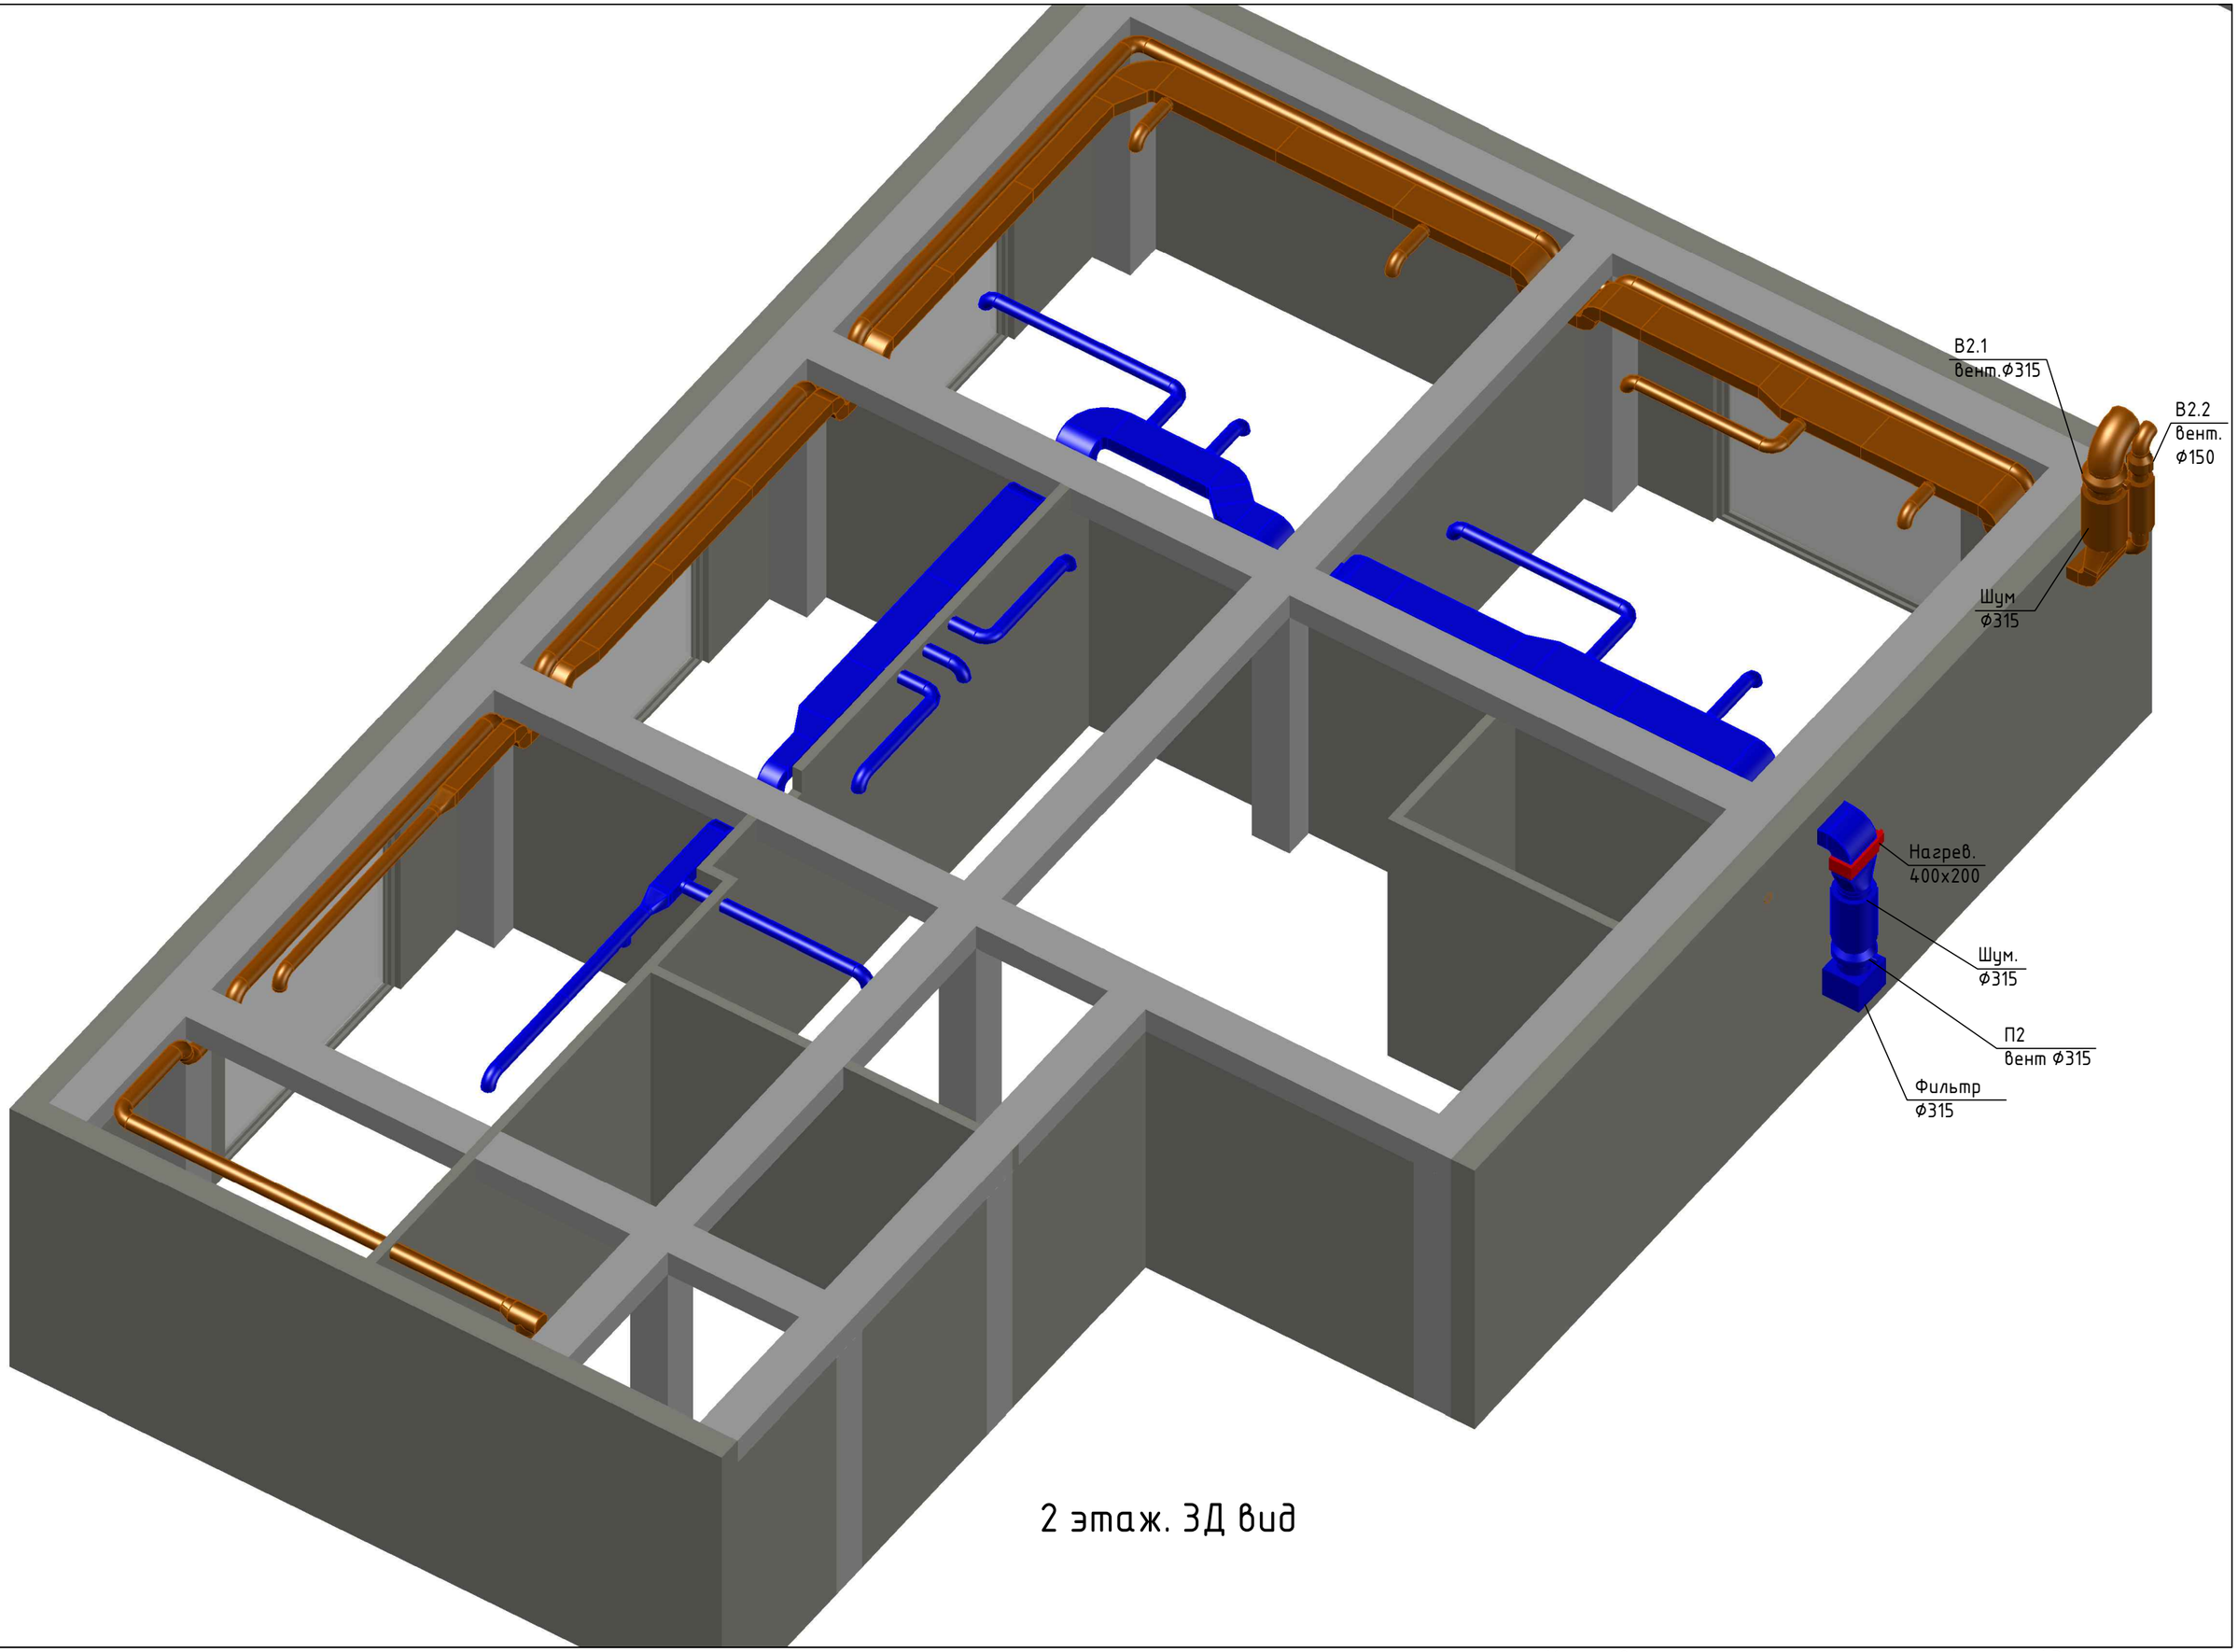

2 этаж. 3Д вид

Согласовано

Взам. инв. №

Подпись и дата

Инв. № подл.

Копировал

Формат А3

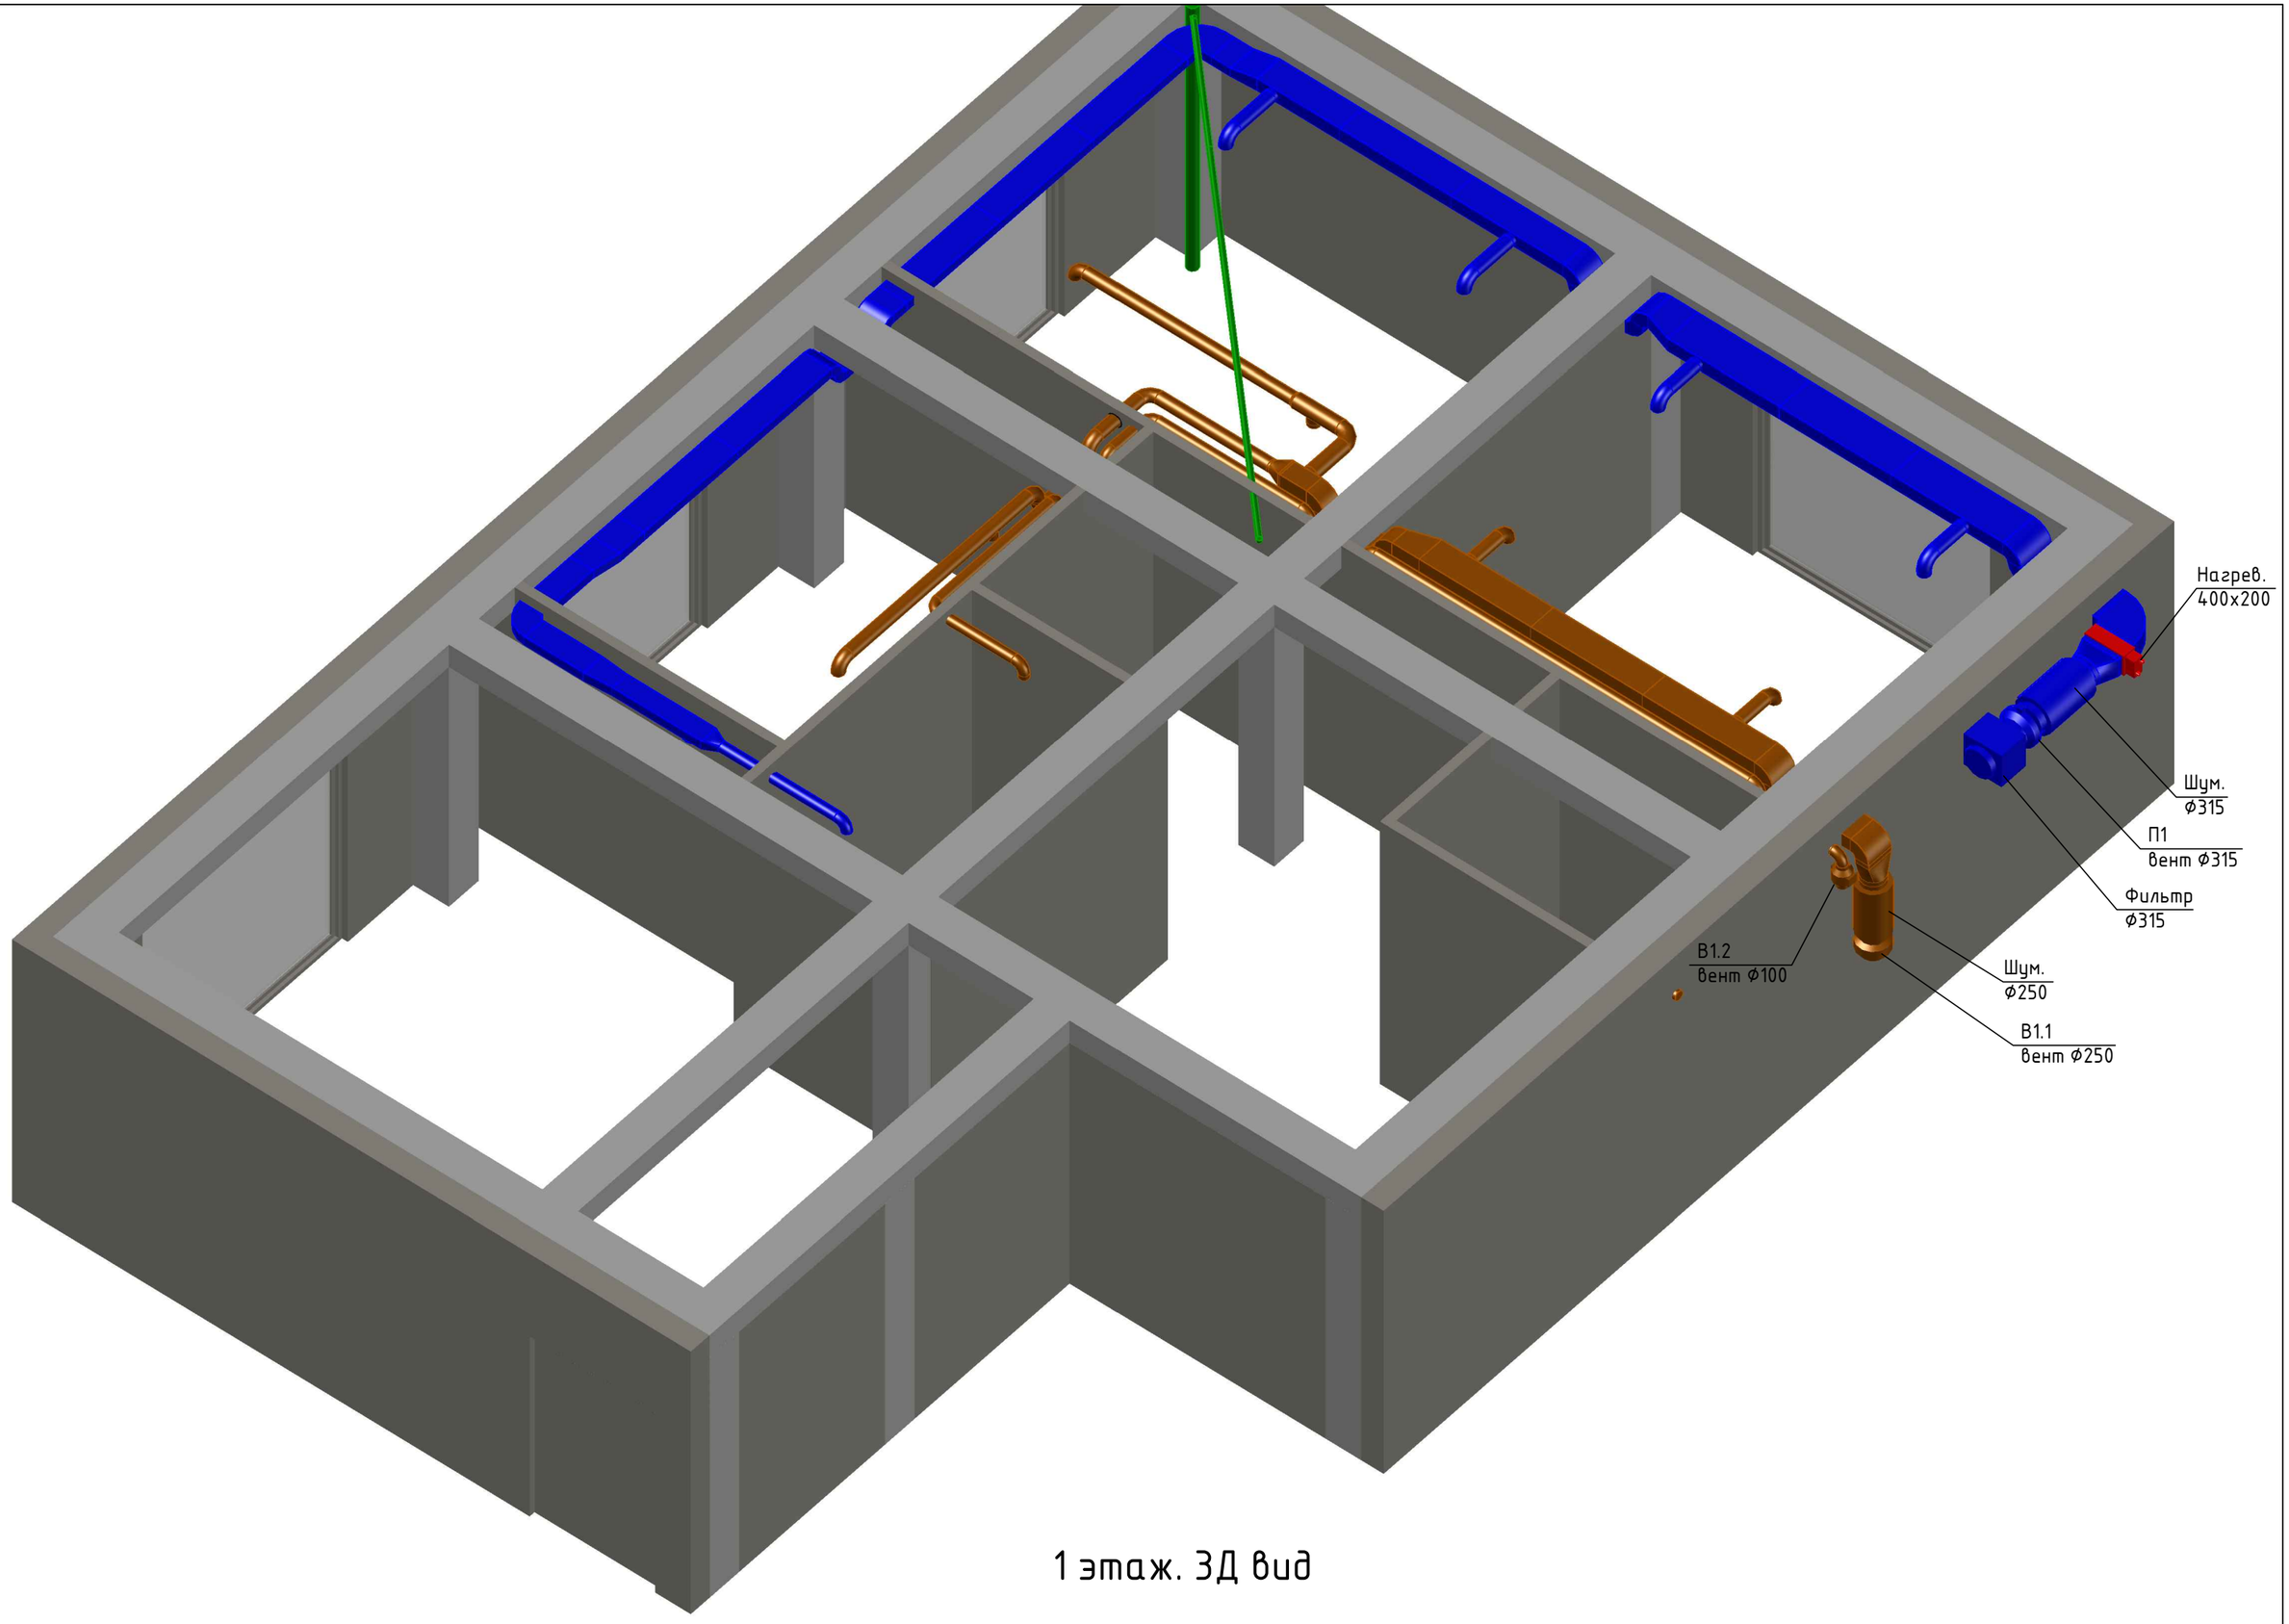

1 этаж. 3Д вид

Согласовано

Взам. инв. №

Подпись и дата

Инв. № подл.

Копировал

Формат А3

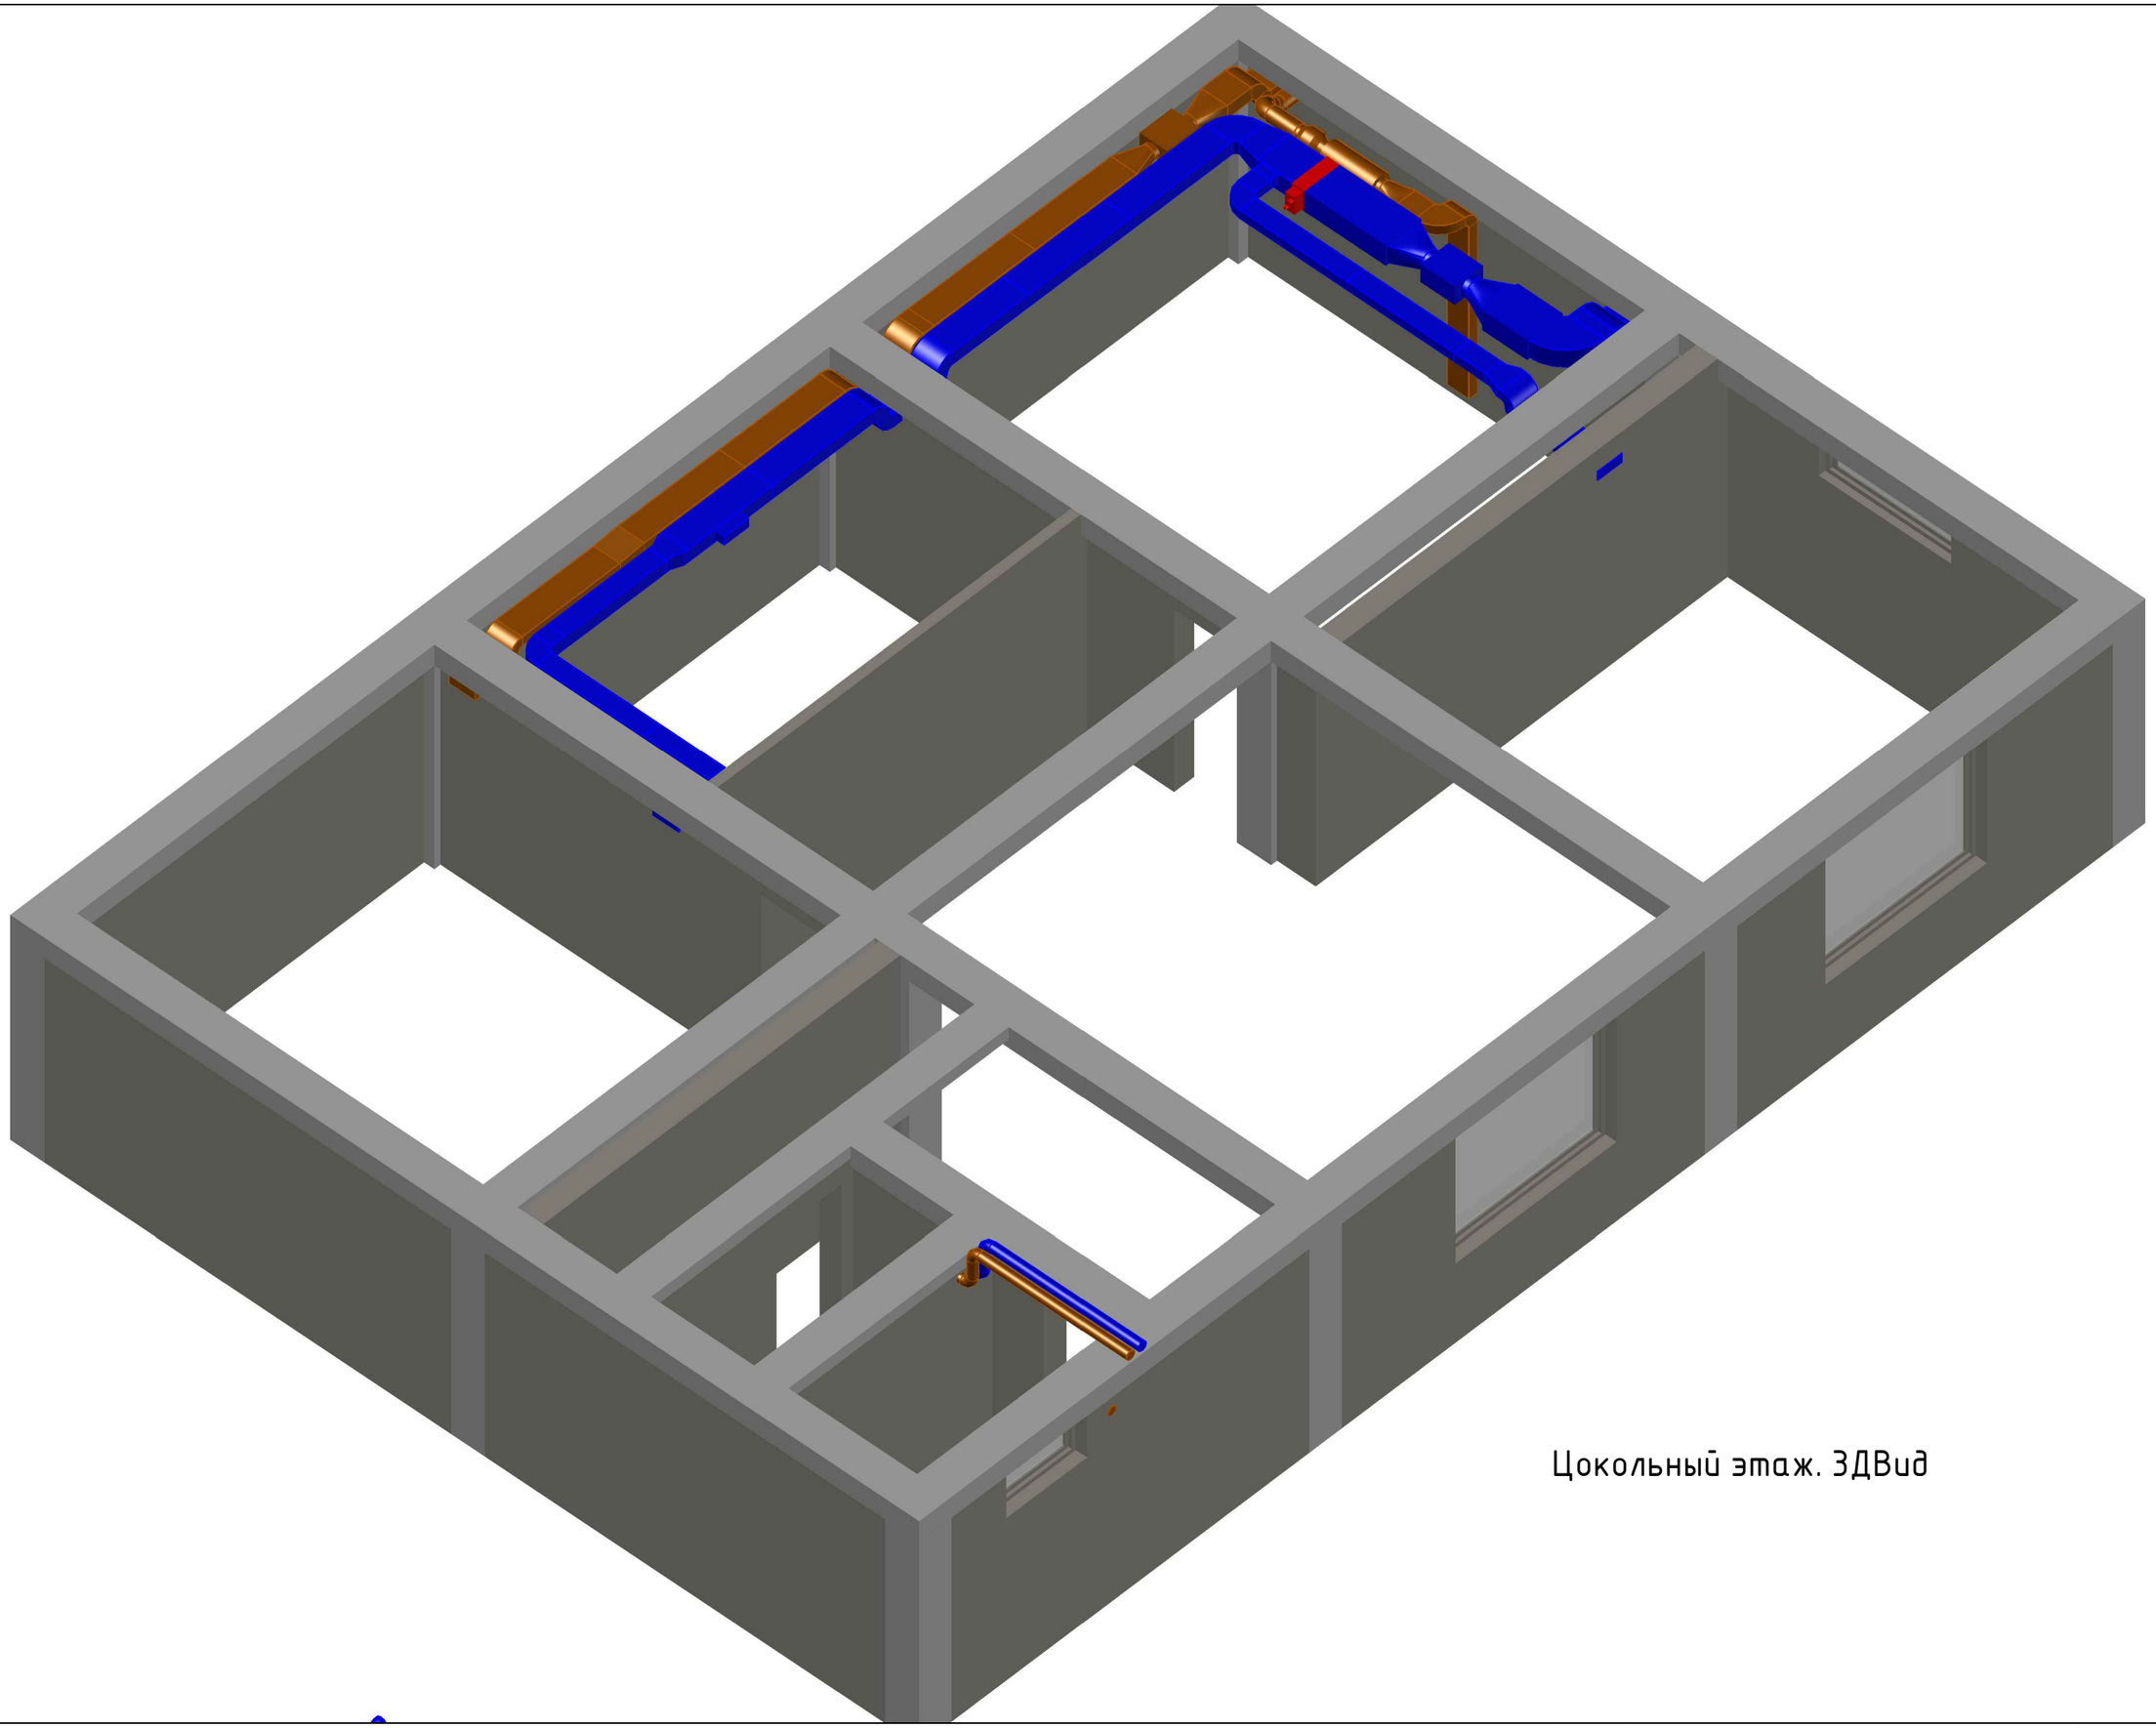

Цокольный этаж. 3ДВид

Согласовано

Взам. инв. №

Подпись и дата

Инв. № подл.

Копировал

Формат А3