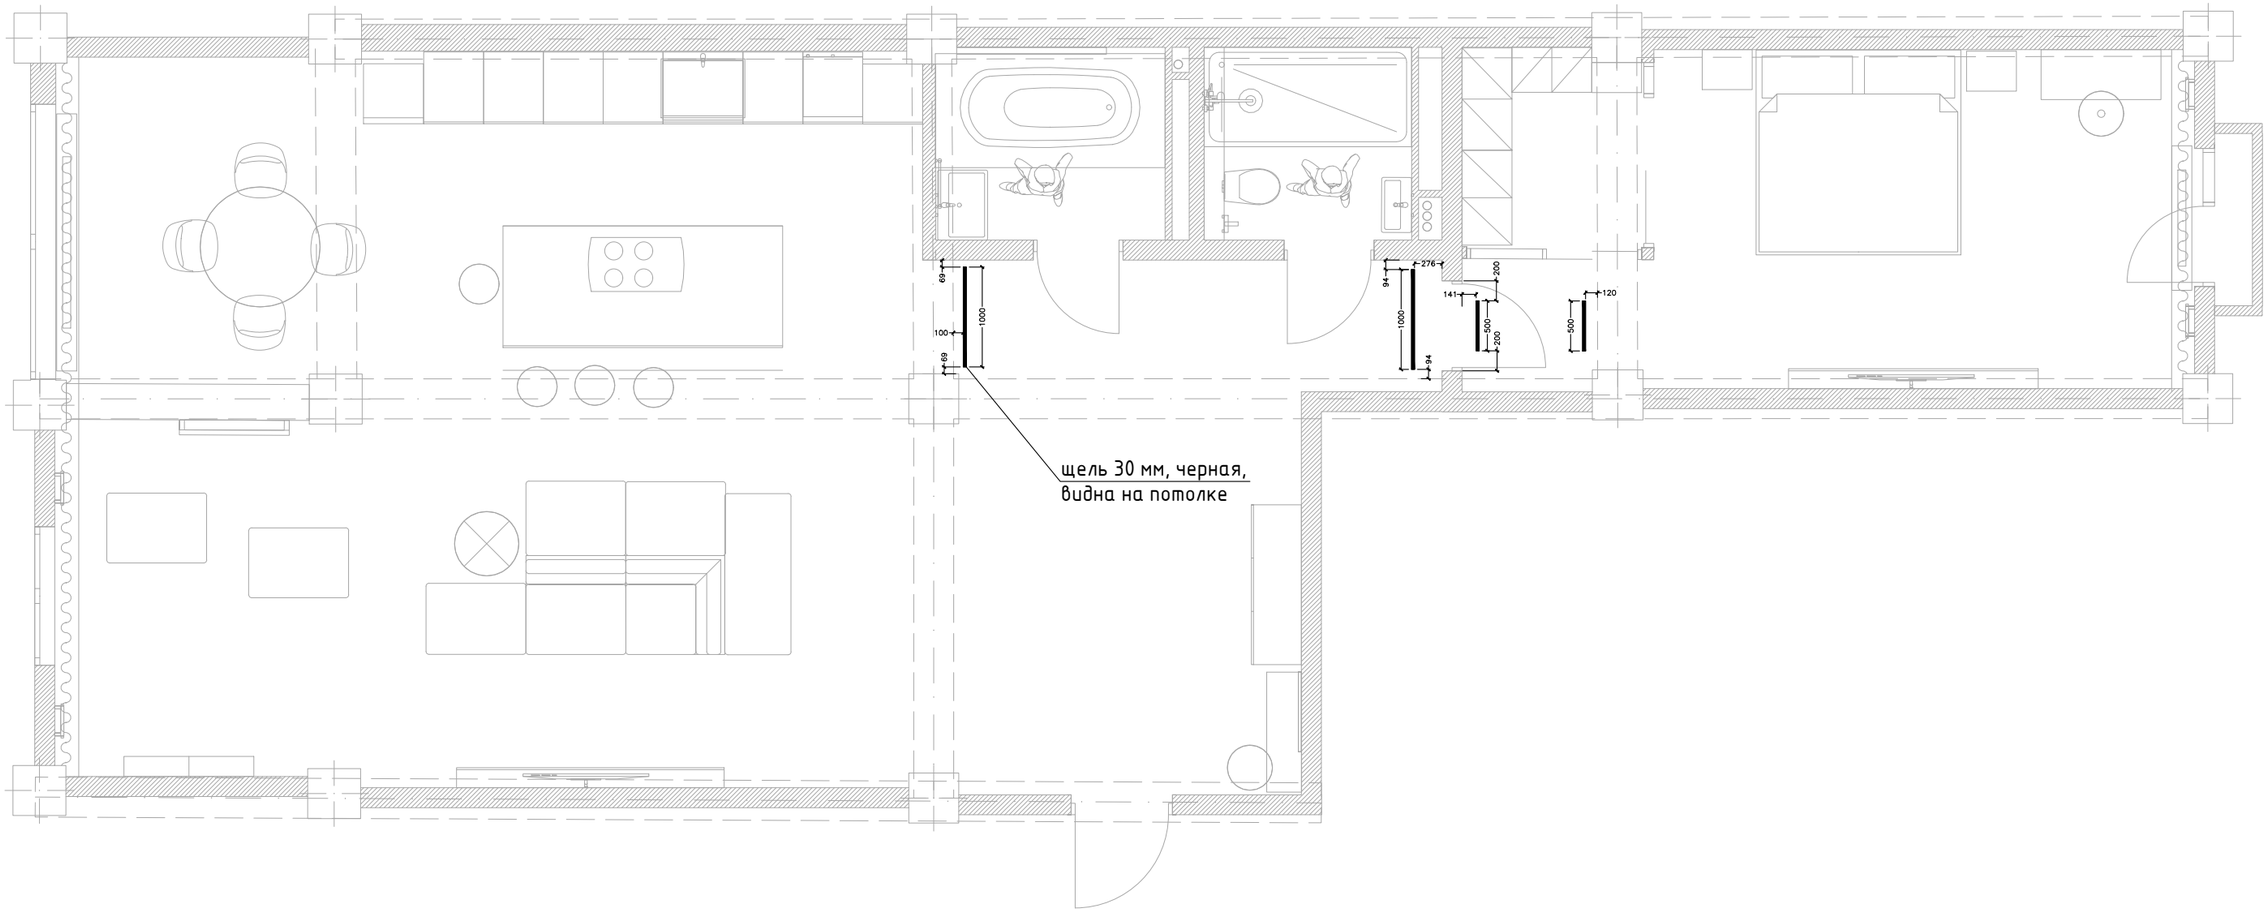

Согласовано

Взам. инв. №

Подпись и дата

Инв. № подл.

						ПД.03.2024-ОВ-КВ-МХ
						Разработка проектной документации по вентиляции.
Изм.	Кол. уч.	Лист	№ док.	Подп.	Дата	

Разработал	Гаджимирзоев			Квартира. Республика Дагестан, г. Махачкала, ул. Абубакарова, 67а	Стадия: П; Лист: ; Листов:
Проверил					
ГИП				План щелевых диффузоров на потолке	
Н.контроль					

Копировал

Формат А3

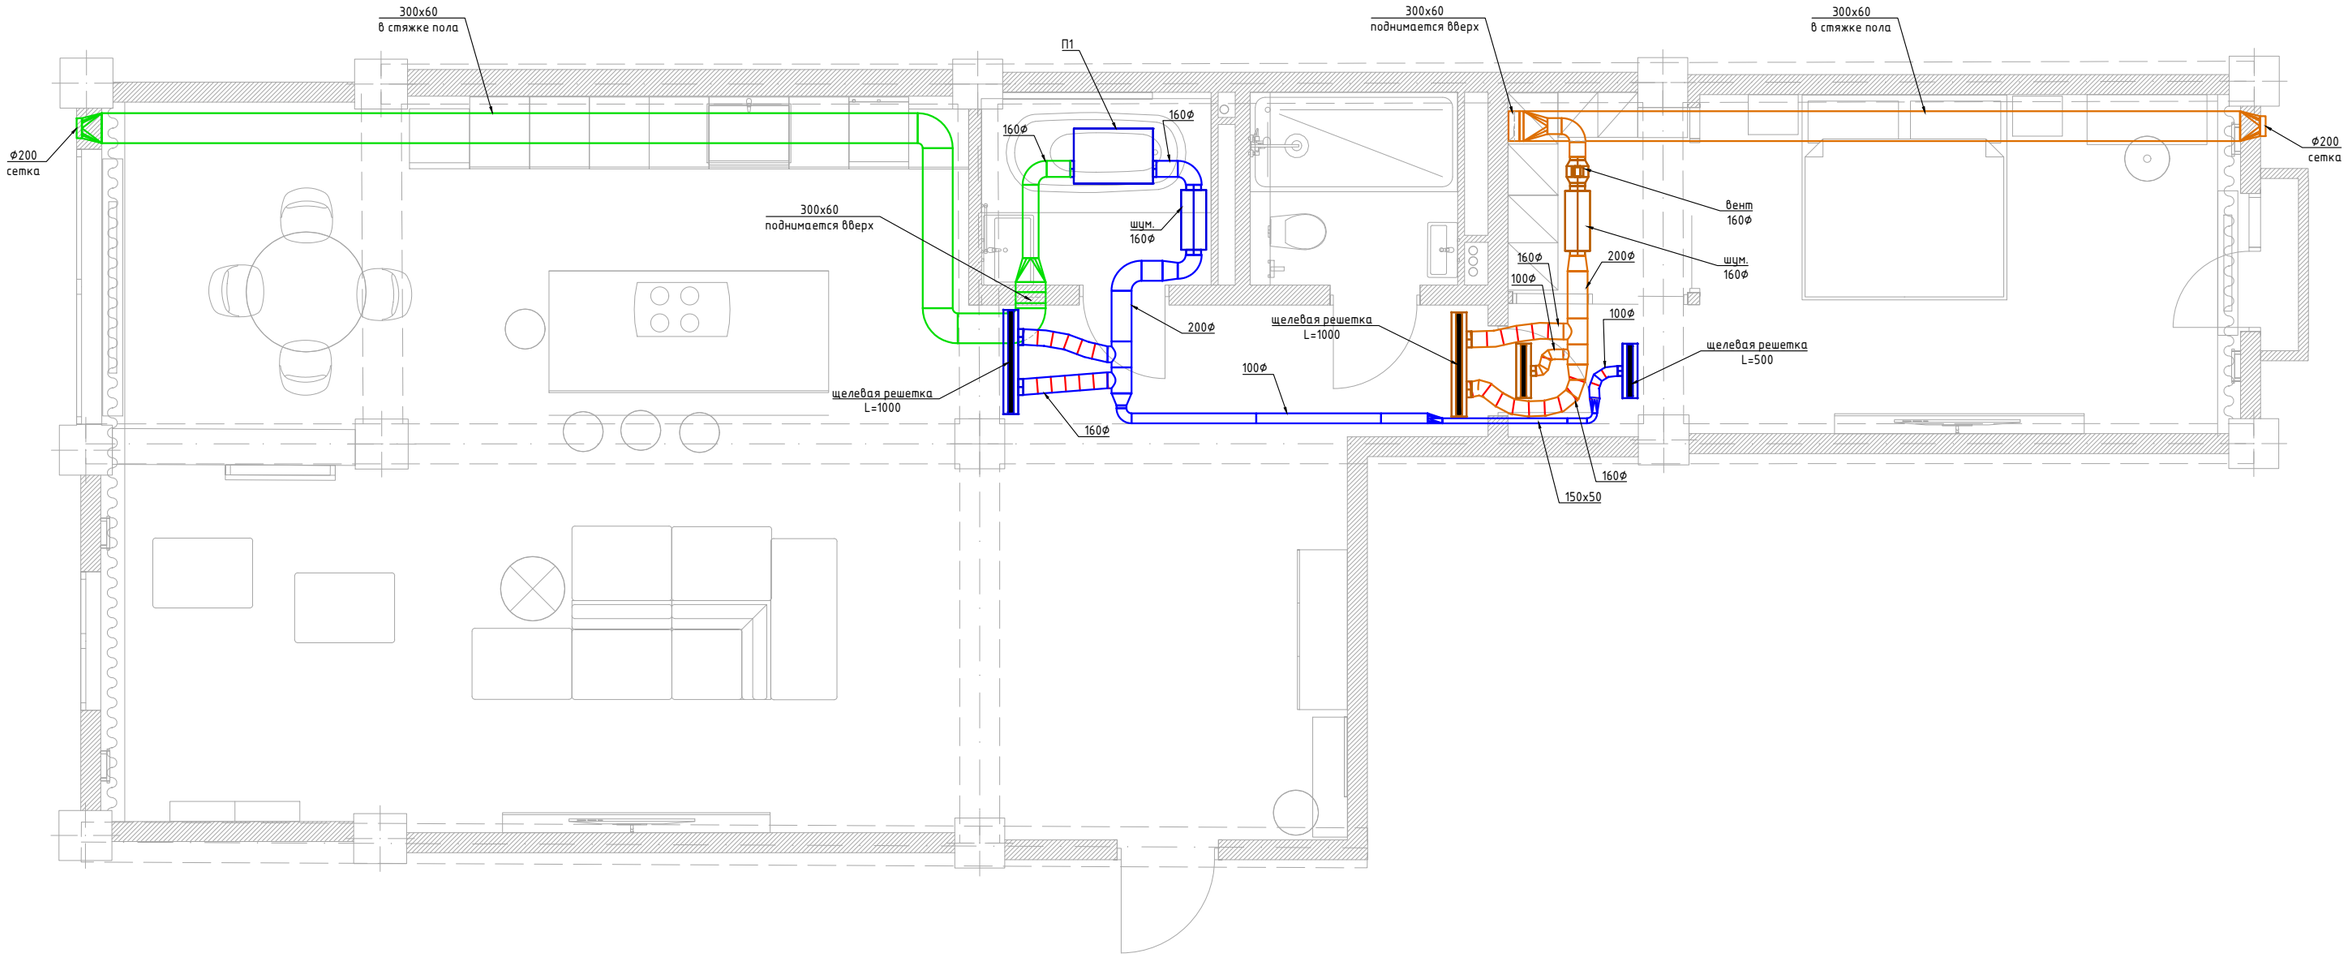

Согласовано

Взам. инв. №

Подпись и дата

Инв. № подл.

						ПД.03.2024-ОВ-КВ-МХ
						Разработка проектной документации по вентиляции.
Изм.	Кол. уч.	Лист	№ док.	Подп.	Дата	
Разработал		Гаджимирзоев				Квартира. Республика Дагестан, г. Махачкала, ул. Абубакарова, 67а
Проверил						
ГИП						План системы вентиляции.
Н.контроль						

Стадия	Лист	Листов
П		

Копировал

Формат А3

Инв. № подл.	Подпись и дата	Взам. инв. №

Согласовано			

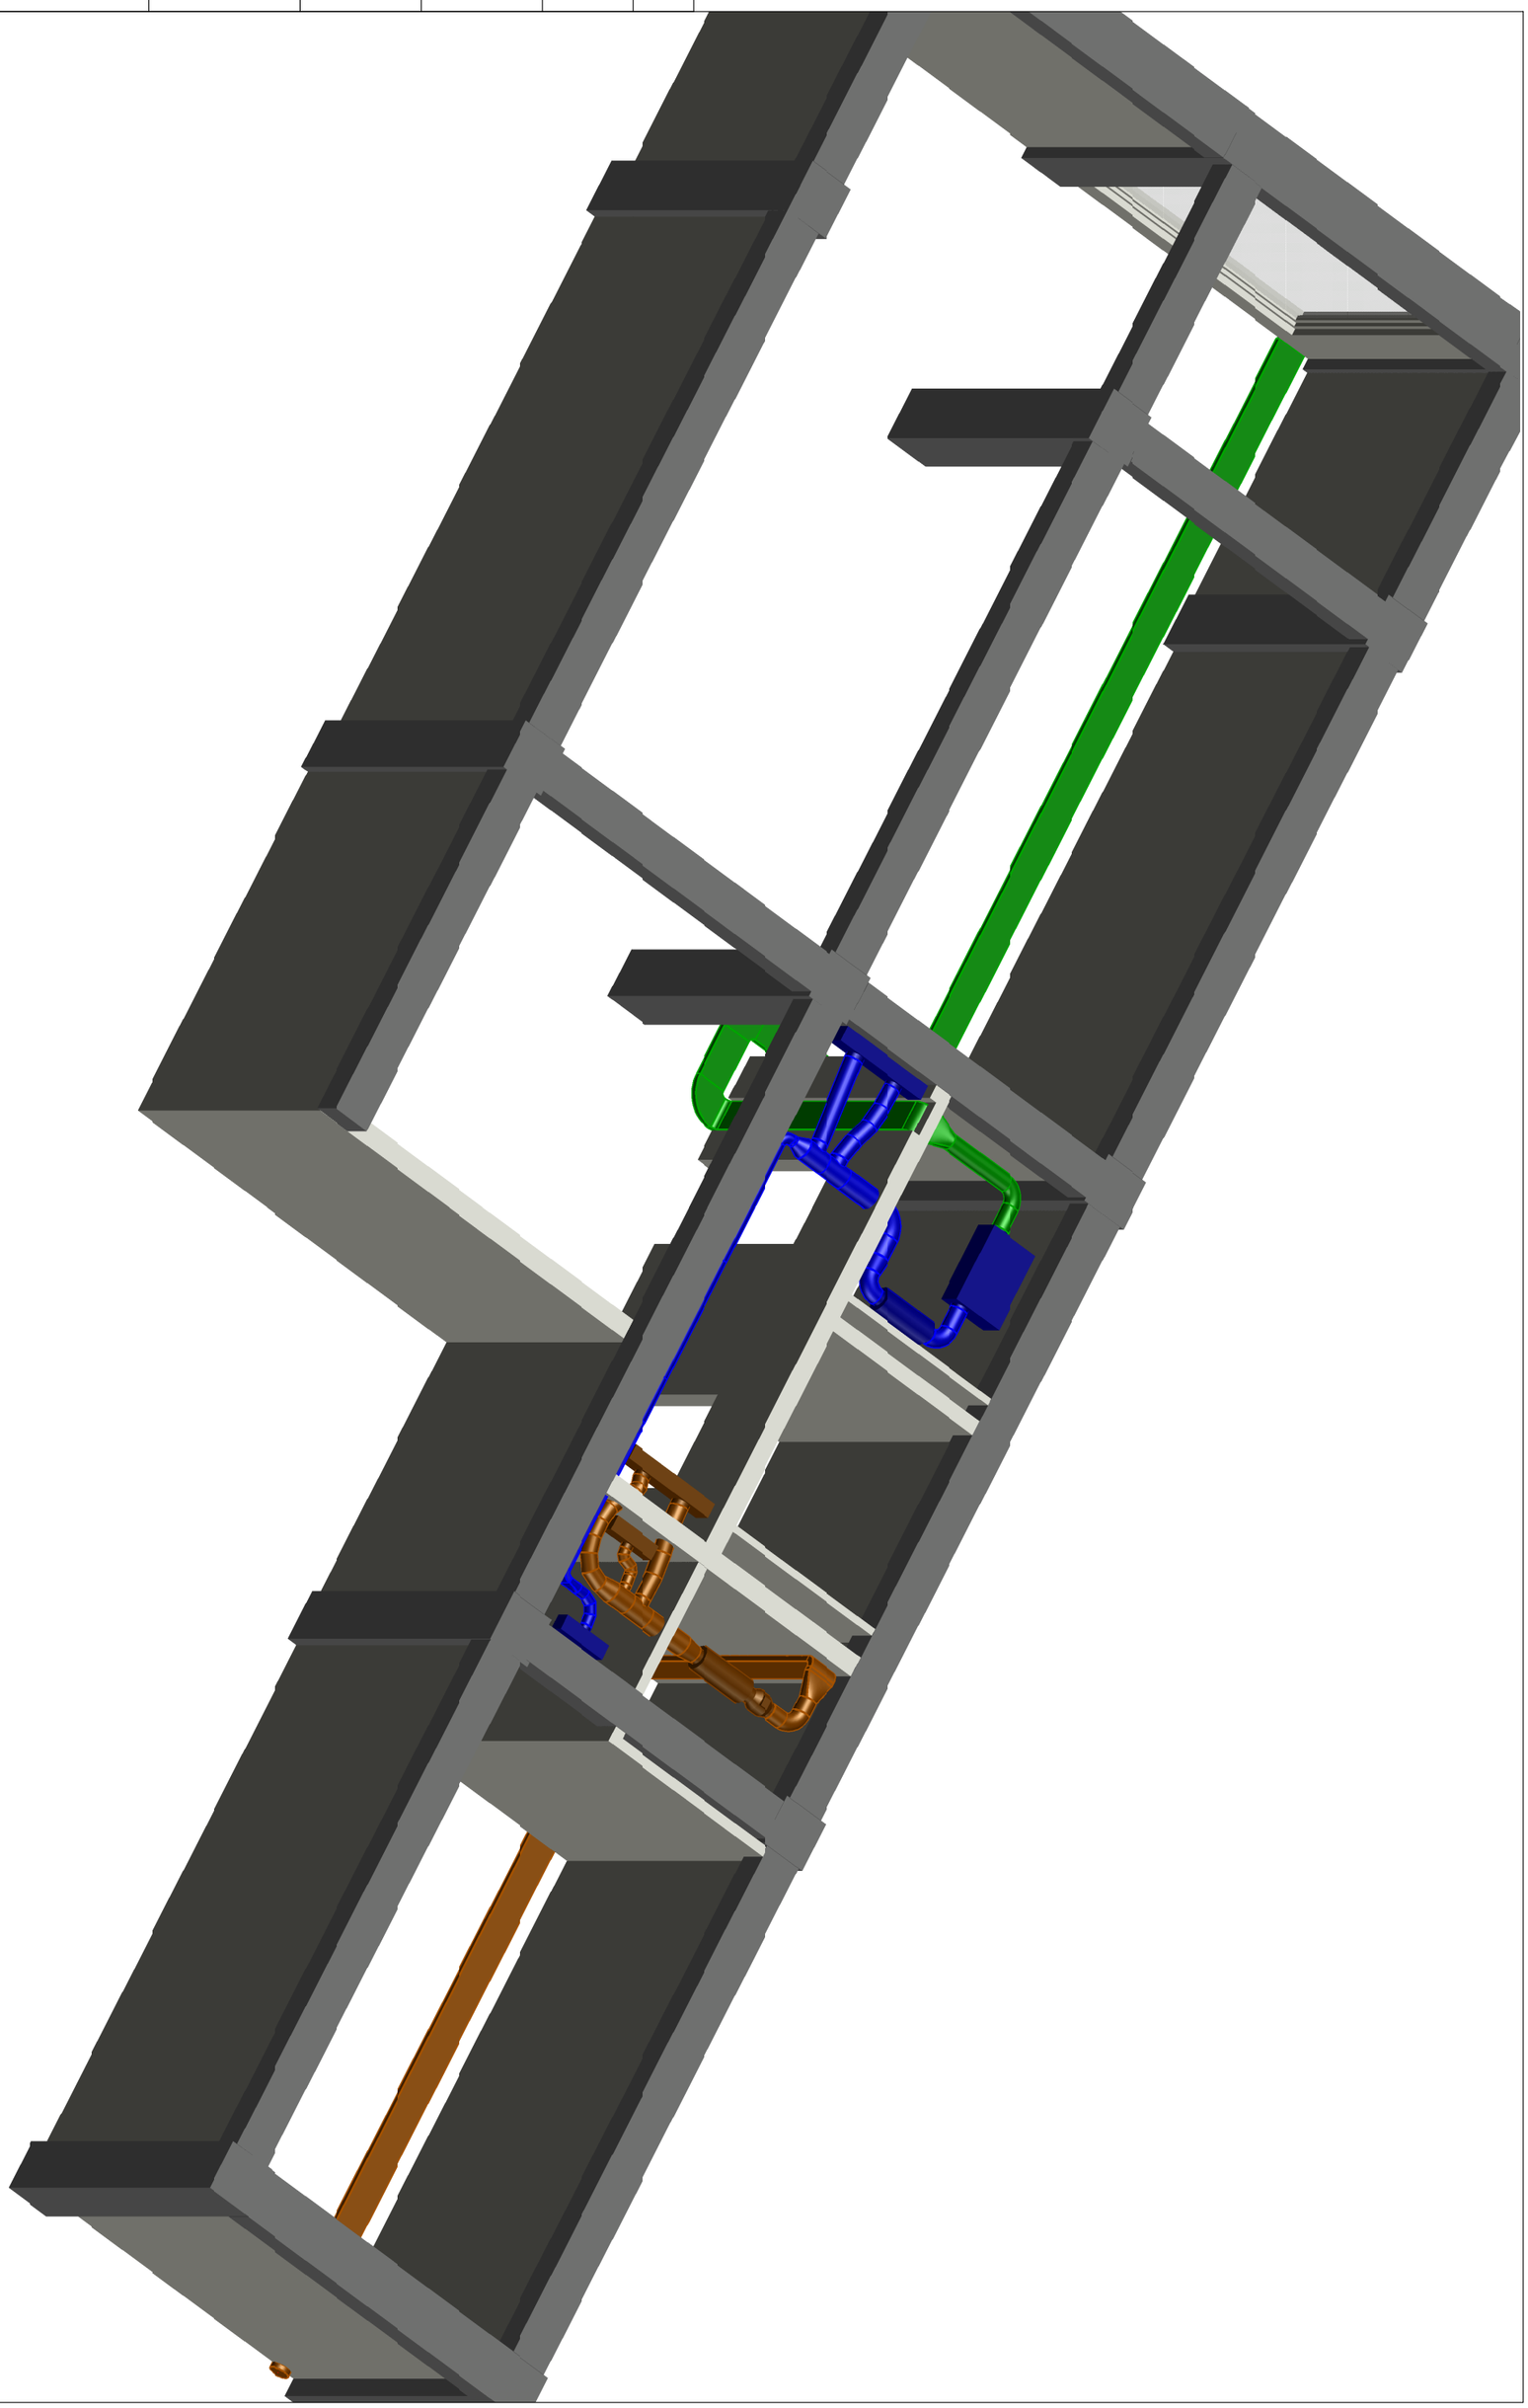

Инв. № подл.	Подпись и дата	Взам. инв. №
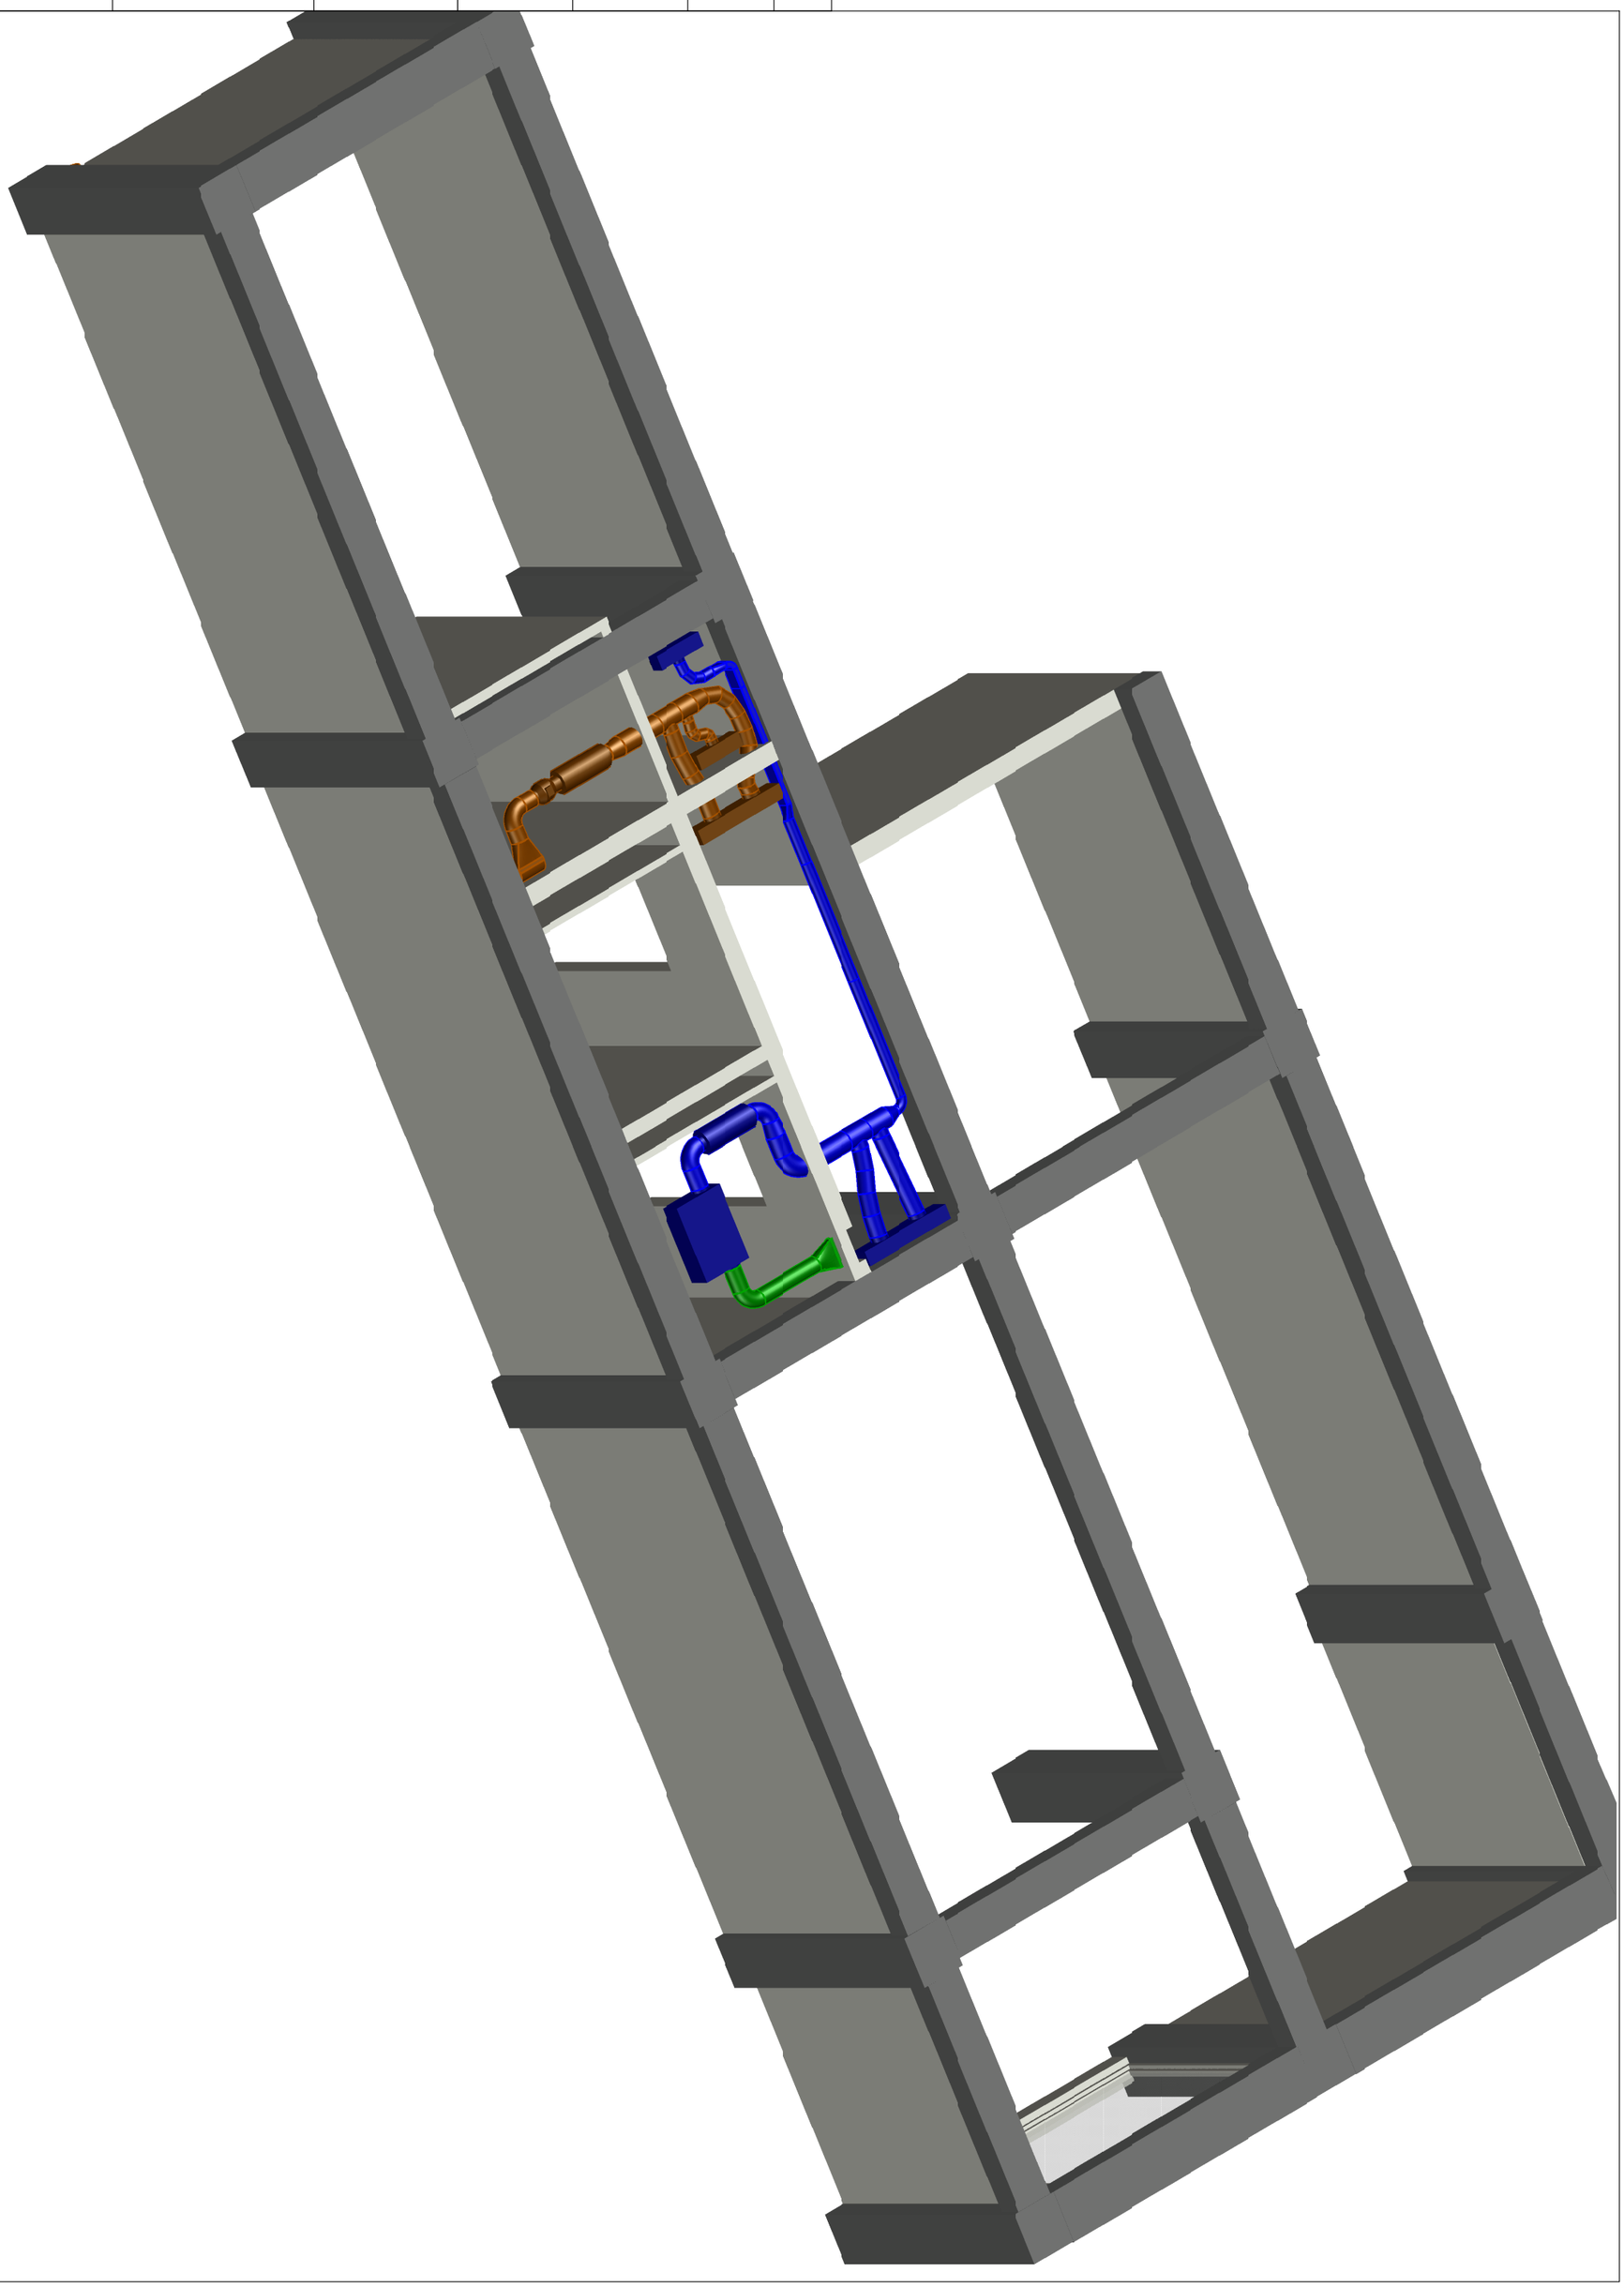
Согласовано