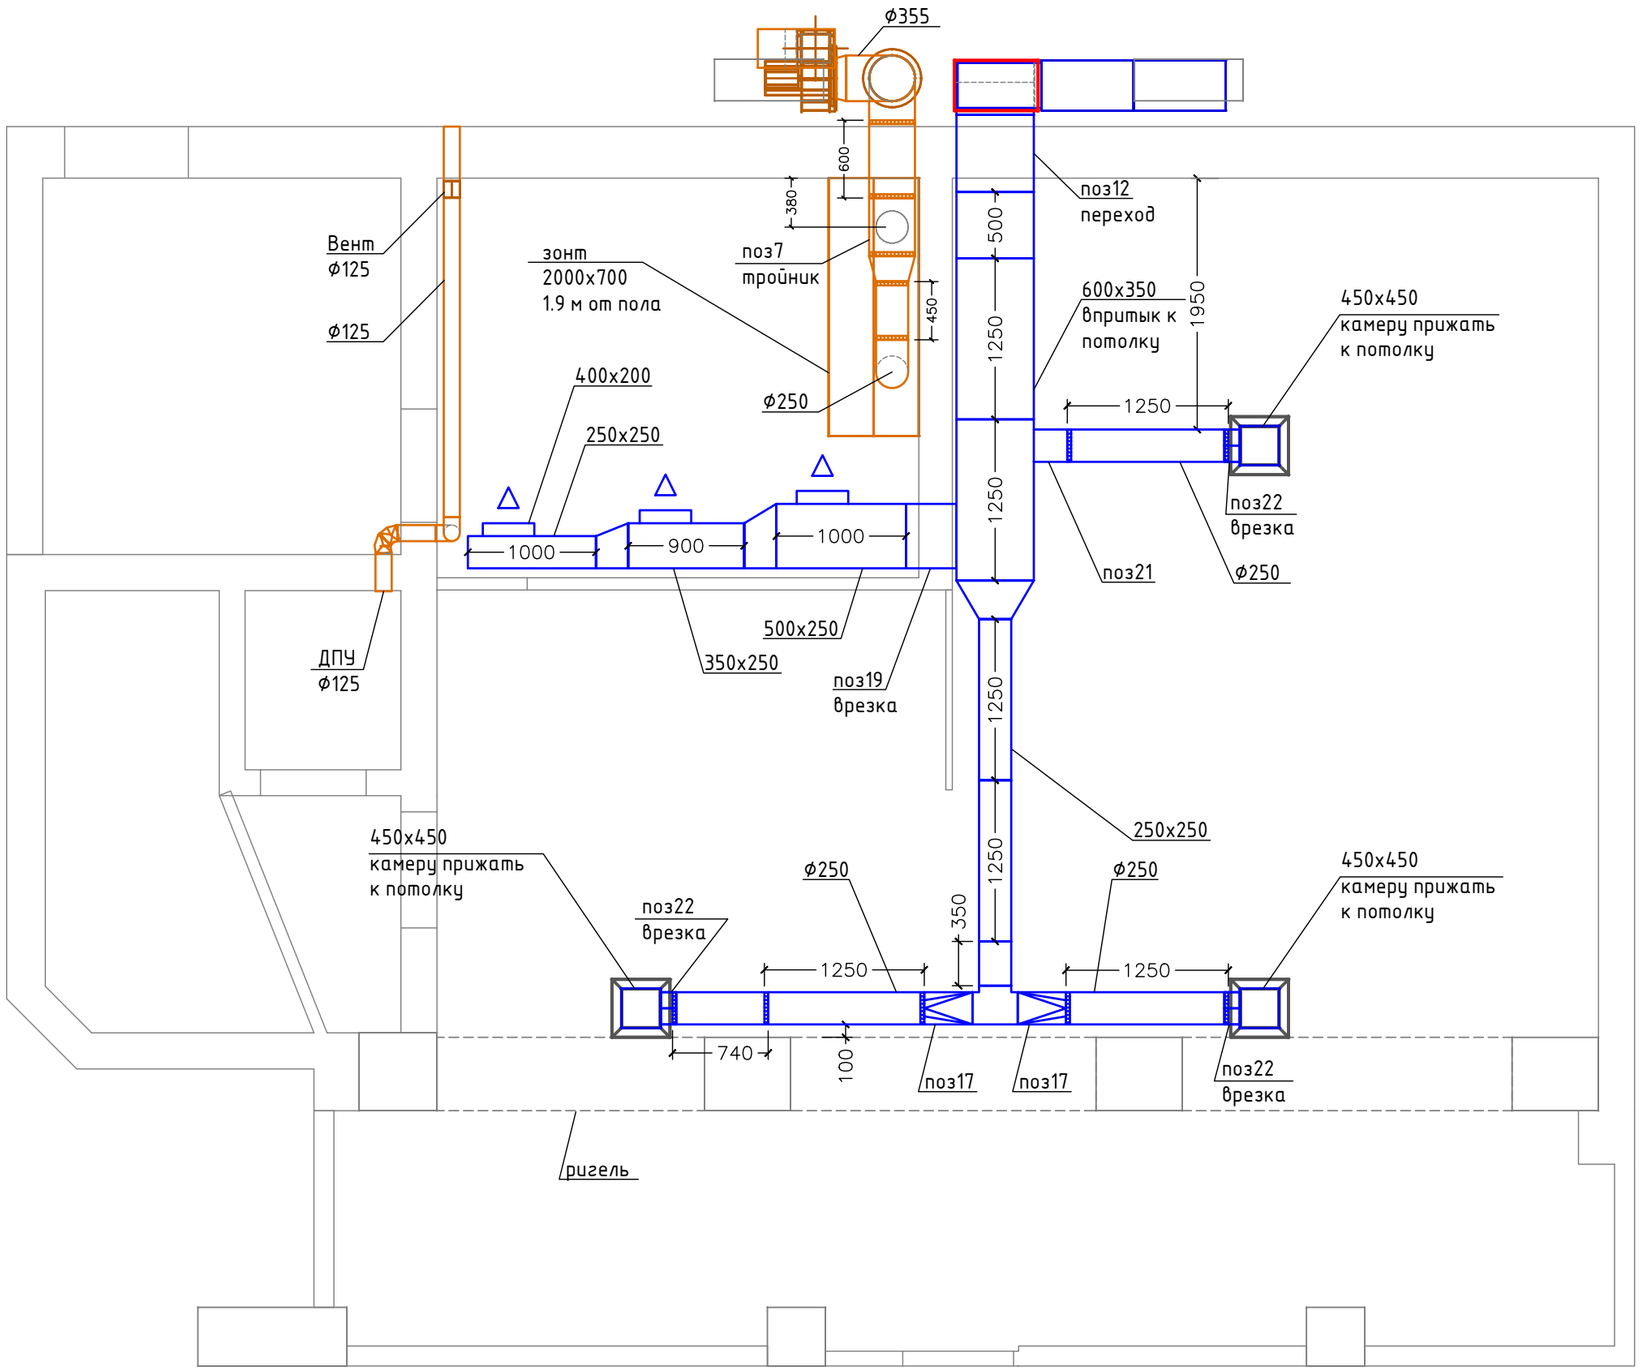

Согласовано

Взам. инв. №

Подпись и дата

Инв. № подл.

						ПД.05.2024-ОВ-ГР-МХ
						Разработка проектной документации по вентиляции.
Изм.	Кол. уч.	Лист	№ док.	Подп.	Дата	
Разработал	Гаджимирзоев					ГИРО
Проверил						
ГИП						План системы вентиляции
Н.контроль						

Стадия	Лист	Листов
П	1	

"MakeHOUSE"

Копировал

Формат А3

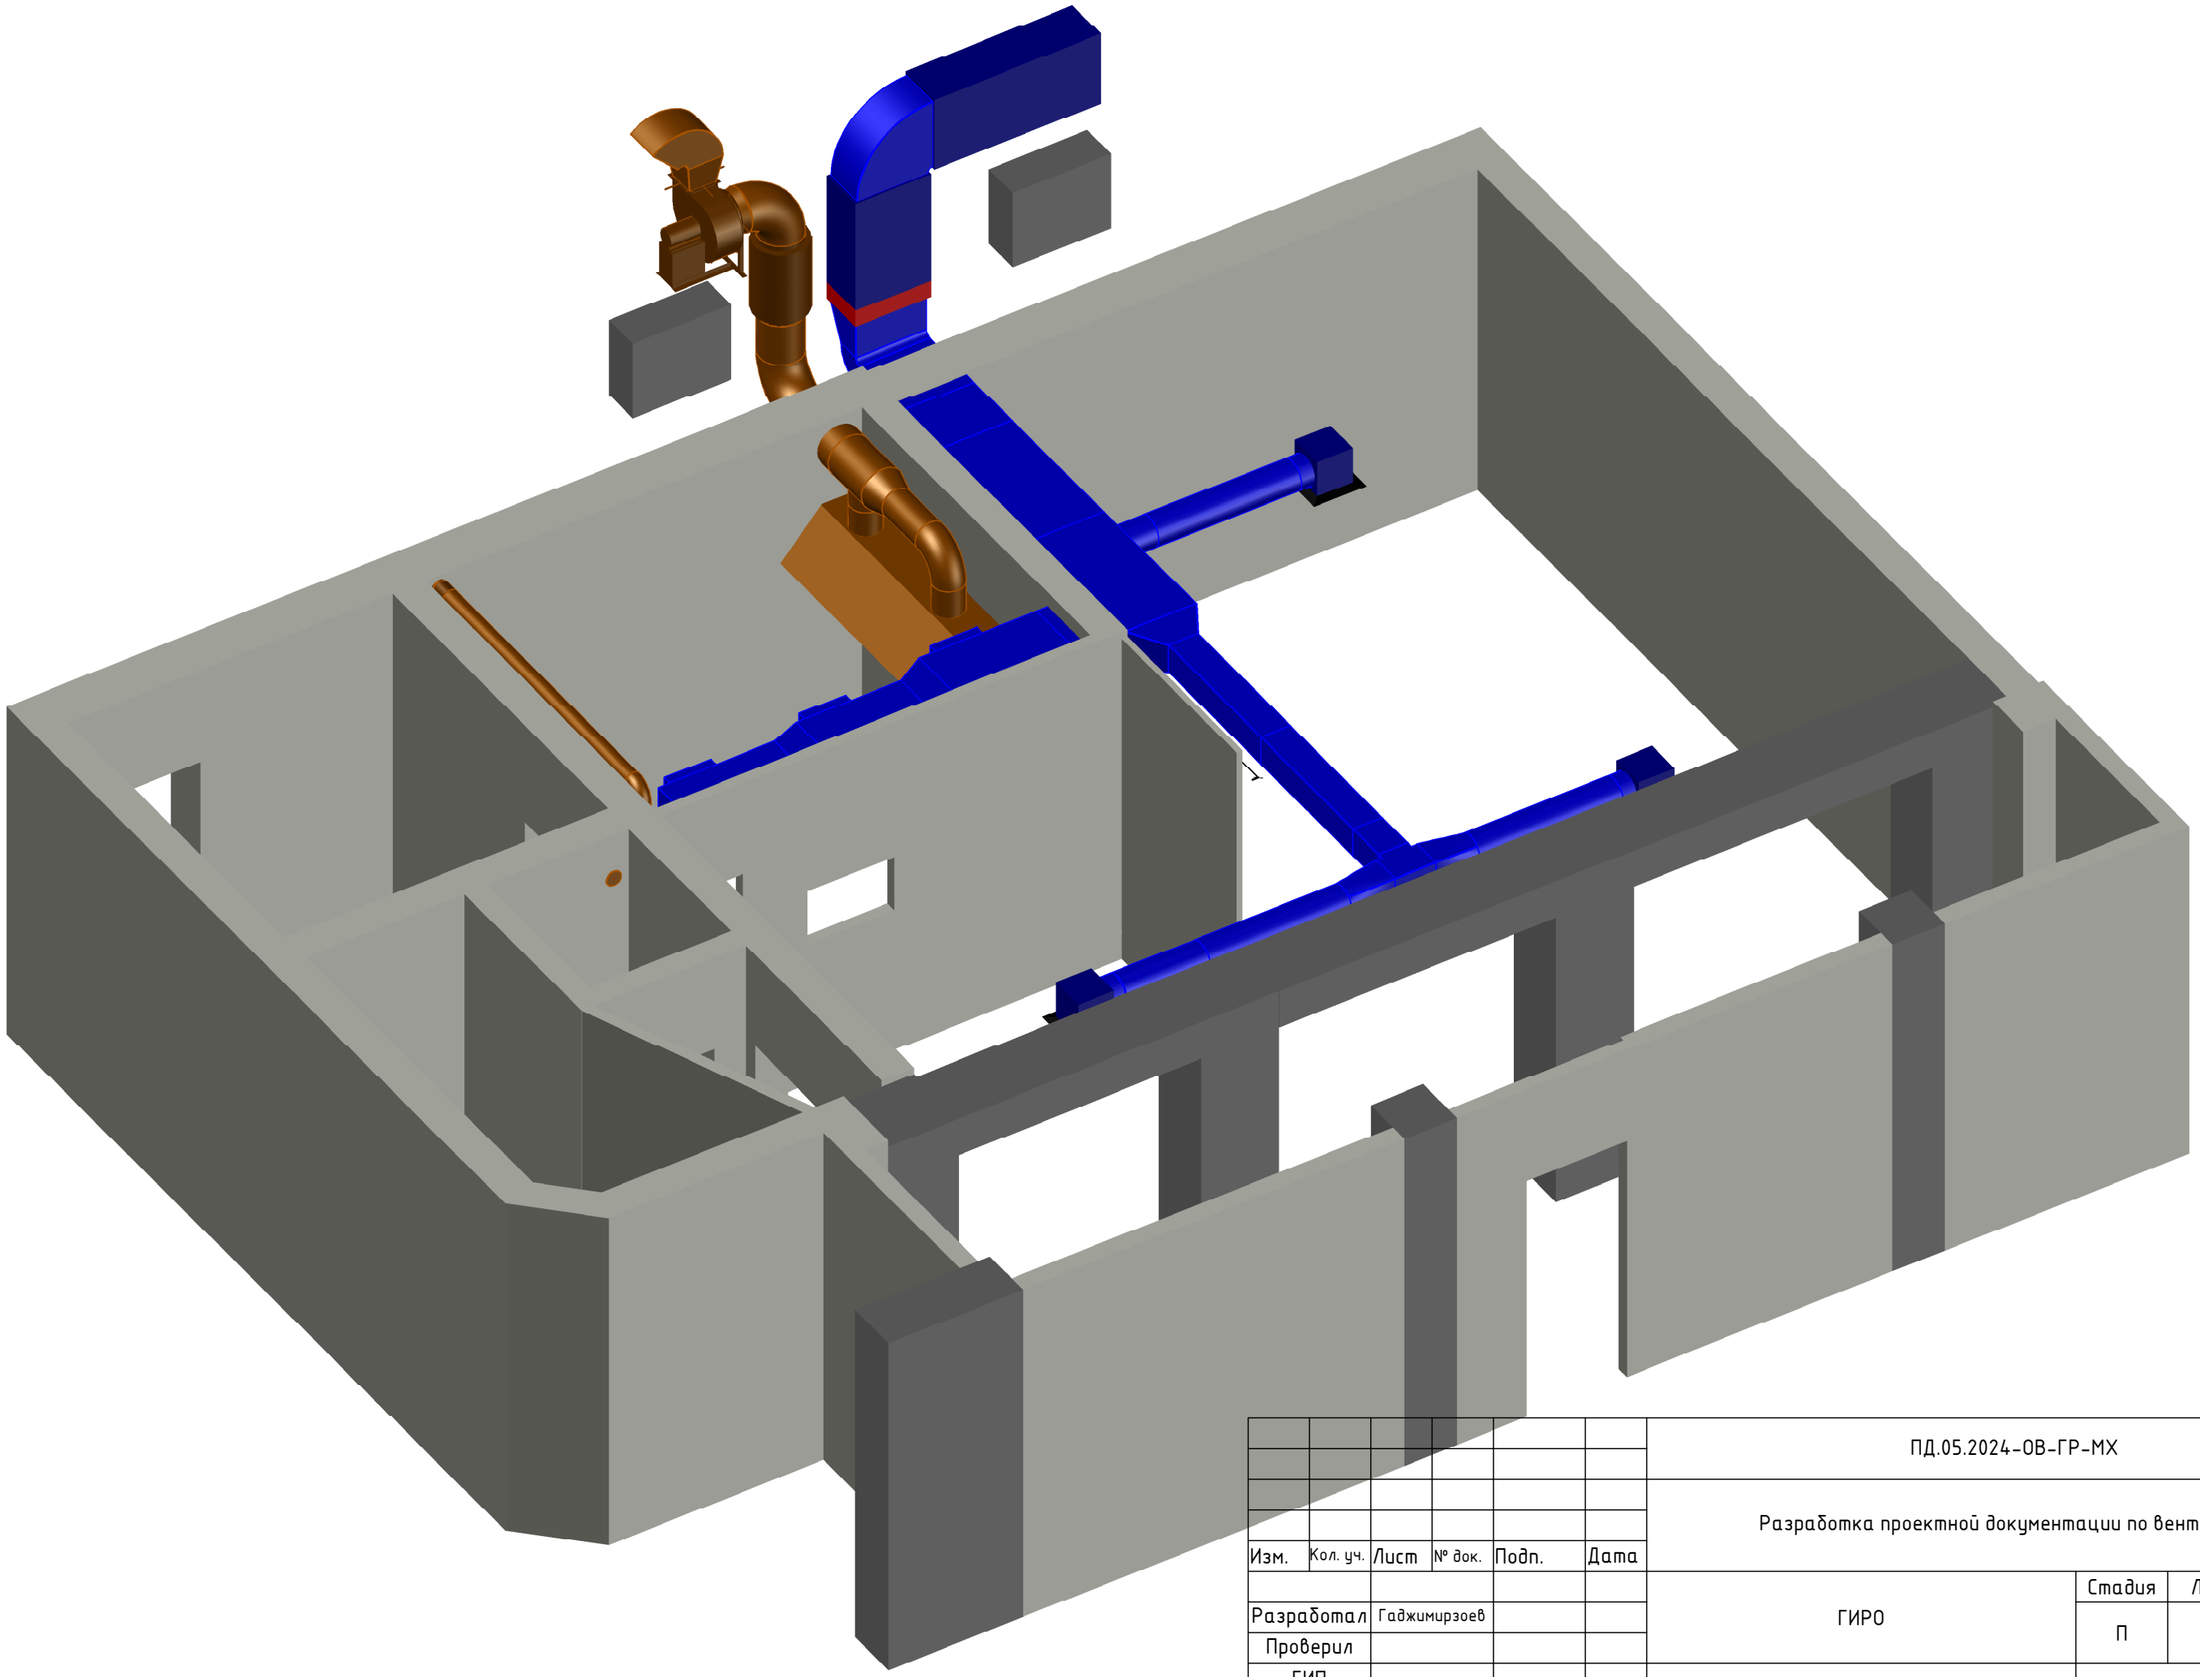

Согласовано

Взам. инв. №

Подпись и дата

Инв. № подл.

						ПД.05.2024-ОВ-ГР-МХ
						Разработка проектной документации по вентиляции.
Изм.	Кол. уч.	Лист	№ док.	Подп.	Дата	
Разработал	Гаджимирзоев					ГИРО
Проверил						
ГИП						3D вид 1
Н.контроль						

Стадия	Лист	Листов
П	2	

"MakeHOUSE"

Копировал

Формат А3

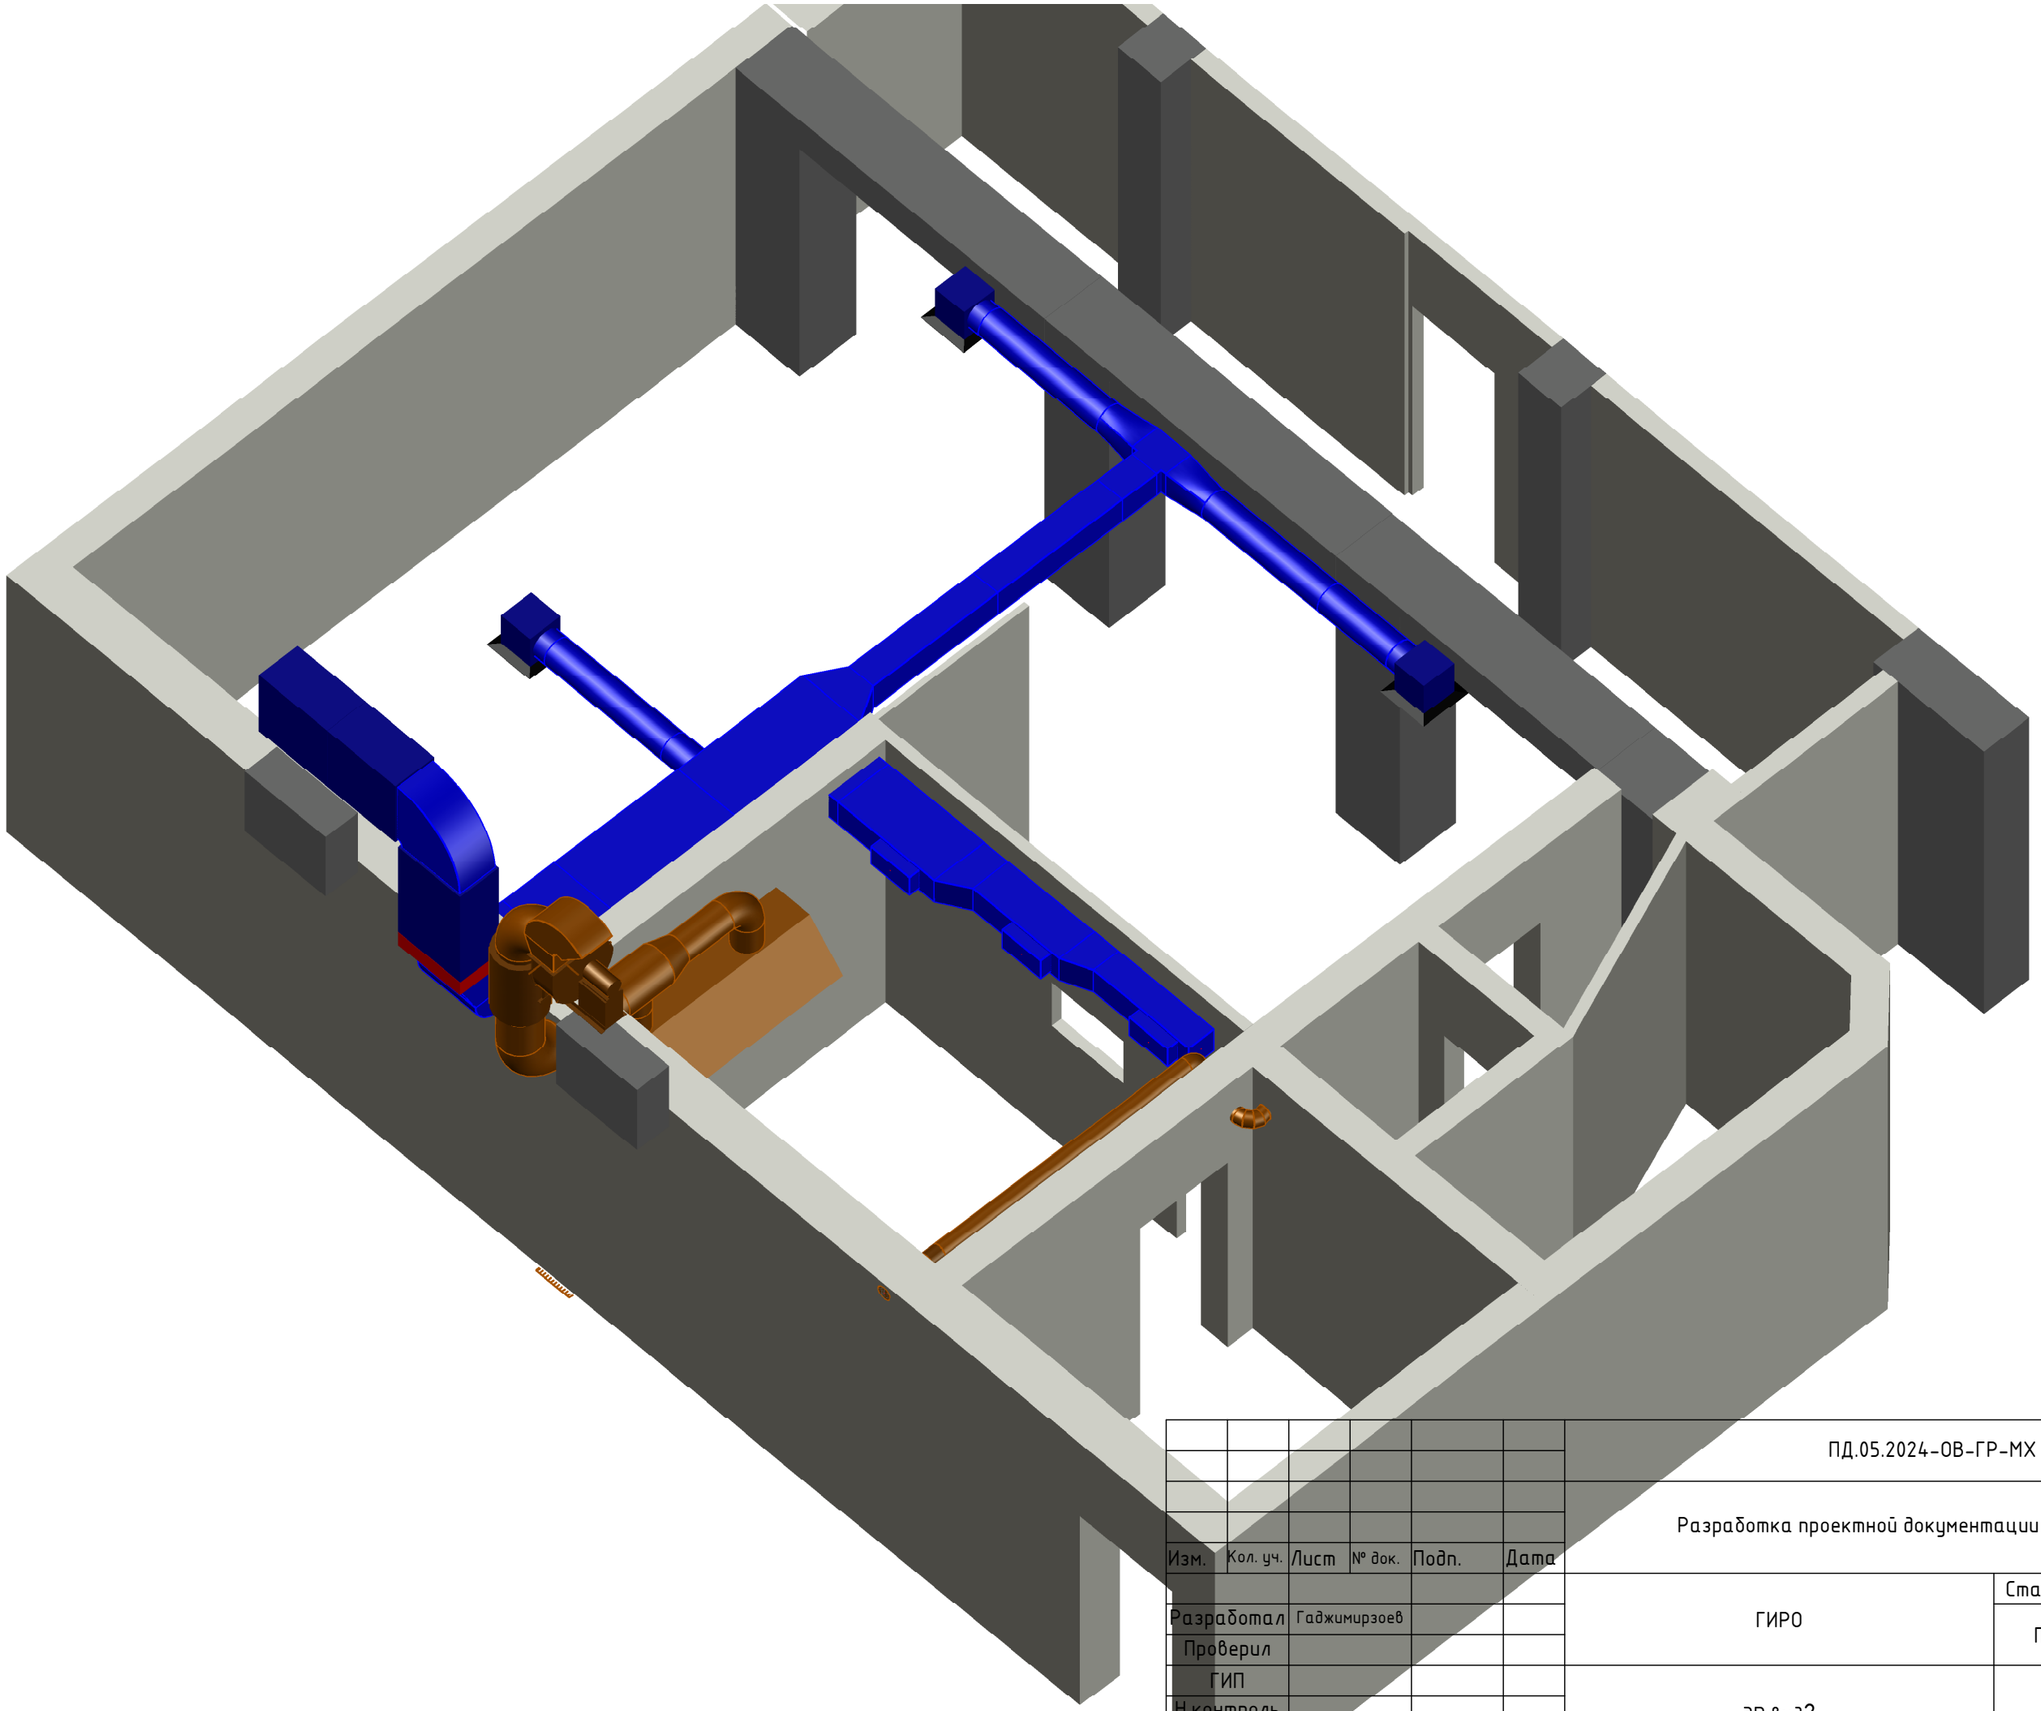

						ПД.05.2024-ОВ-ГР-МХ		
Изм.	Кол. уч.	Лист	№ док.	Подп.	Дата	Разработка проектной документации по вентиляции.		
Разработал	Гаджимирзоев					ГИРО	Стадия	Лист	Листов
Проверил							П	2	
ГИП						3D вид2	"MakeHOUSE"		
Н.контроль									

Согласовано

Взам. инв. №

Подпись и дата

Инв. № подл.

Копировал

Формат А3

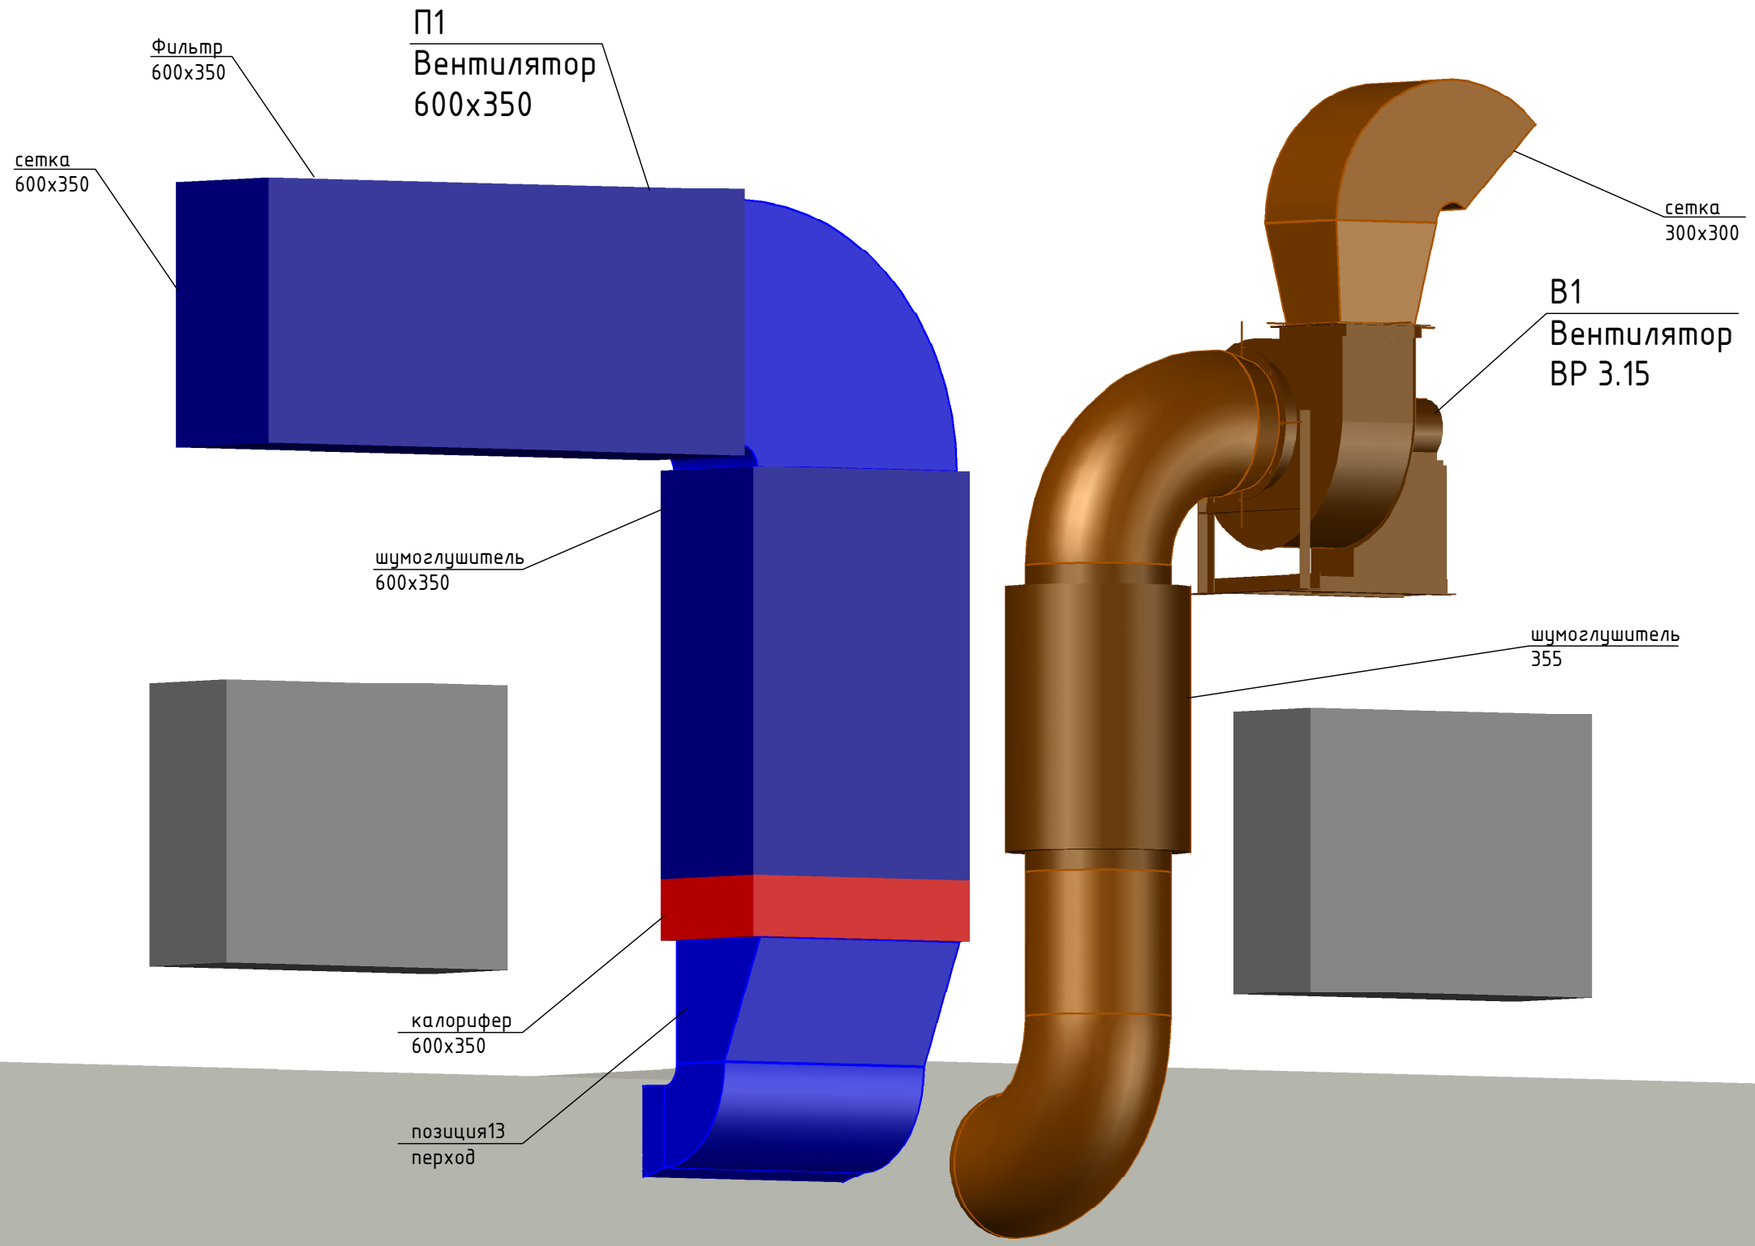

Согласовано

Взам. инв. №

Подпись и дата

Инв. № подл.

						ПД.05.2024-ОВ-ГР-МХ
						Разработка проектной документации по вентиляции.
Изм.	Кол. уч.	Лист	№ док.	Подп.	Дата	
Разработал		Гаджимирзоев				ГИРО
Проверил						
ГИП						3D вид 3
Н.контроль						

Стадия	Лист	Листов
П	4	

"MakeHOUSE"

Копировал

Формат А3