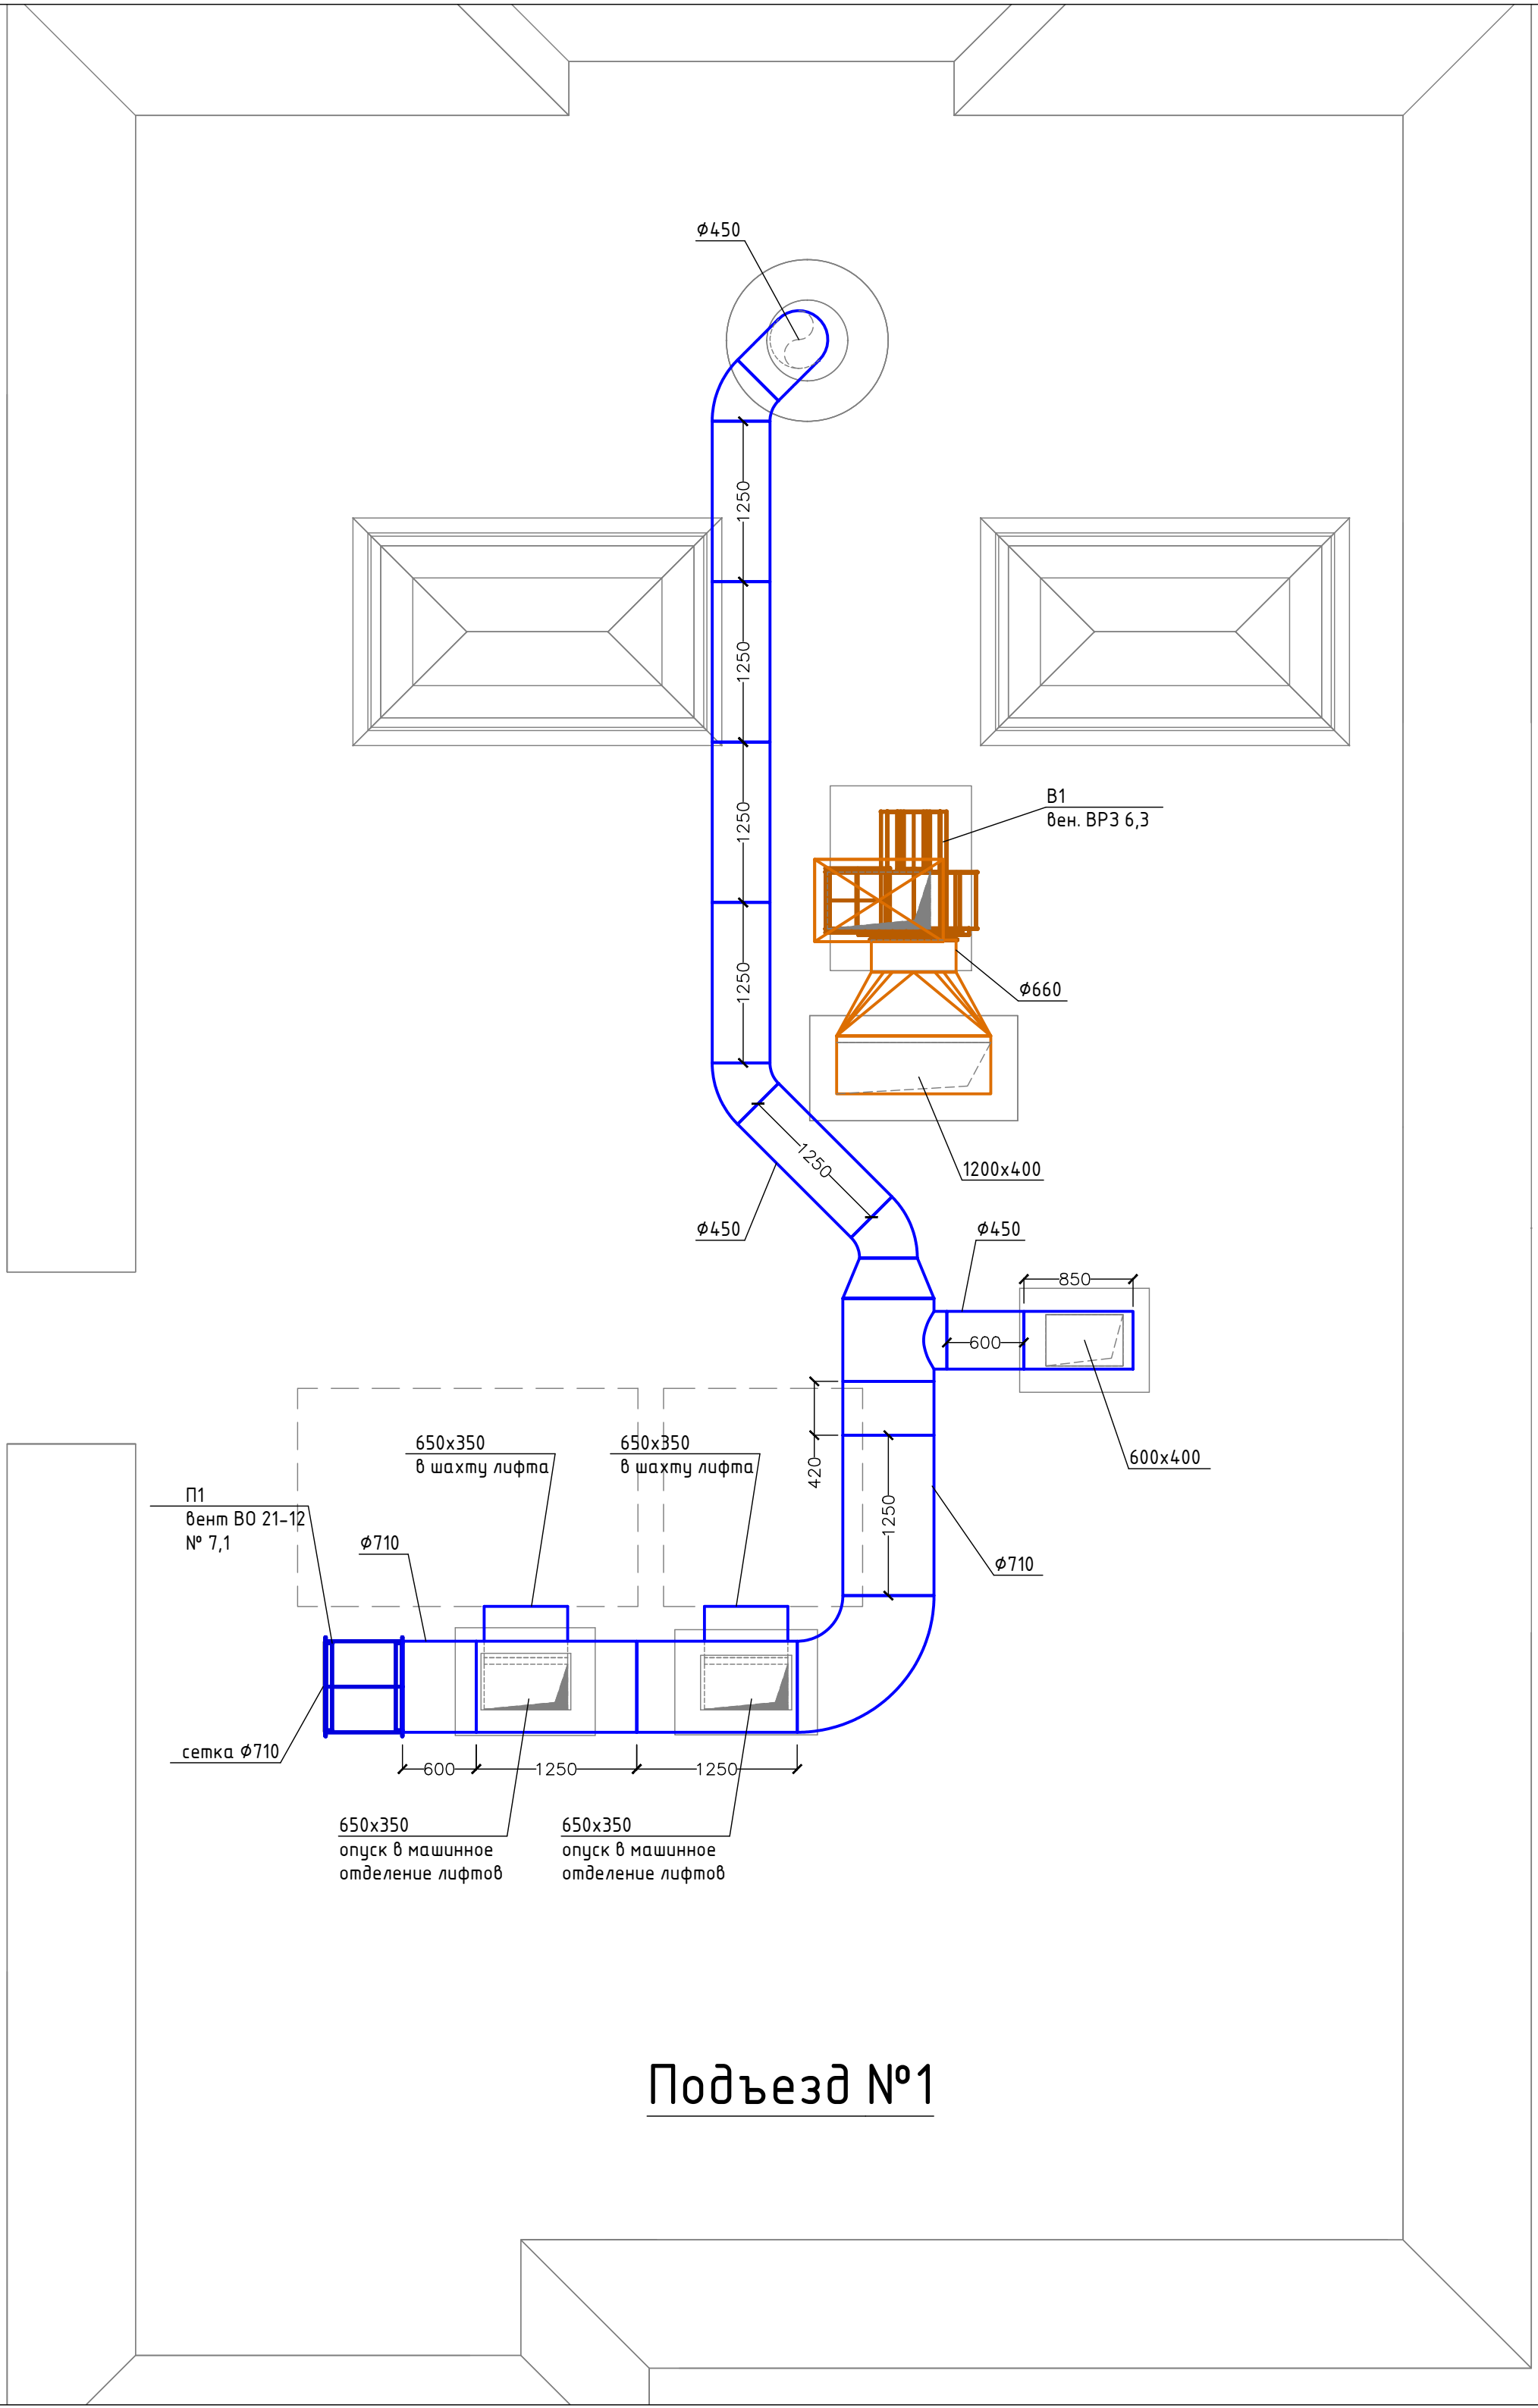
ϕ450
1250
1250
1250
1250
1250
В1
вен. ВР3 6,3
ϕ660
1200x400
ϕ450
ϕ450
850
600
600x400
650x350
в шахту лифта
650x350
в шахту лифта
420
1250
ϕ710
П1
вент ВО 21-12
№ 7,1
ϕ710
сетка ϕ710
600
1250
1250
650x350
опуск в машинное
отделение лифтов
650x350
опуск в машинное
отделение лифтов

Подъезд №1

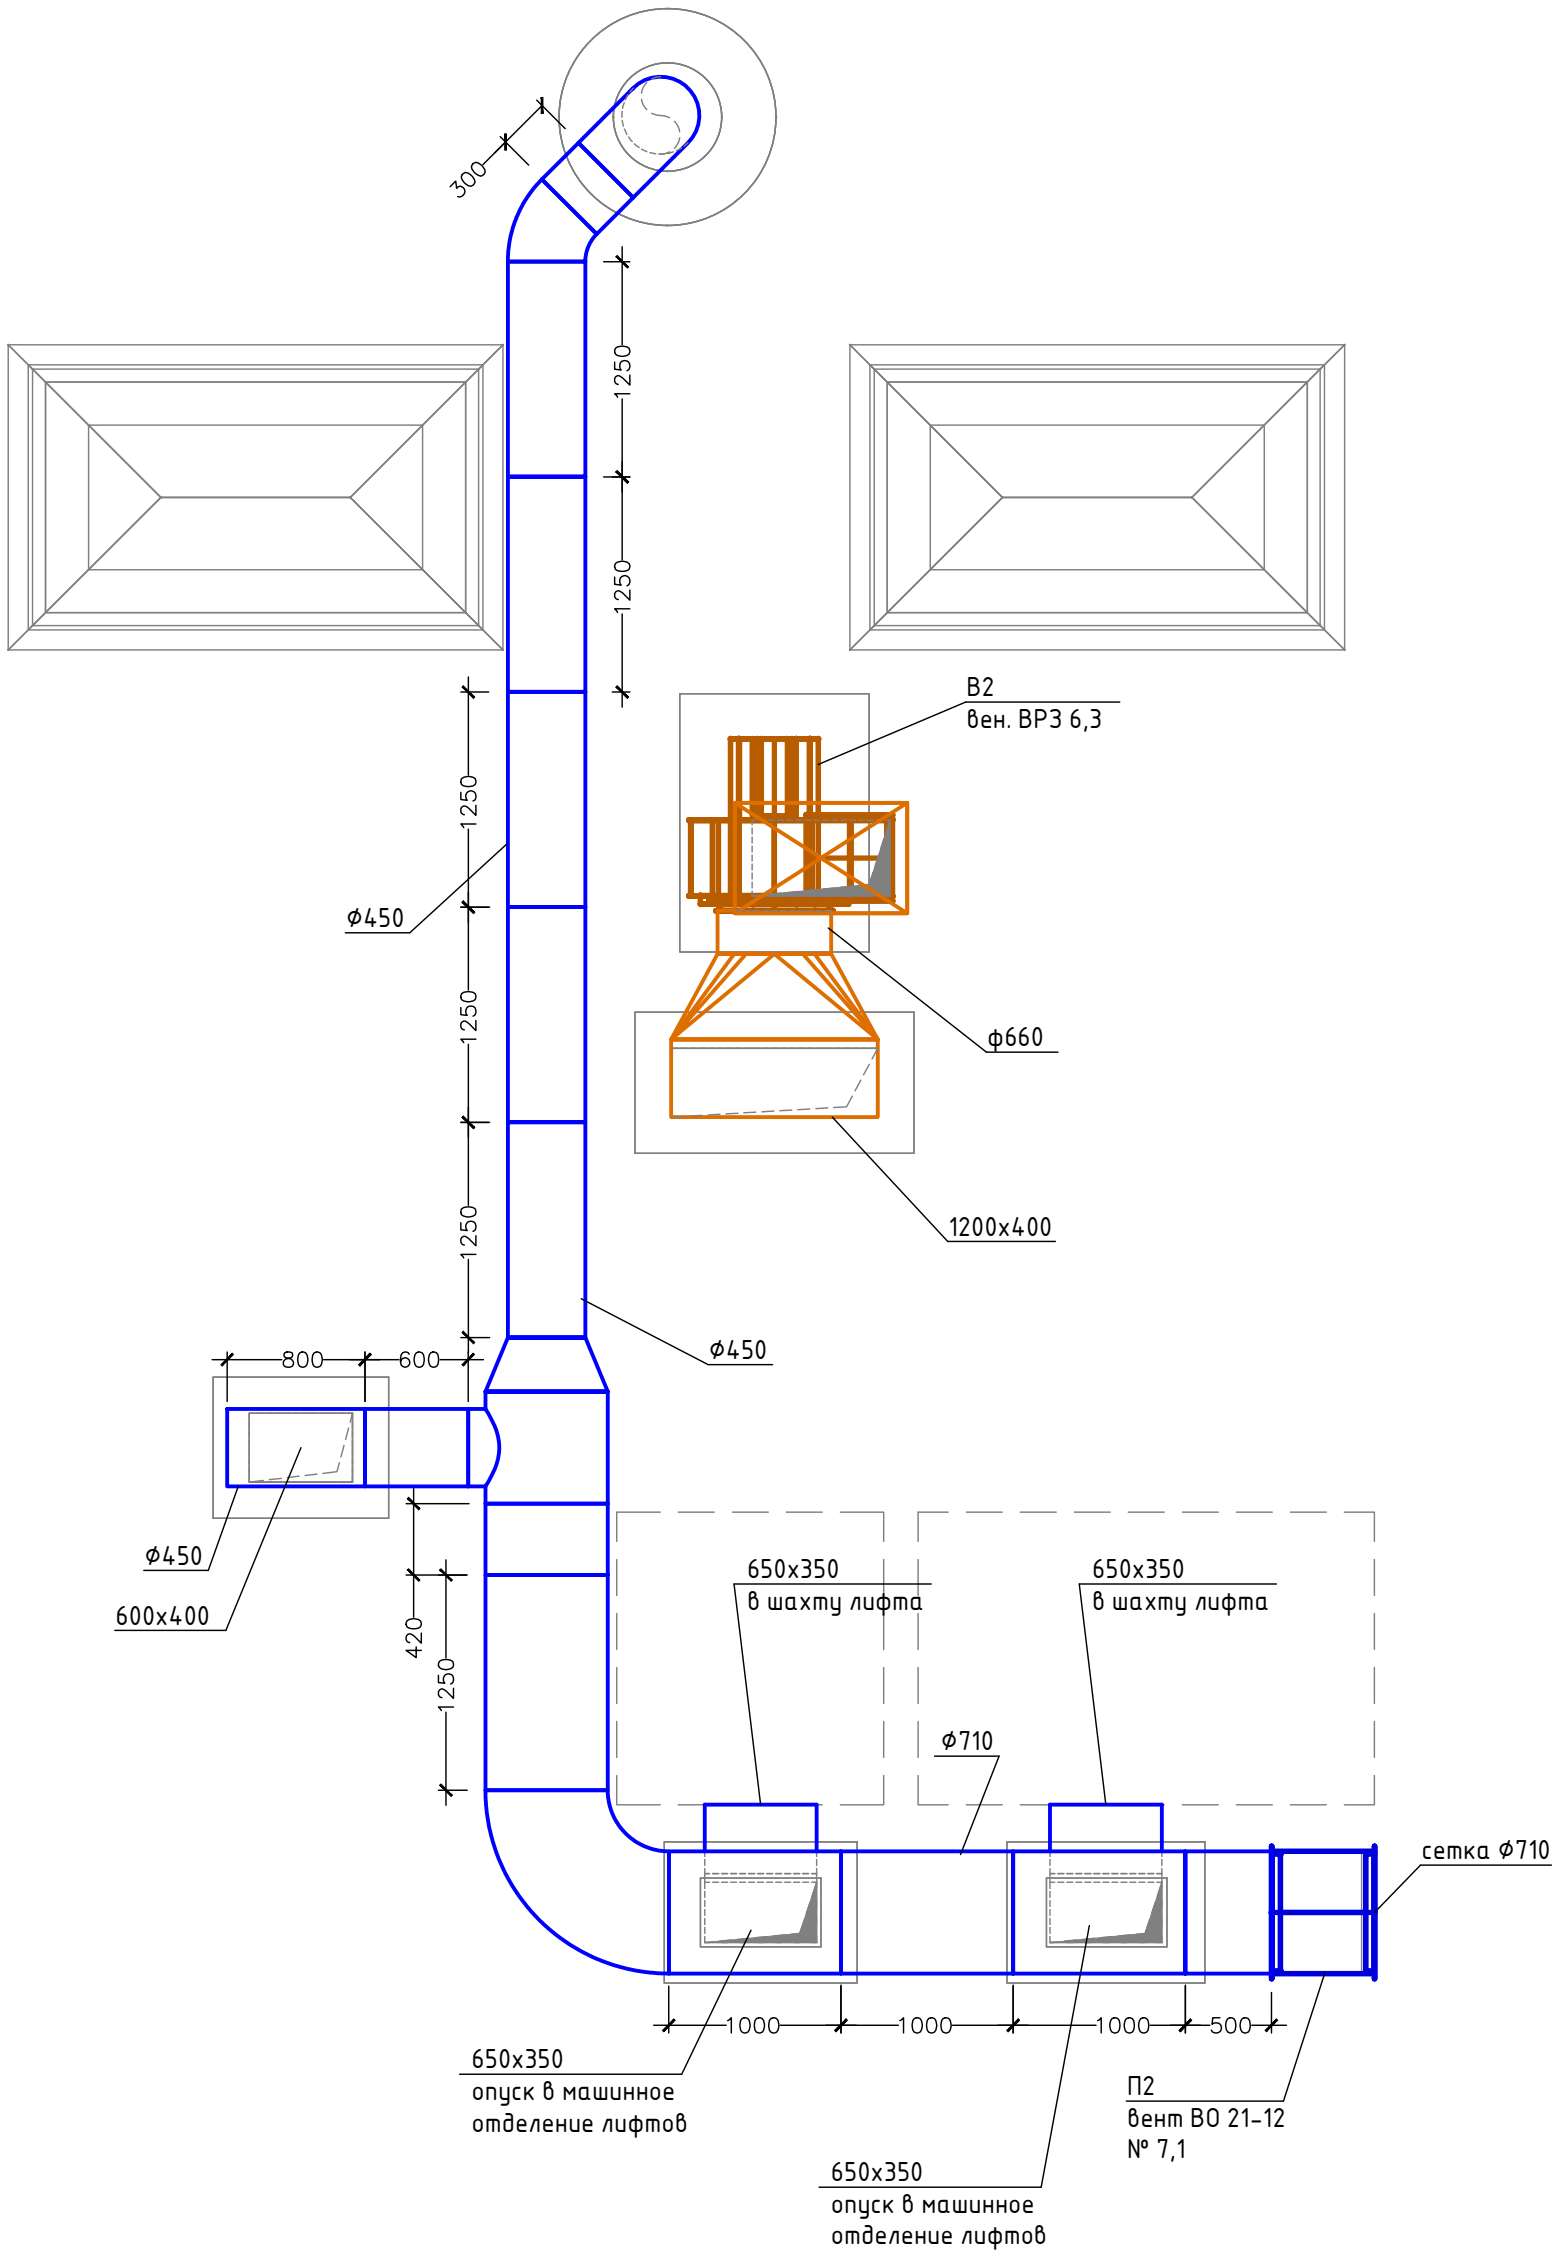
300
1250
1250
1250
1250
1250
1250
В2
вен. ВР3 6,3
ф450
ф660
1200x400
ф450
800
600
ф450
600x400
420
1250
650x350
в шахту лифта
650x350
в шахту лифта
ф710
сетка ф710
1000
1000
1000
500
650x350
опуск в машинное
отделение лифтов
П2
вент ВО 21-12
№ 7,1
650x350
опуск в машинное
отделение лифтов

Подъезд №2

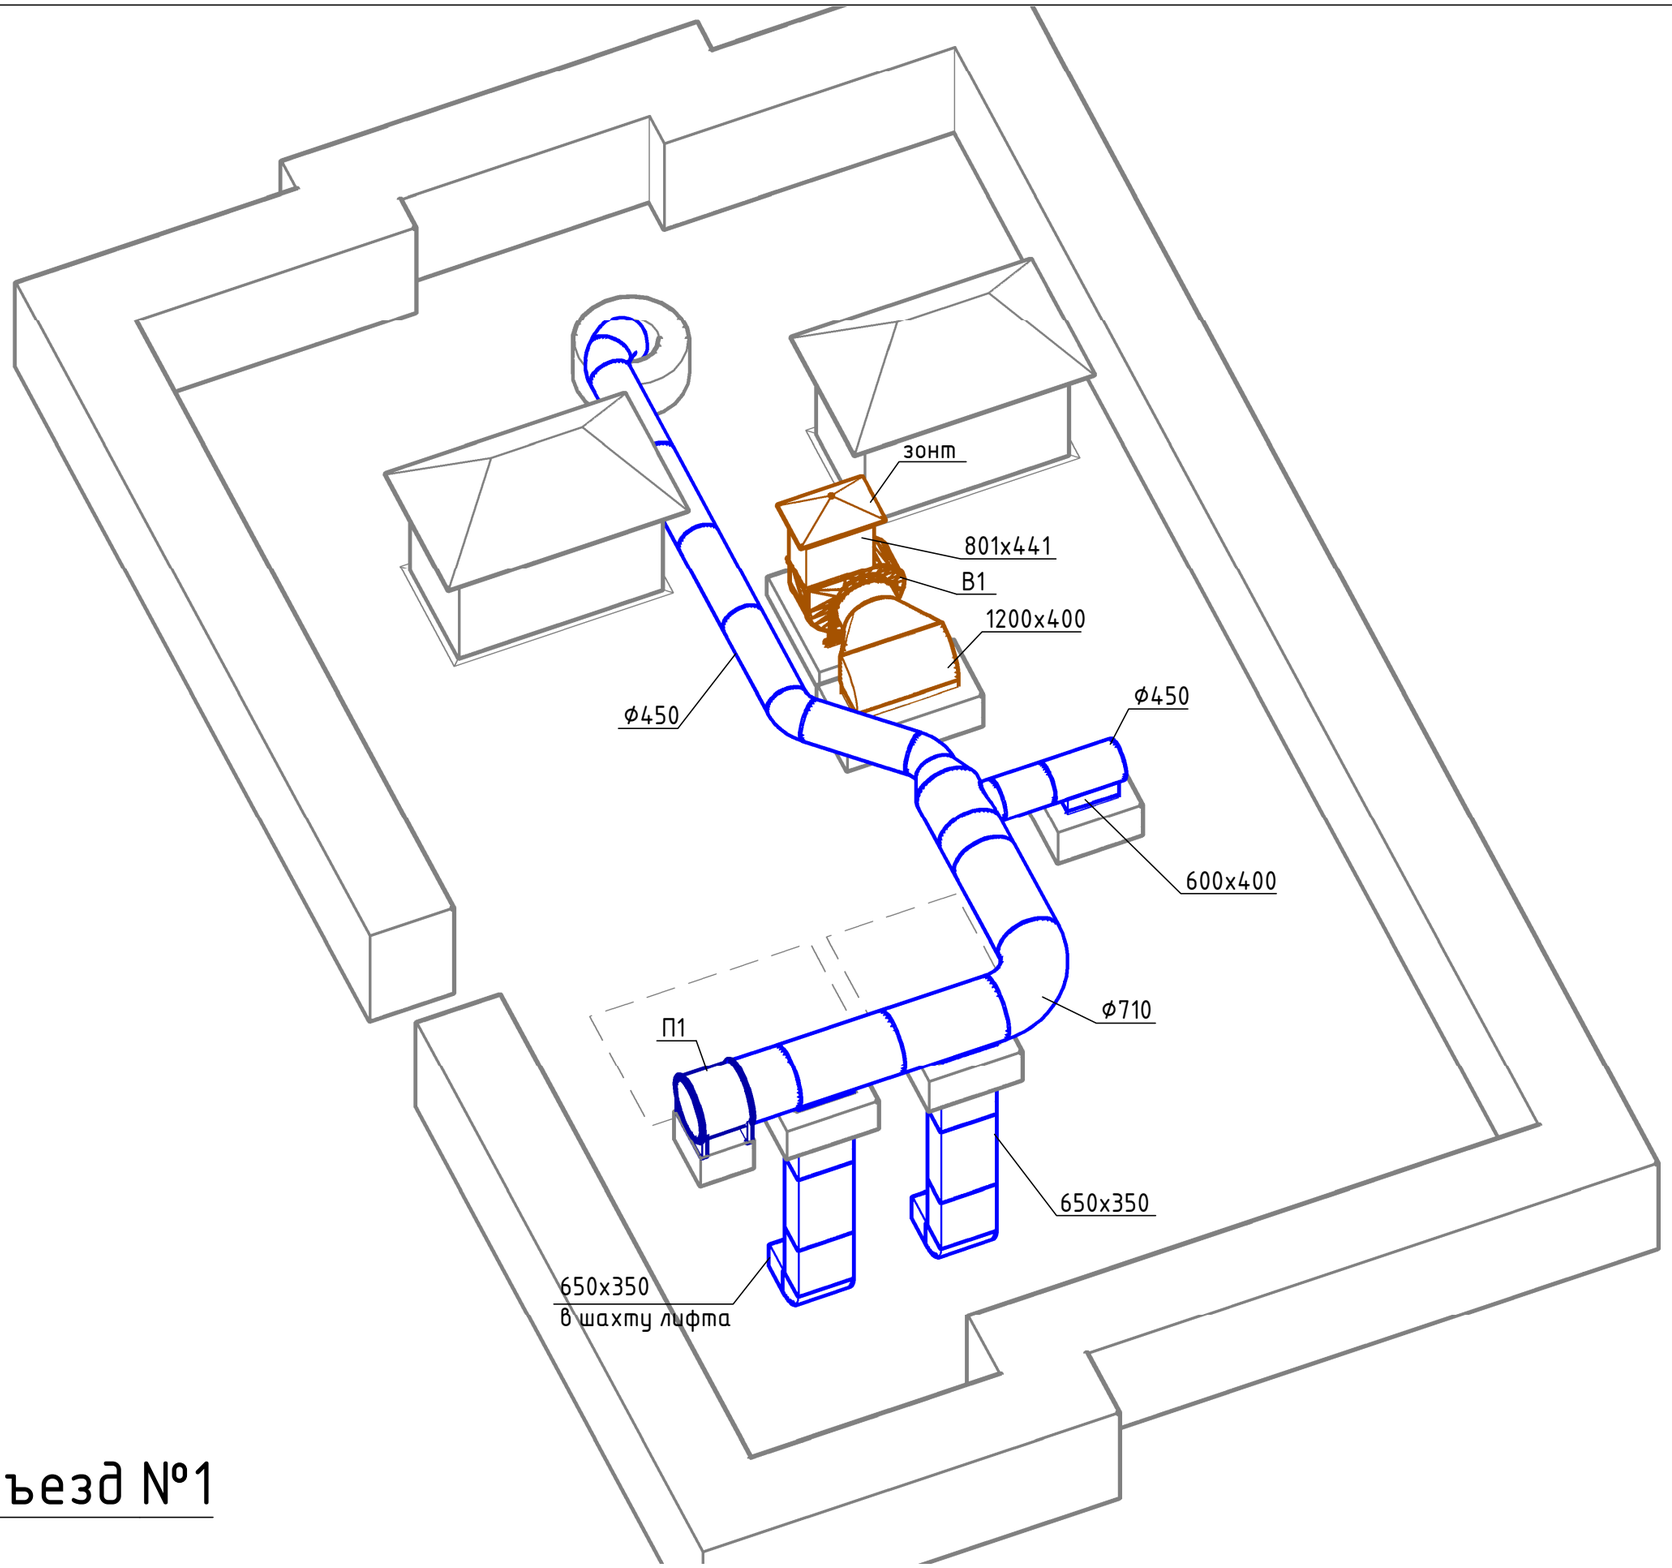

Подъезд №1

Согласовано

Взам. инв. №

Подпись и дата

Инв. № подл.

Копировал

Формат А3

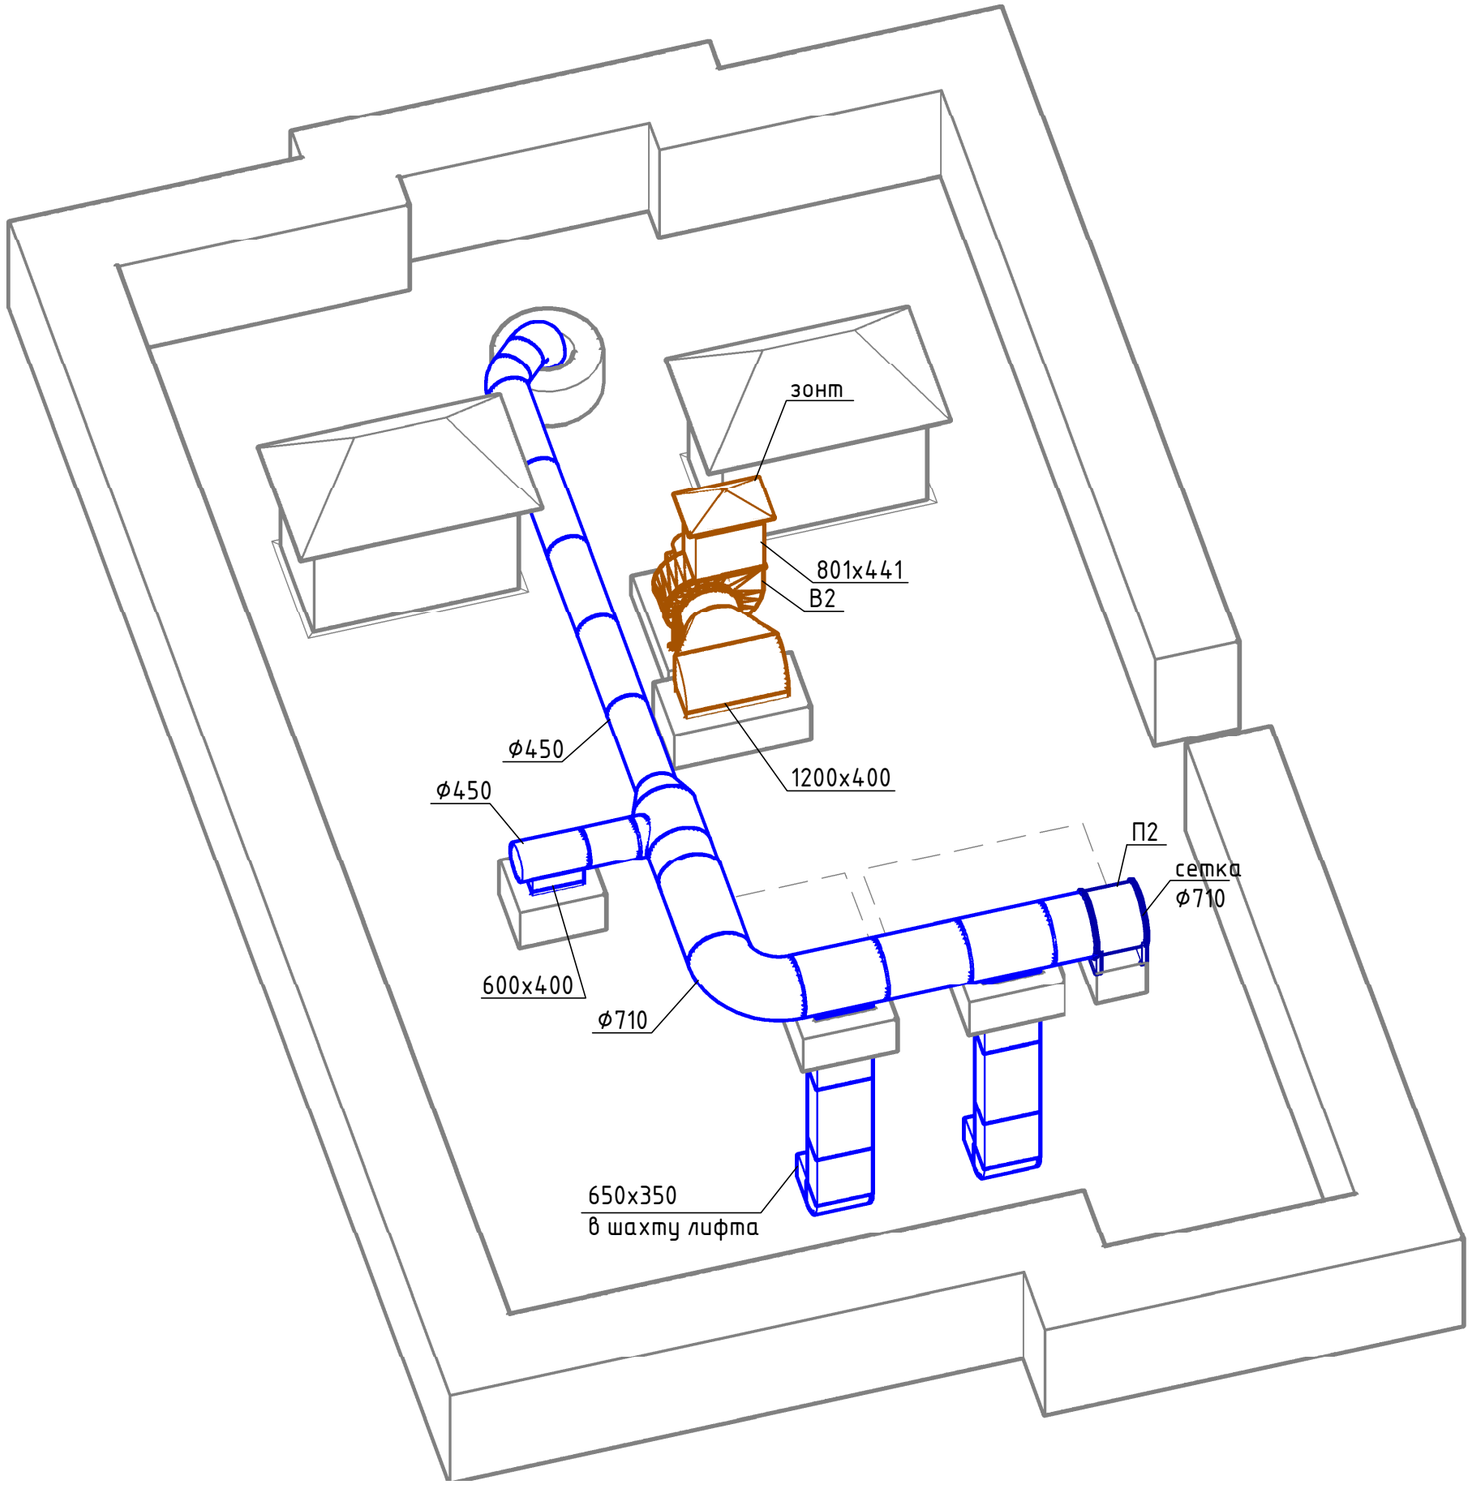

Подъезд №2

Согласовано

Взам. инв. №

Подпись и дата

Инв. № подл.

Копировал

Формат А3