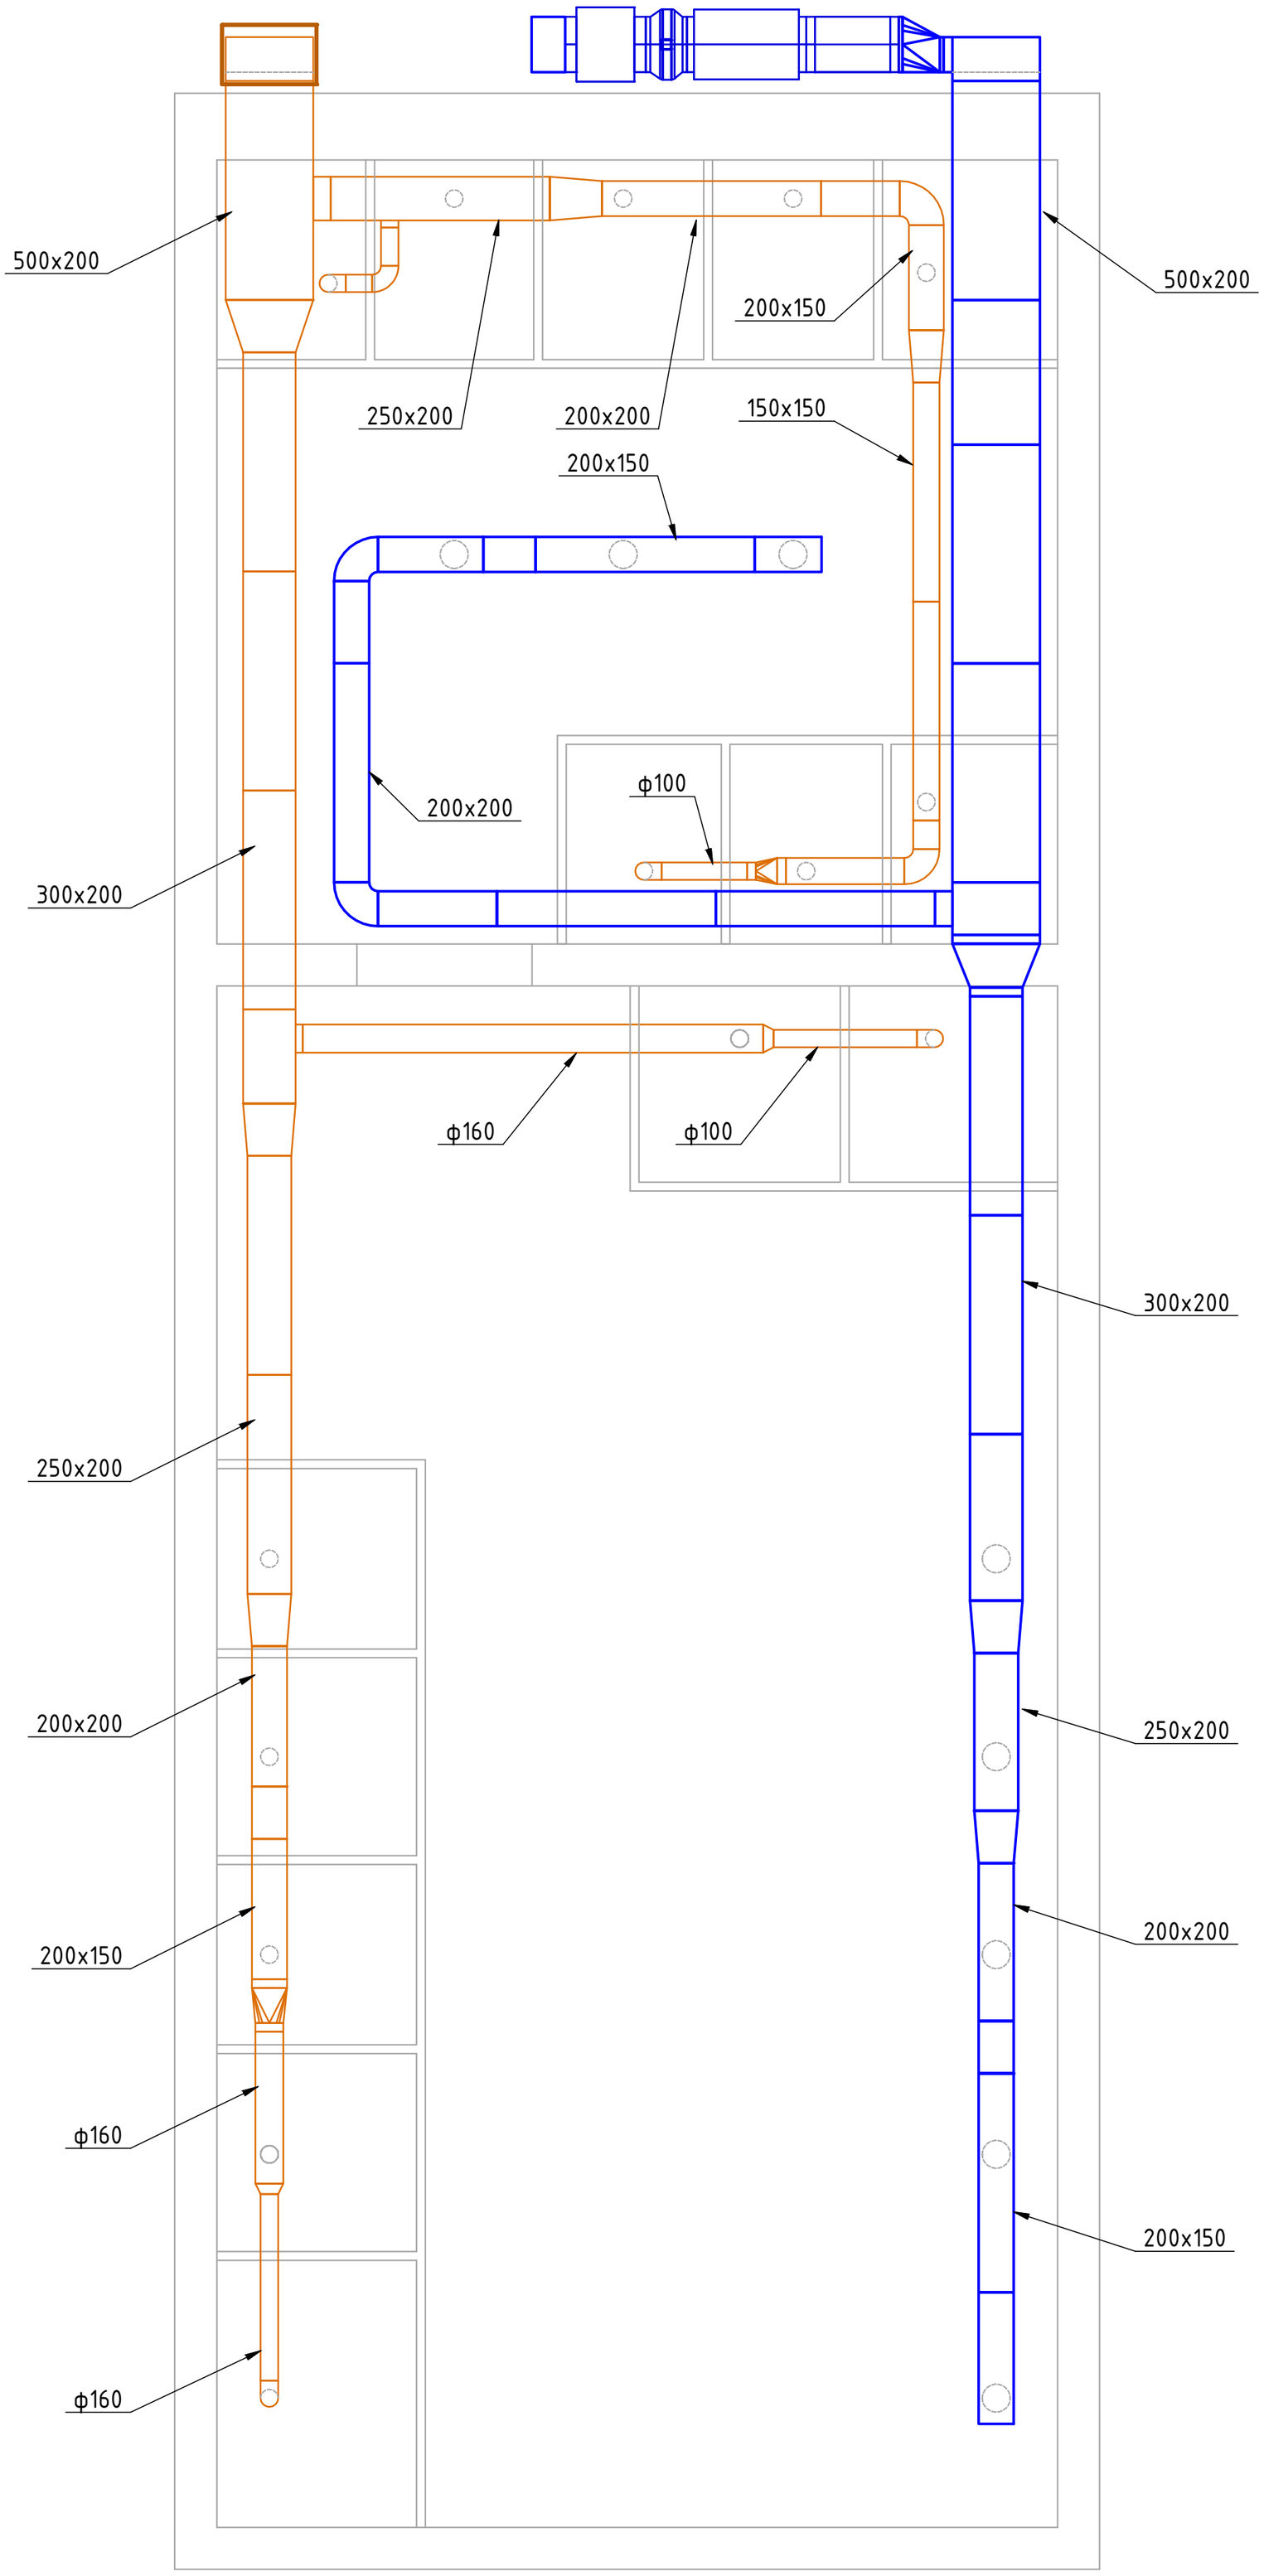

1. ПЛАН СИСТЕМ ВЕНТИЛЯЦИИ

Согласовано

Взам. инв. №

Подпись и дата

Инв. № подл.

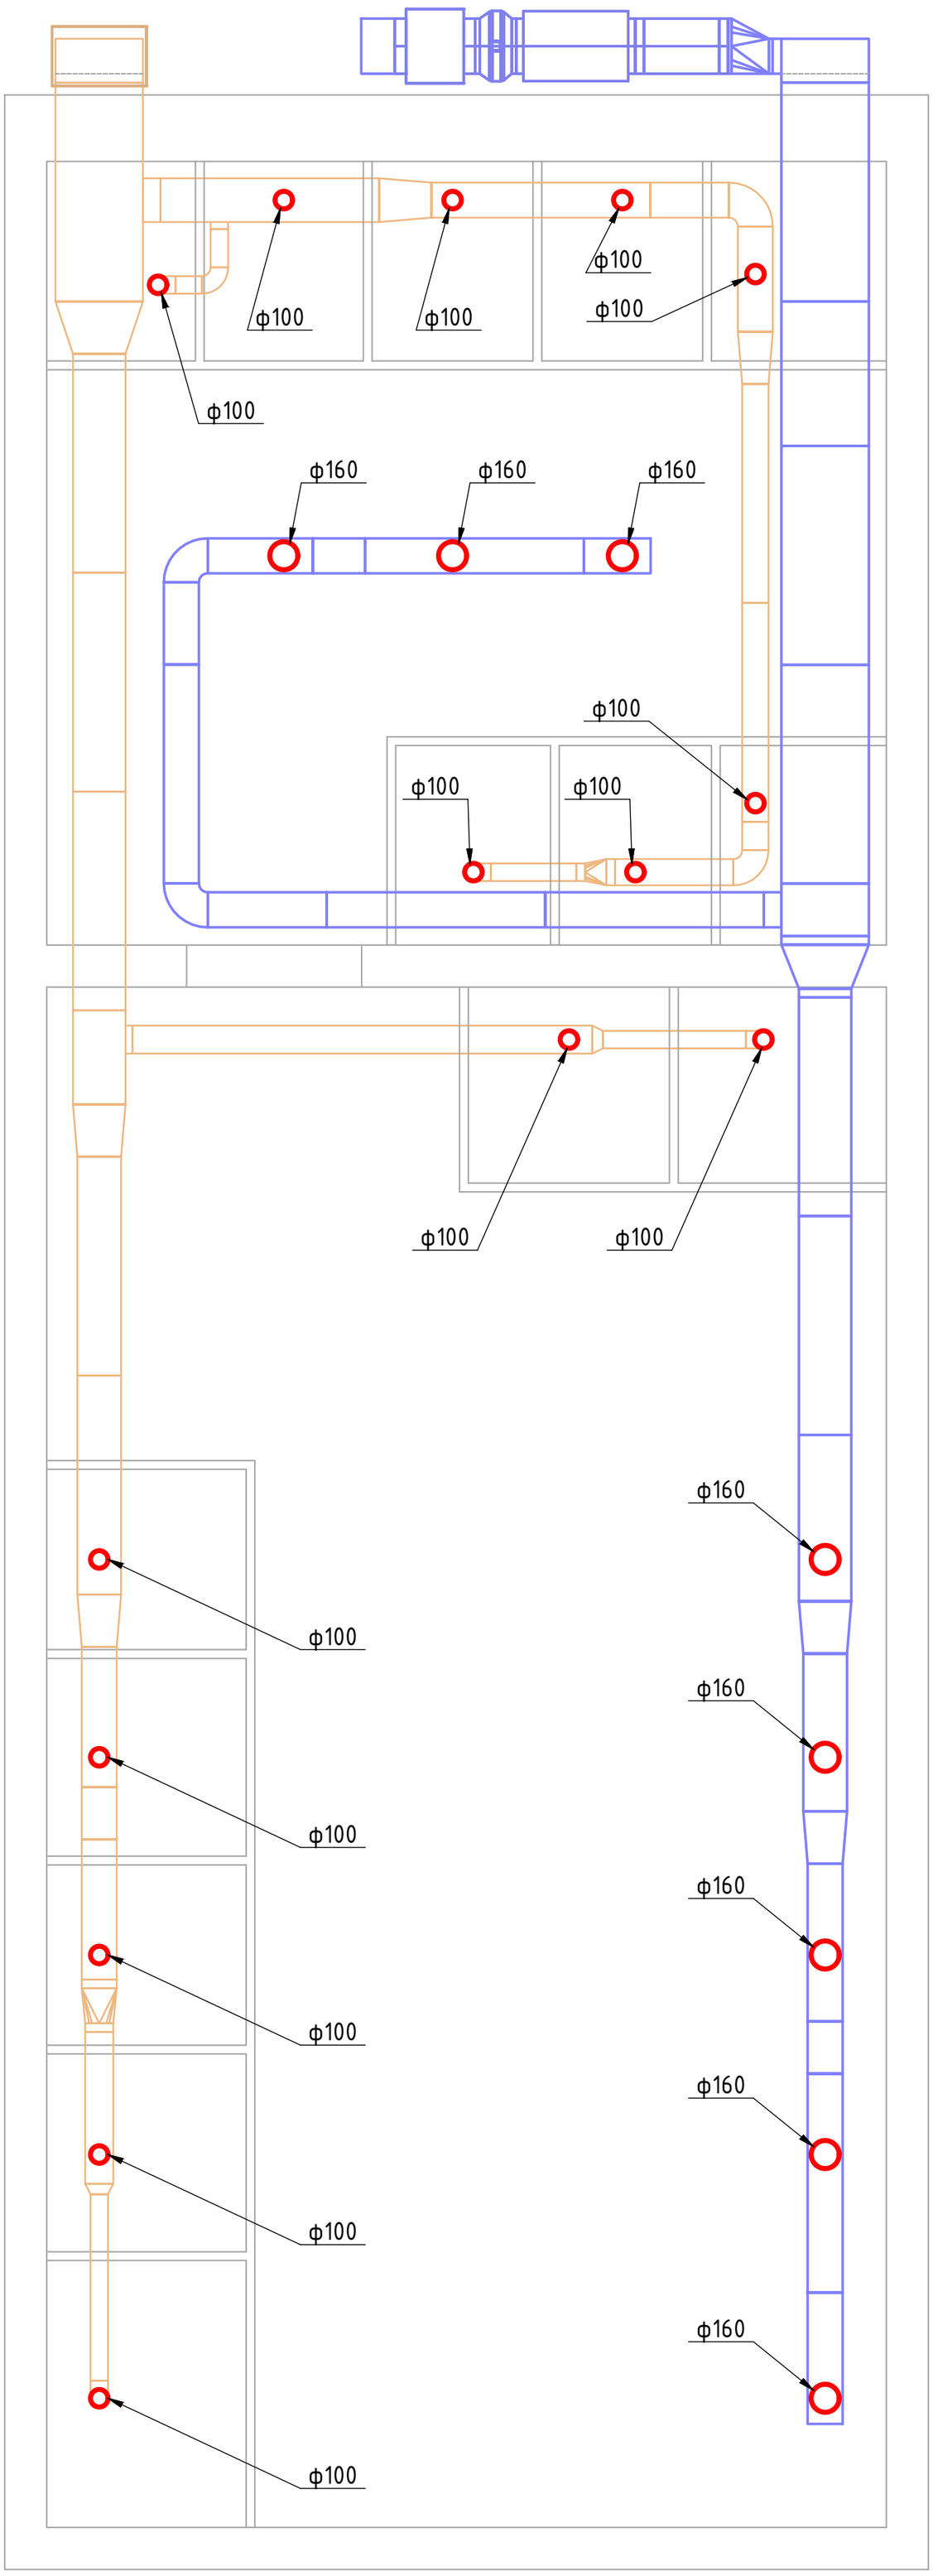

2. ПЛАН ПОТОЛОЧНЫХ РЕШЕТОК

Согласовано

Взам. инв. №

Подпись и дата

Инв. № подл.

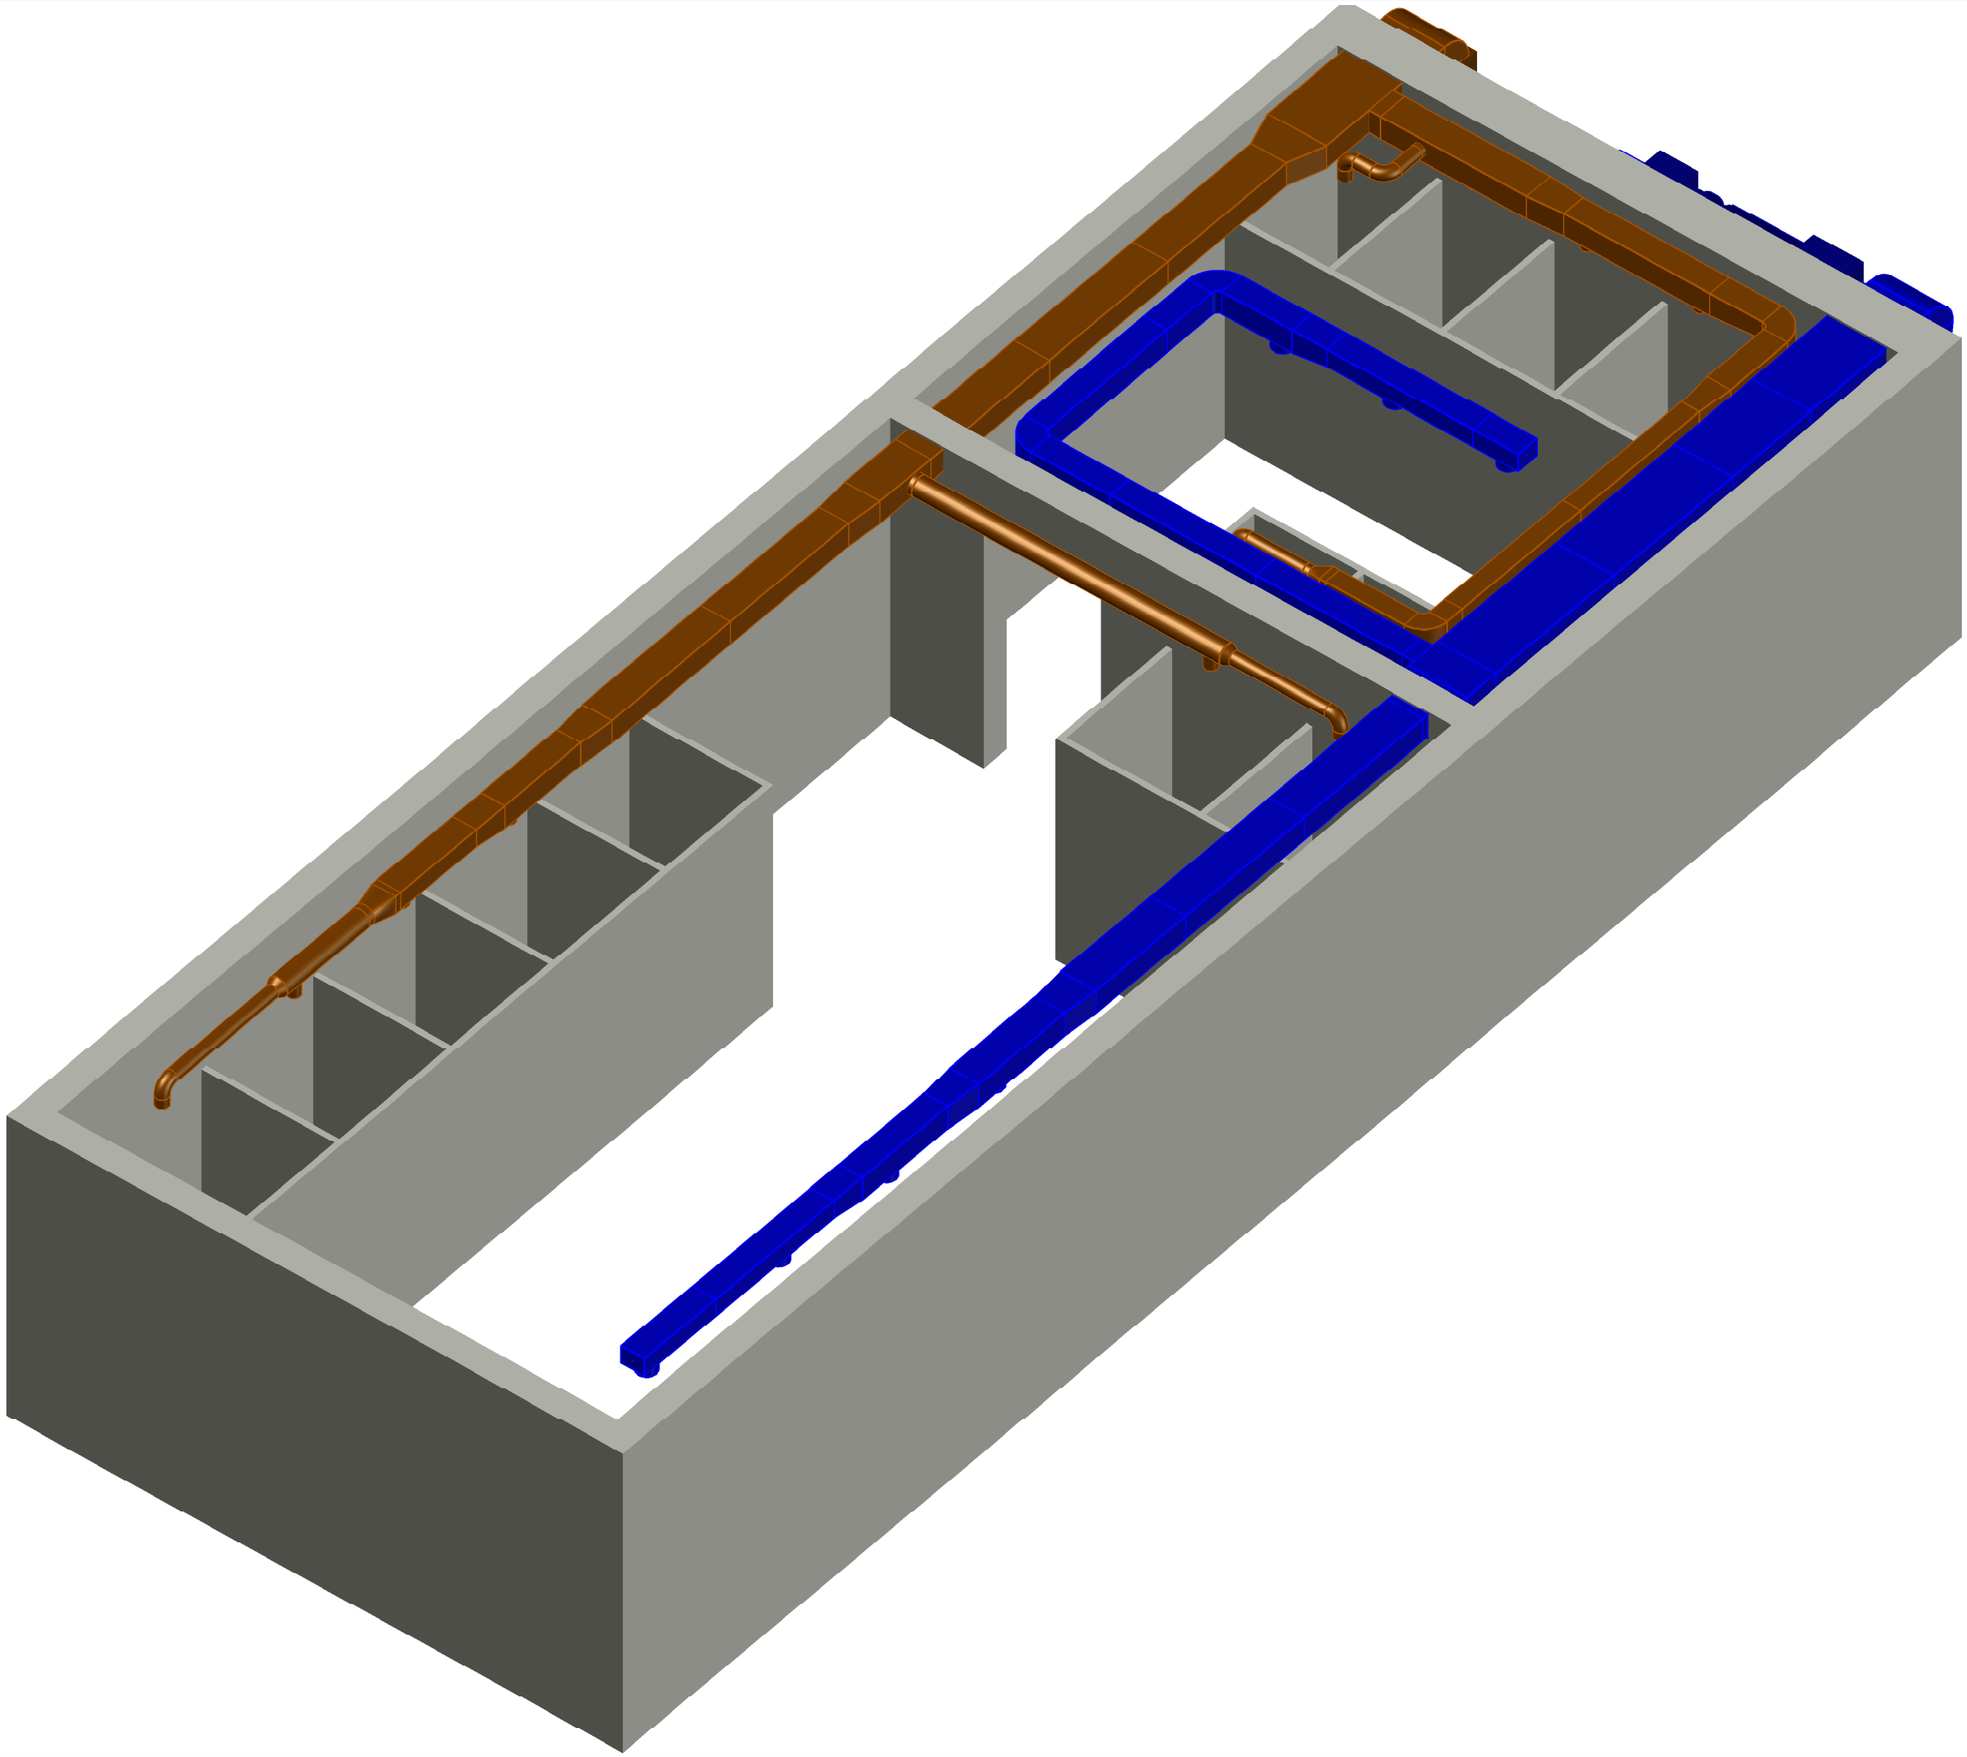

Согласовано

Взам. инв. №

Подпись и дата

Инв. № подл.

Копировал

Формат А3

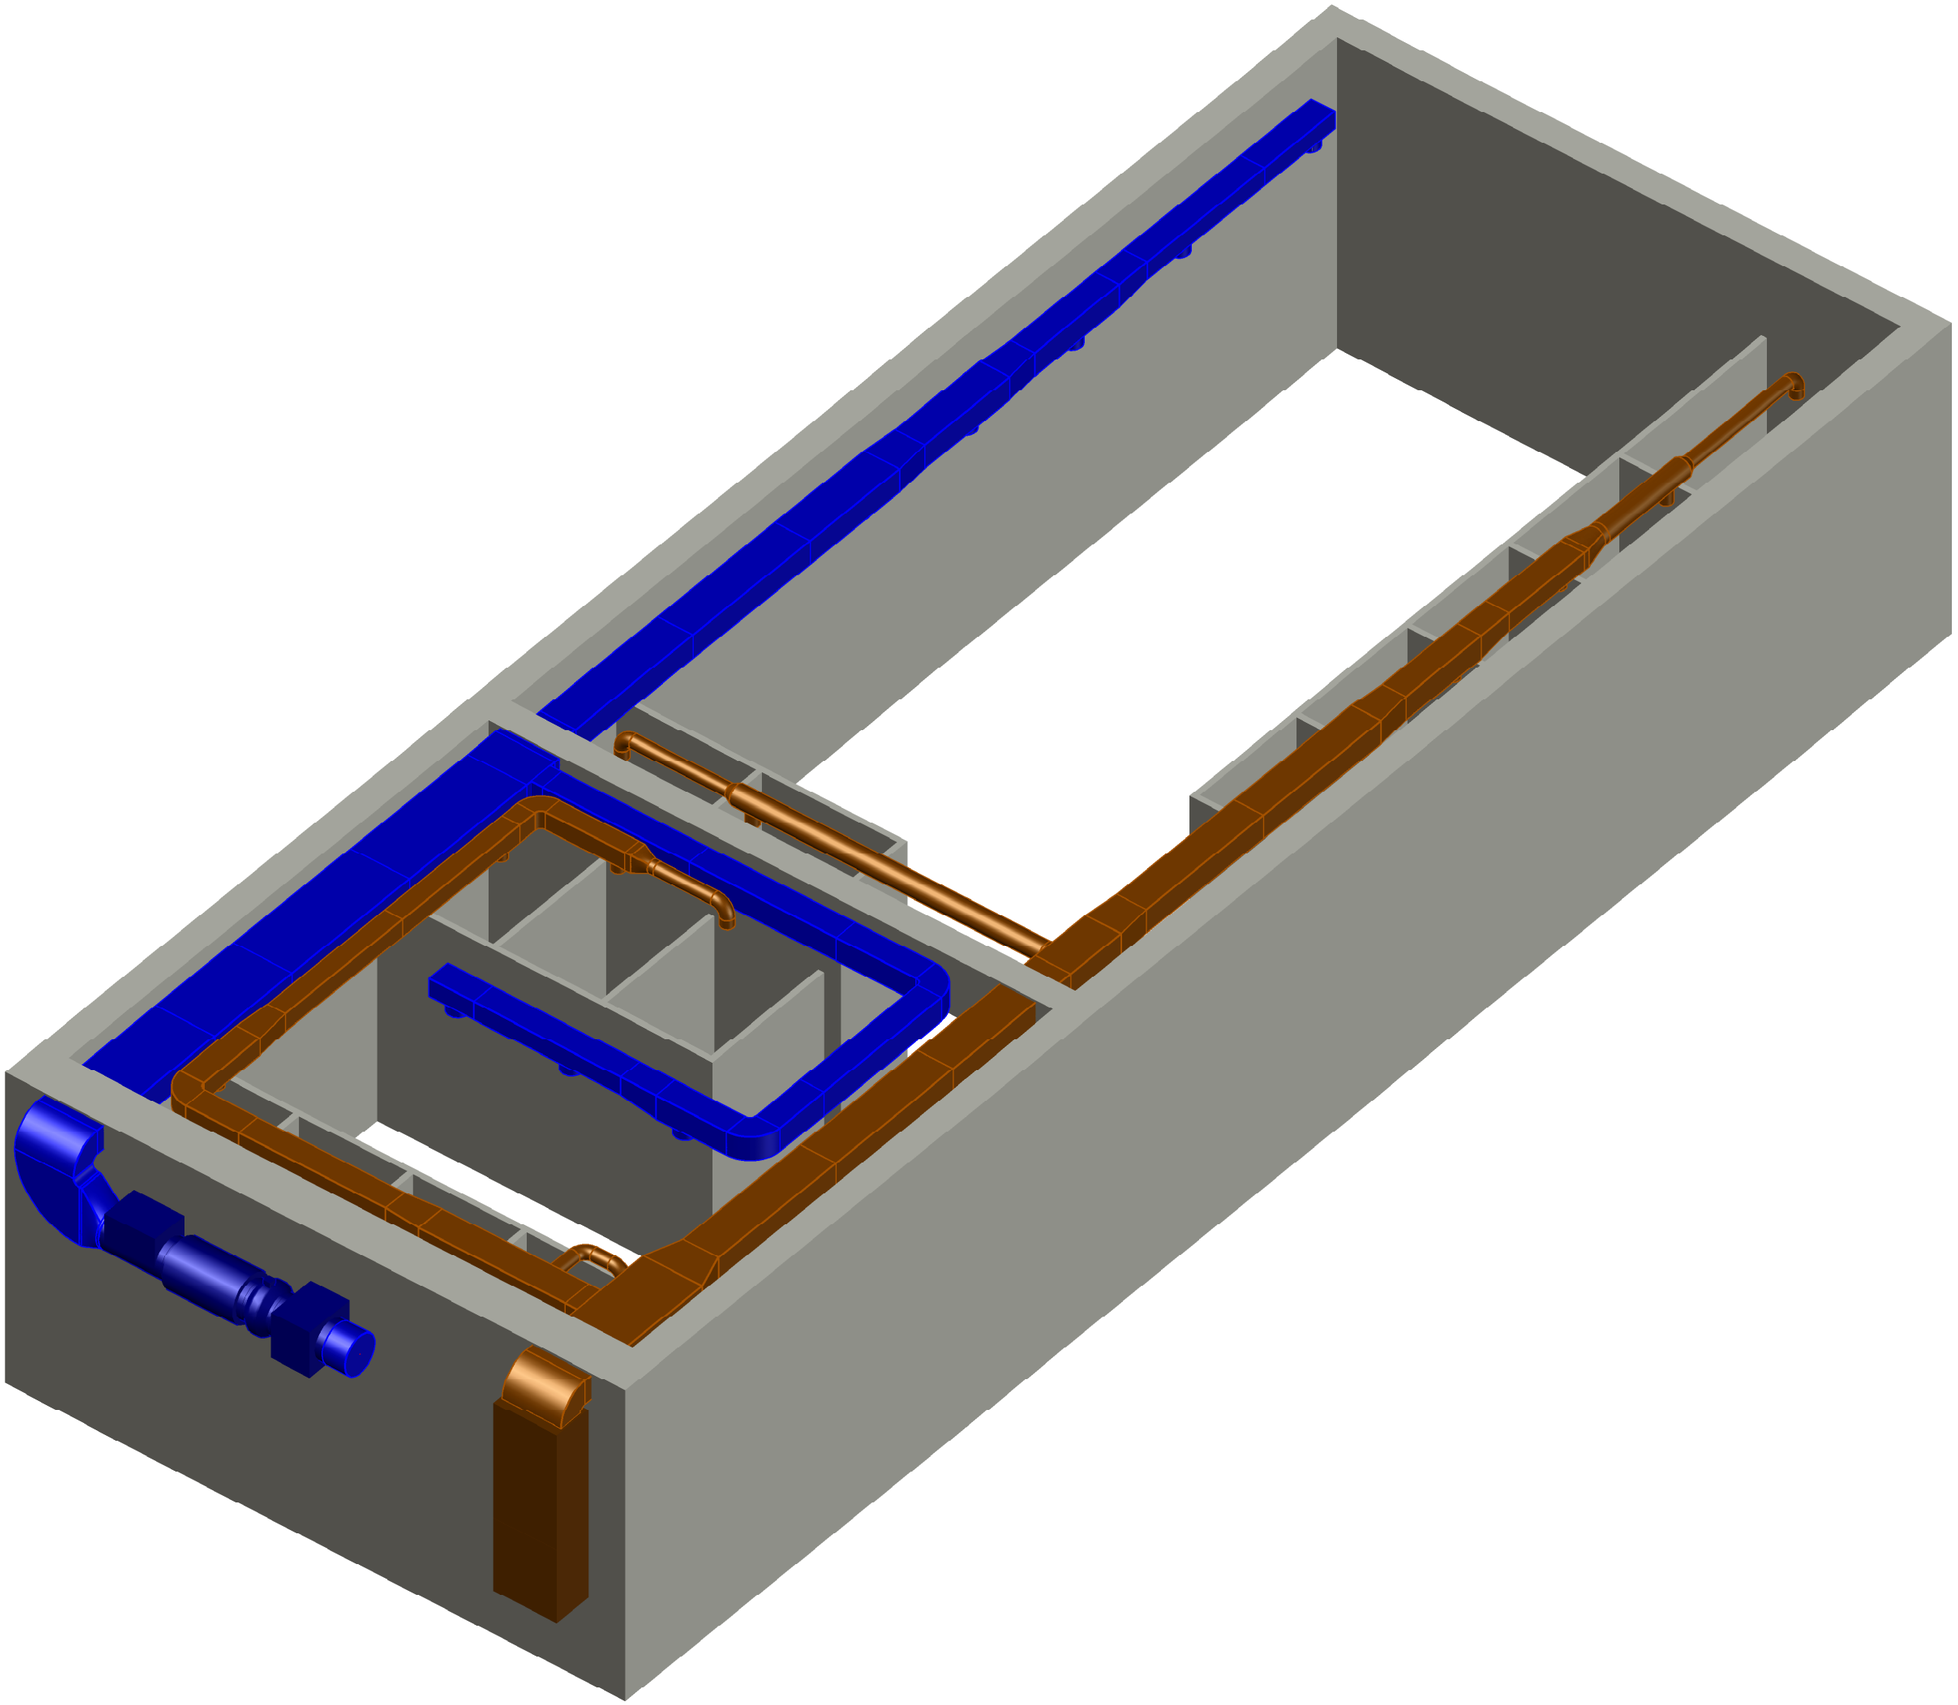

Согласовано

Взам. инв. №

Подпись и дата

Инв. № подл.

Копировал

Формат А3