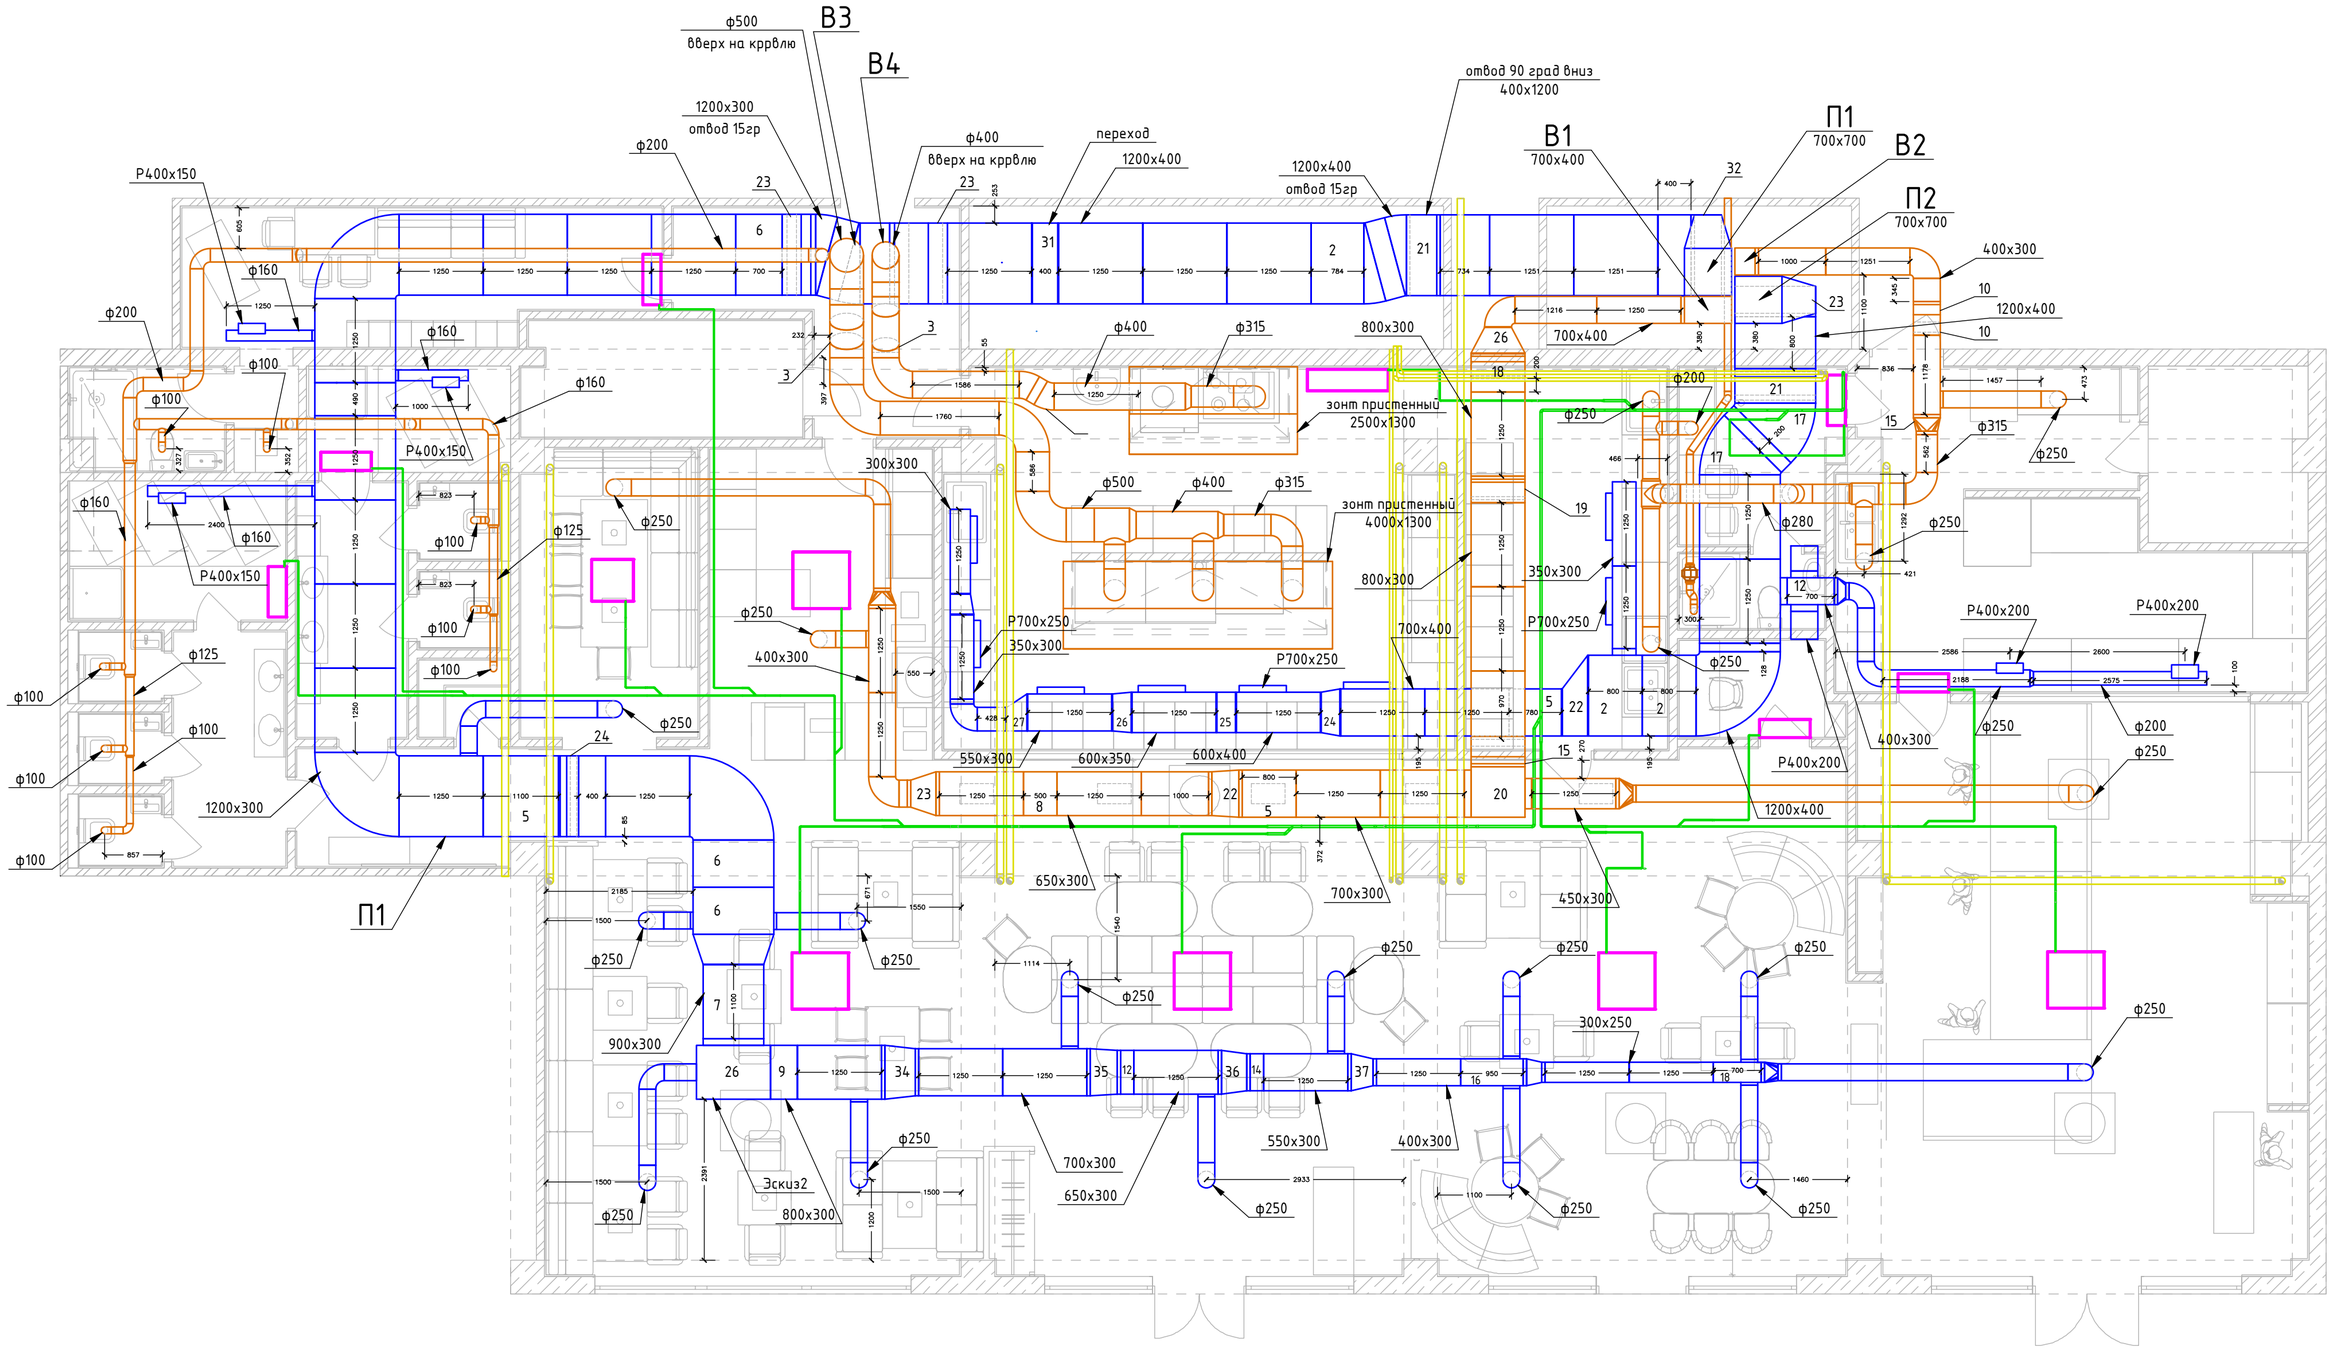

						ПД.05.2025-ОВ-ГТ-НН			
Изм.	Кол. уч.	Лист	№ док.	Подп.	Дата	Разработка проектной документации по вентиляции.			
Разработал						Ресторан в г. Махачкала	Стадия	Лист	Листов
Проверил							П	1	
ГИП						План систем вентиляции.			
Н.контроль									

Подп. и дата

Инв. № дубл.

Взам. инв. №

Подпись и дата

Инв. № подл.

Копировал

Формат А2

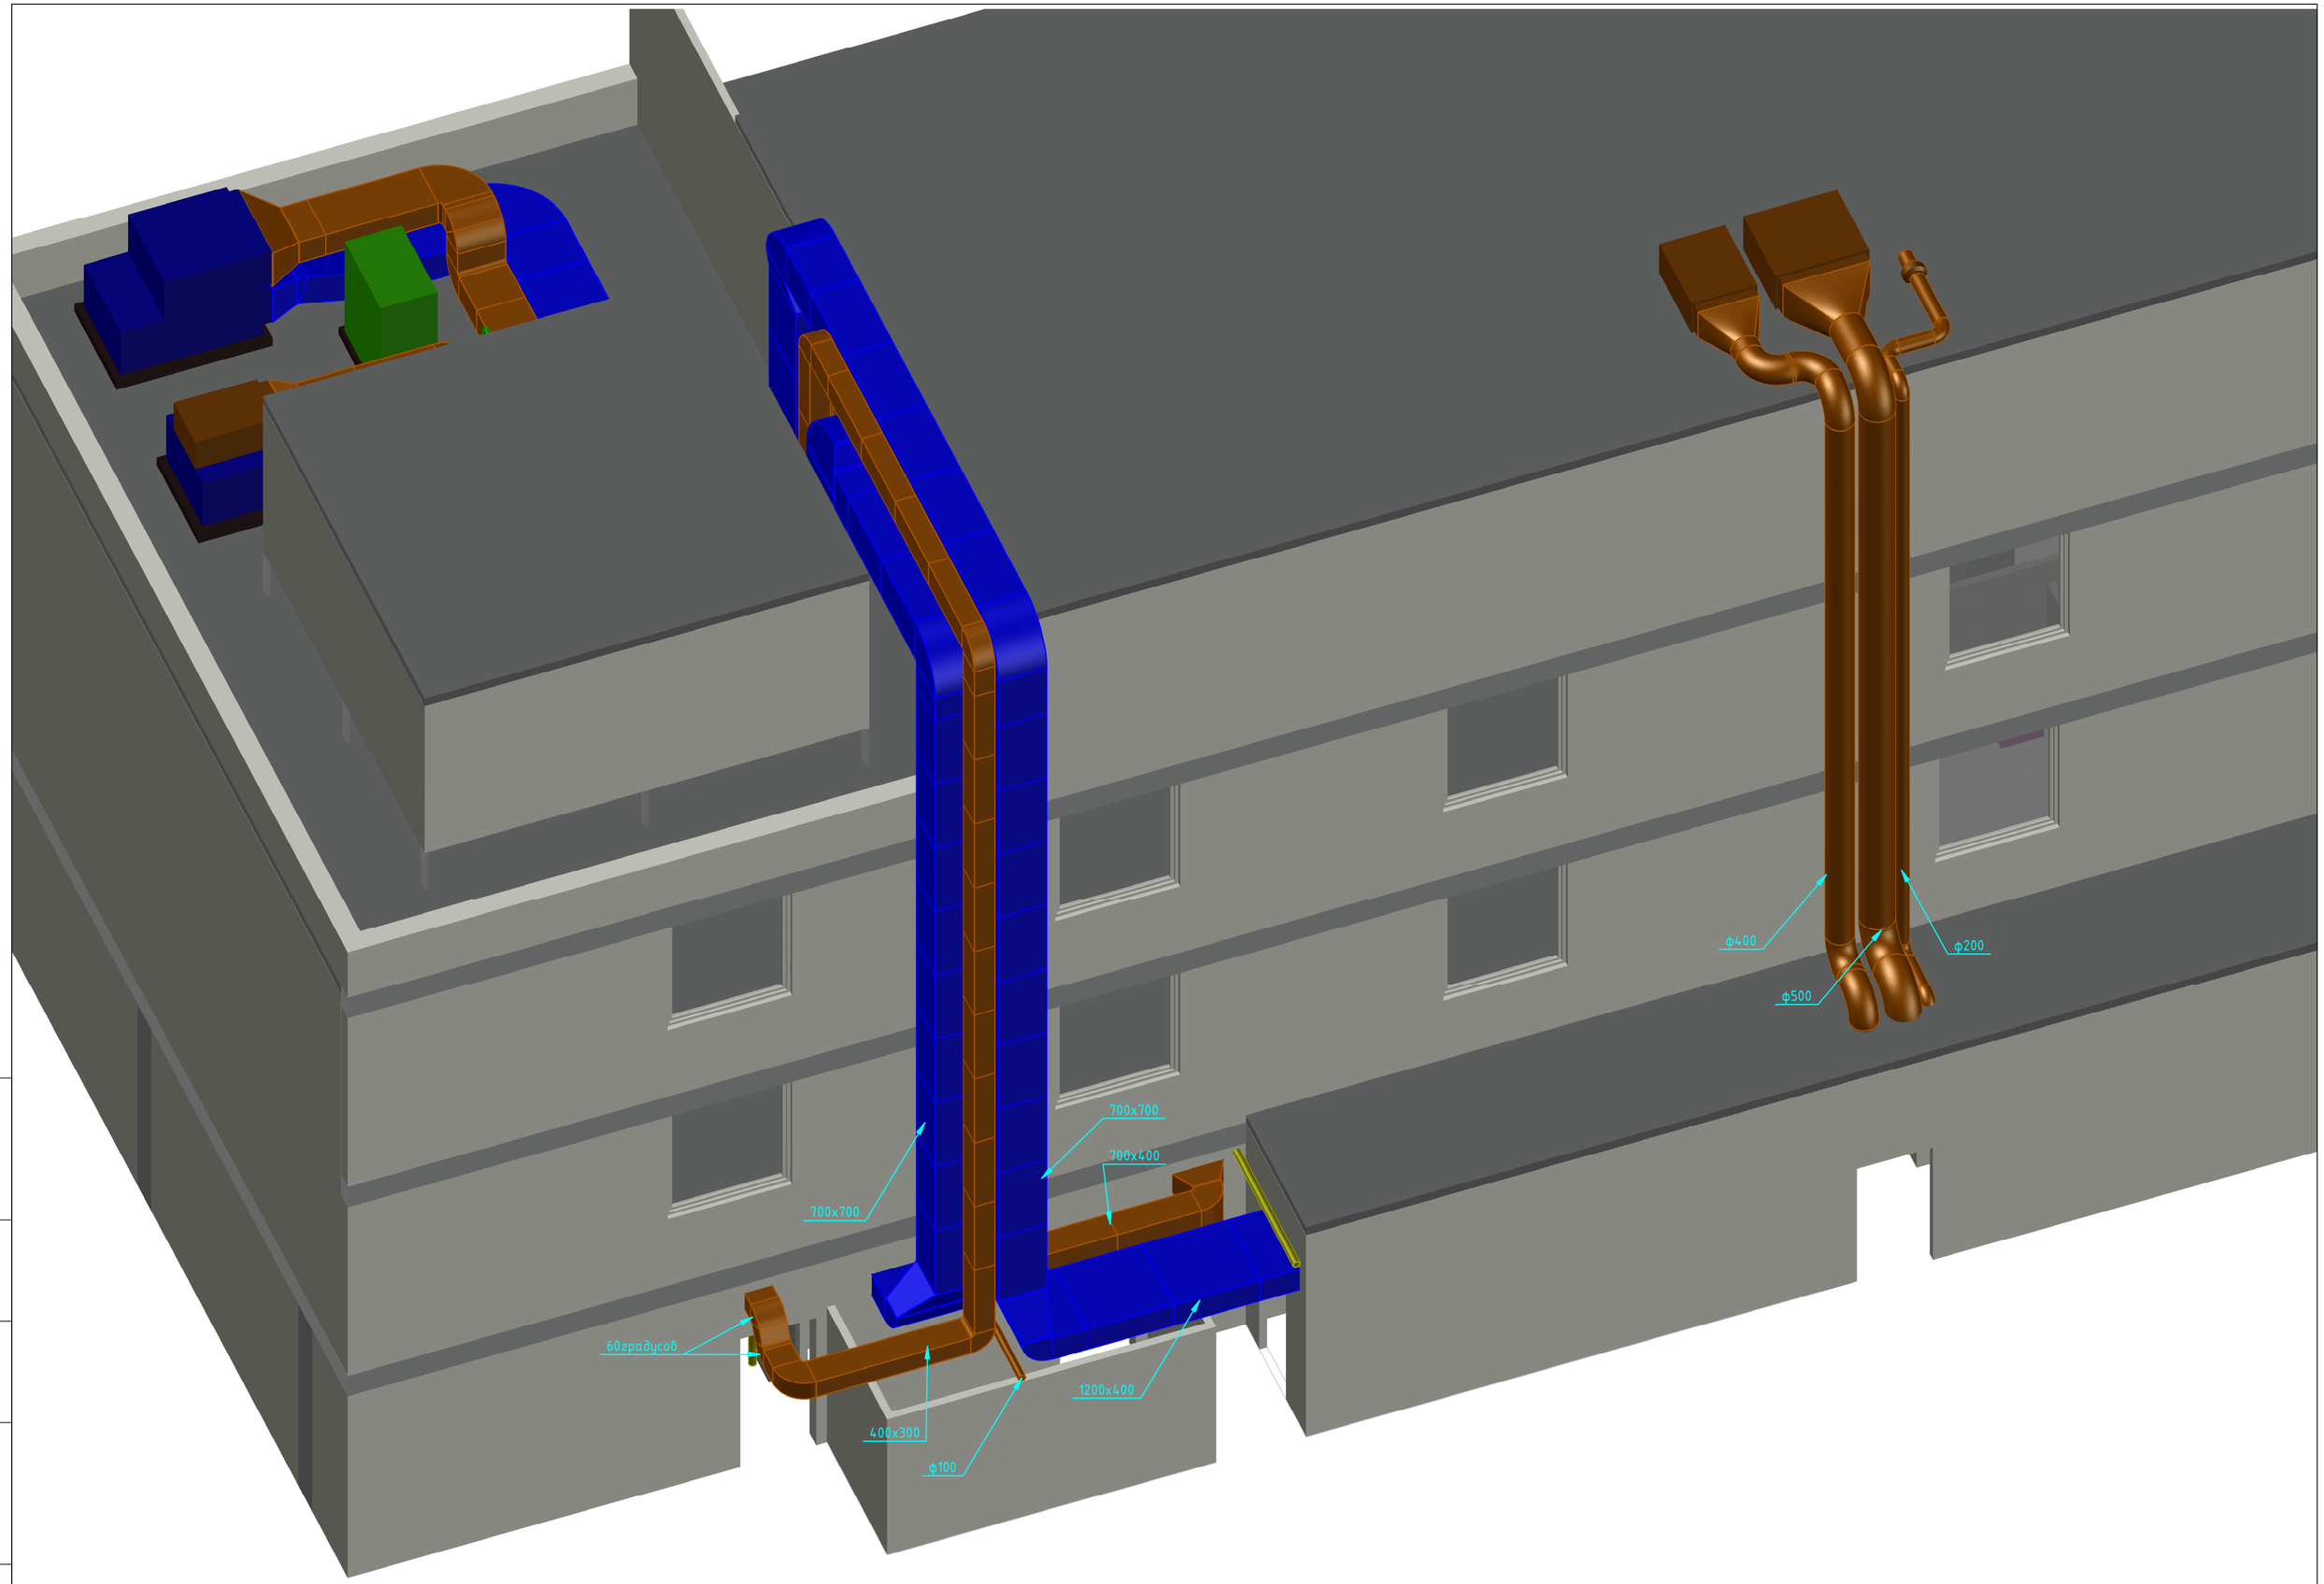

Подп. и дата

Инв. № дубл.

Взам. инв. №

Подпись и дата

Инв. № подл.

Копировал

Формат А2